

CASA ÁNGEL · ABERTURAS · 01. PLANTA ALTA · 07 COCINA

Hoja 1 de 1 · 3 elementos: V-157, V-158, MC-612302

Planta del local · códigos y anchos 1:50

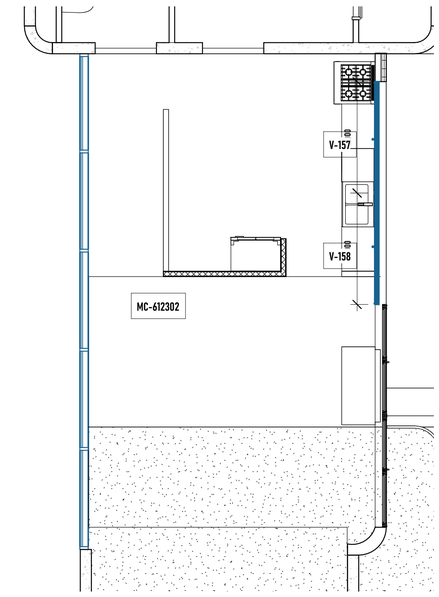


V-157 · alzado interior 1:20

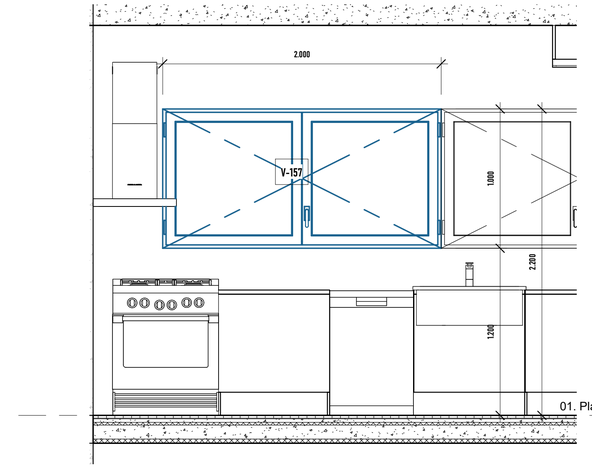


Aluprom 44 - 2 Hojas - Practicable - Ventanas
Ancho 2.000 - Alta 1.000 - Antepecho 1.200 - Dintel 2.200 m
Muro 0.200 m - Materiales: Aluminio, Cristal - Vidrio claro templado, Poliamida

V-158 · alzado interior 1:20

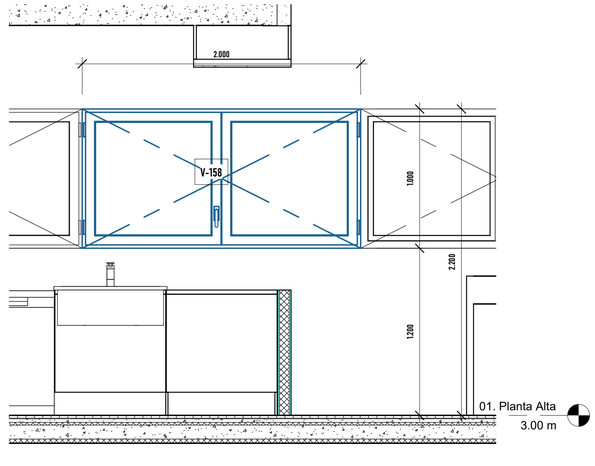

Aluprom 44 - 2 Hojas - Practicable - Ventanas
Ancho 2.000 - Alta 1.000 - Antepecho 1.200 - Dintel 2.200 m
Muro 0.200 m - Materiales: Aluminio, Cristal - Vidrio claro templado, Poliamida

MC-612302 · alzado interior 1:30

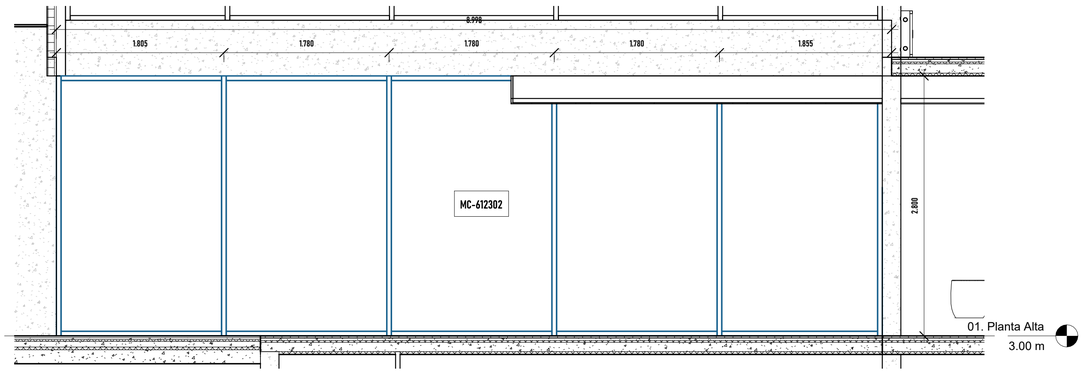

Muro cortina - Ventanales Patio - 5 paneles / 16 montantes
Largo 8.998 - Alto 2.800 - Arranque +0.000 - Superior +2.800 m
Muro 0.025 m
Compartida con: Living (computar una vez)

Cotas en metros (0.001 m) sobre geometría nativa. Cotas de muros cortina: referidas a ejes de grilla y extremos del conjunto (no asociativas). Alzados vistos desde el interior del local. Elementos compartidos entre locales: un solo cómputo por código.

https://ezeader.myportfolio.com/ezequiel-ader

Consultant
Address
Address
Phone
Fax
e-mail

Consultant
Address
Address
Phone
Fax
e-mail

Consultant
Address
Address
Phone
Fax
e-mail

Consultant
Address
Address
Phone
Fax
e-mail

No.	Description	Date

Angel Luis Brusca

CASA ANGEL

ABR-R4-PA-07

Project number	0001
Date	18 de Agosto, 2025
Drawn by	Author
Checked by	Checker

Cocina · ABR

Scale: As indicated

10/23/2026 2:56:15 PM