

# CASA ÁNGEL · ABERTURAS · 01. PLANTA ALTA · 09 LIVING

Hoja 1 de 1 · 1 elementos: MC-612302

Planta del local · códigos y anchos 1:40

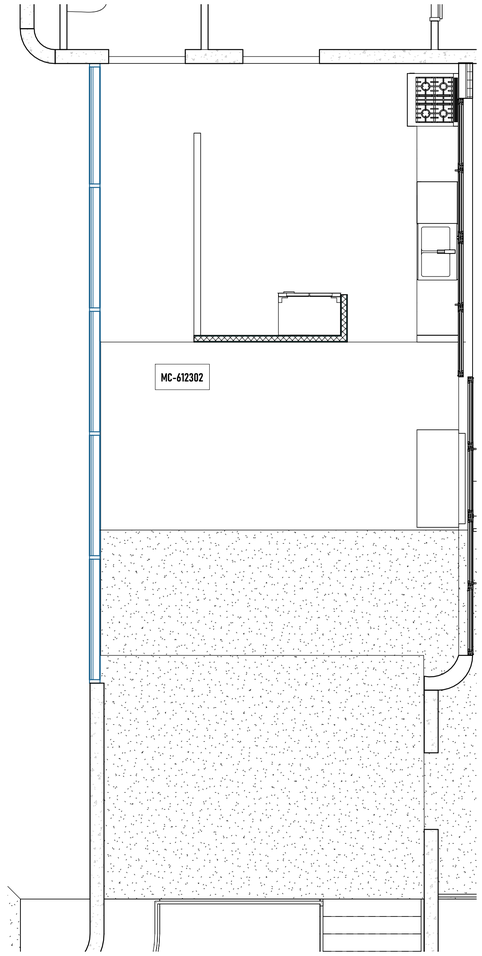


MC-612302 · alzado interior 1:30

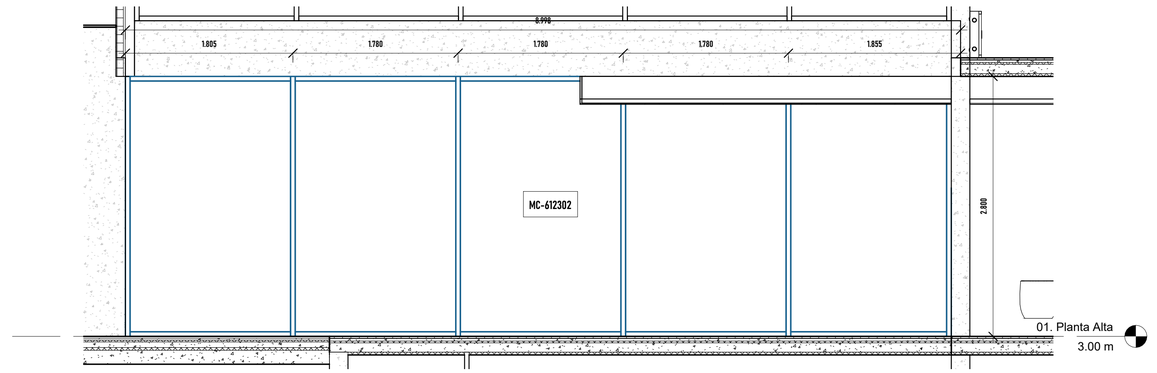


Muro cortina - Ventanales Patio - 5 paneles / 16 montantes
Largo 8.998 - Alto 2.800 - Arranque +0.000 - Superior +2.800 m
Muro 0.025 m
Compartida con: Cocina (computar una vez)

Cotas en metros (0.001 m) sobre geometría nativa. Cotas de muros cortina: referidas a ejes de grilla y extremos del conjunto (no asociativas). Alzados vistos desde el interior del local. Elementos compartidos entre locales: un solo cómputo por código.

https://ezeader.myportfolio.com/ezequiel-ader


Consultant
Address
Address
Phone
Fax
e-mail

Consultant
Address
Address
Phone
Fax
e-mail

Consultant
Address
Address
Phone
Fax
e-mail

Consultant
Address
Address
Phone
Fax
e-mail


| No. | Description | Date |
|---|---|---|

Angel Luis Brusca

CASA ANGEL

ABR-R4-PA-09

| | |
|---|---|
| Project number | 0001 |
| Date | 18 de Agosto, 2025 |
| Drawn by | Author |
| Checked by | Checker |

Living · ABR

Scale As indicated

10/23/2026 2:56:32 PM