

CASA ÁNGEL · ABERTURAS · 00. PLANTA BAJA · 12 QUINCHO

Hoja 1 de 2 · 1 elementos: MC-1046997

Planta del local · 12 · Quincho 1:30

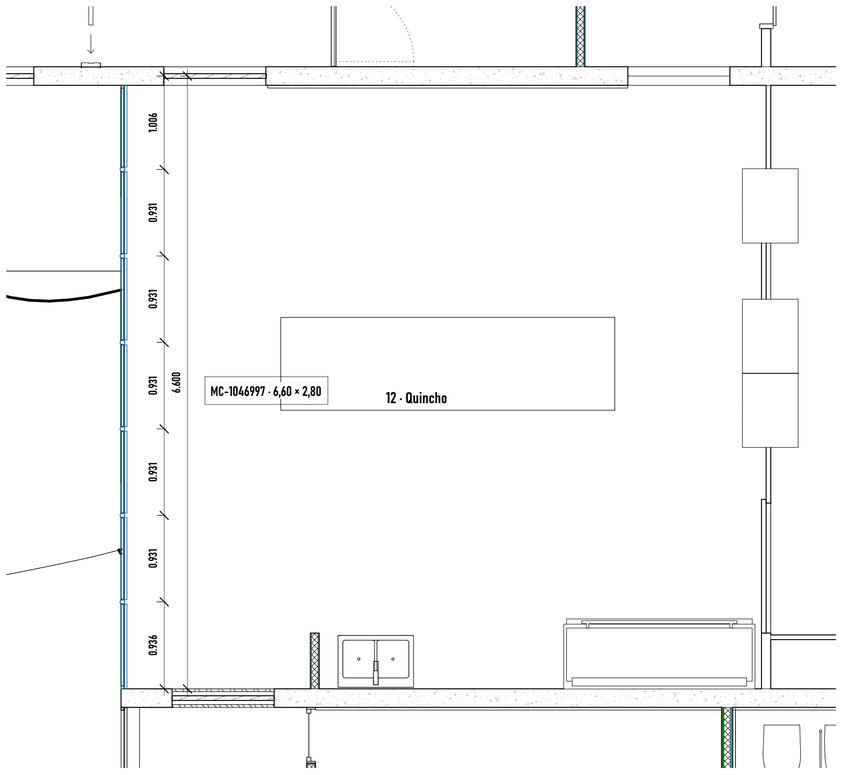

Axonométrica del local · 12 · Quincho 1:40

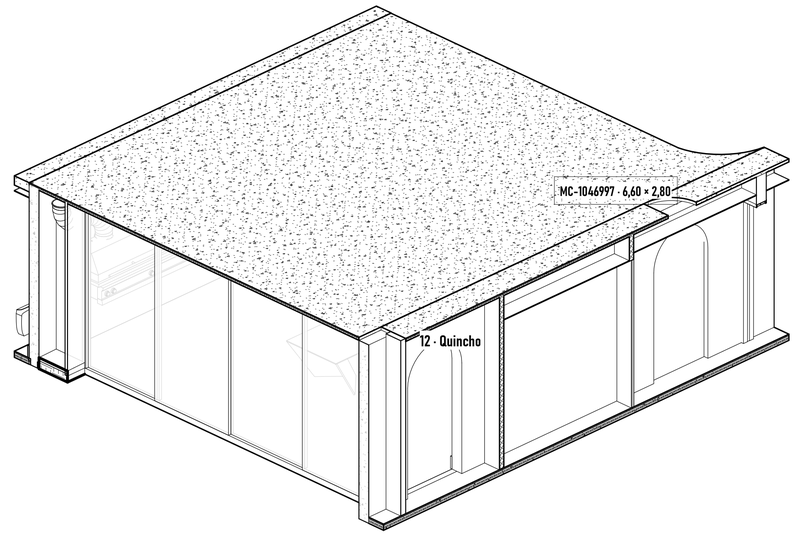

Cotas en metros (0.001 m) sobre geometría nativa. Cotas de muros cortina y cápsula del ascensor: referidas a ejes de grilla, extremos y centros de arcos (no asociativas, salvo radios). Alzados vistos desde el interior del local. Elementos compartidos entre locales: un solo cómputo por código.

https://ezeader.myportfolio.com/ezequiel-ader

Consultant
Address
Address
Phone
Fax
e-mail

Consultant
Address
Address
Phone
Fax
e-mail

Consultant
Address
Address
Phone
Fax
e-mail

Consultant
Address
Address
Phone
Fax
e-mail

No.	Description	Date

Angel Luis Brusca

CASA ANGEL

ABR-R4-PB-12

Project number	0001
Date	18 de Agosto, 2025
Drawn by	Author
Checked by	Checker

Quincho · ABR 1/2


Scale 1 : 30

10/23/2026 4:54:47 PM

CASA ÁNGEL · ABERTURAS · 00. PLANTA BAJA · 12 QUINCHO

Hoja 2 de 2 · 1 elementos: MC-1046997

MC-1046997 · alzado interior 1:15

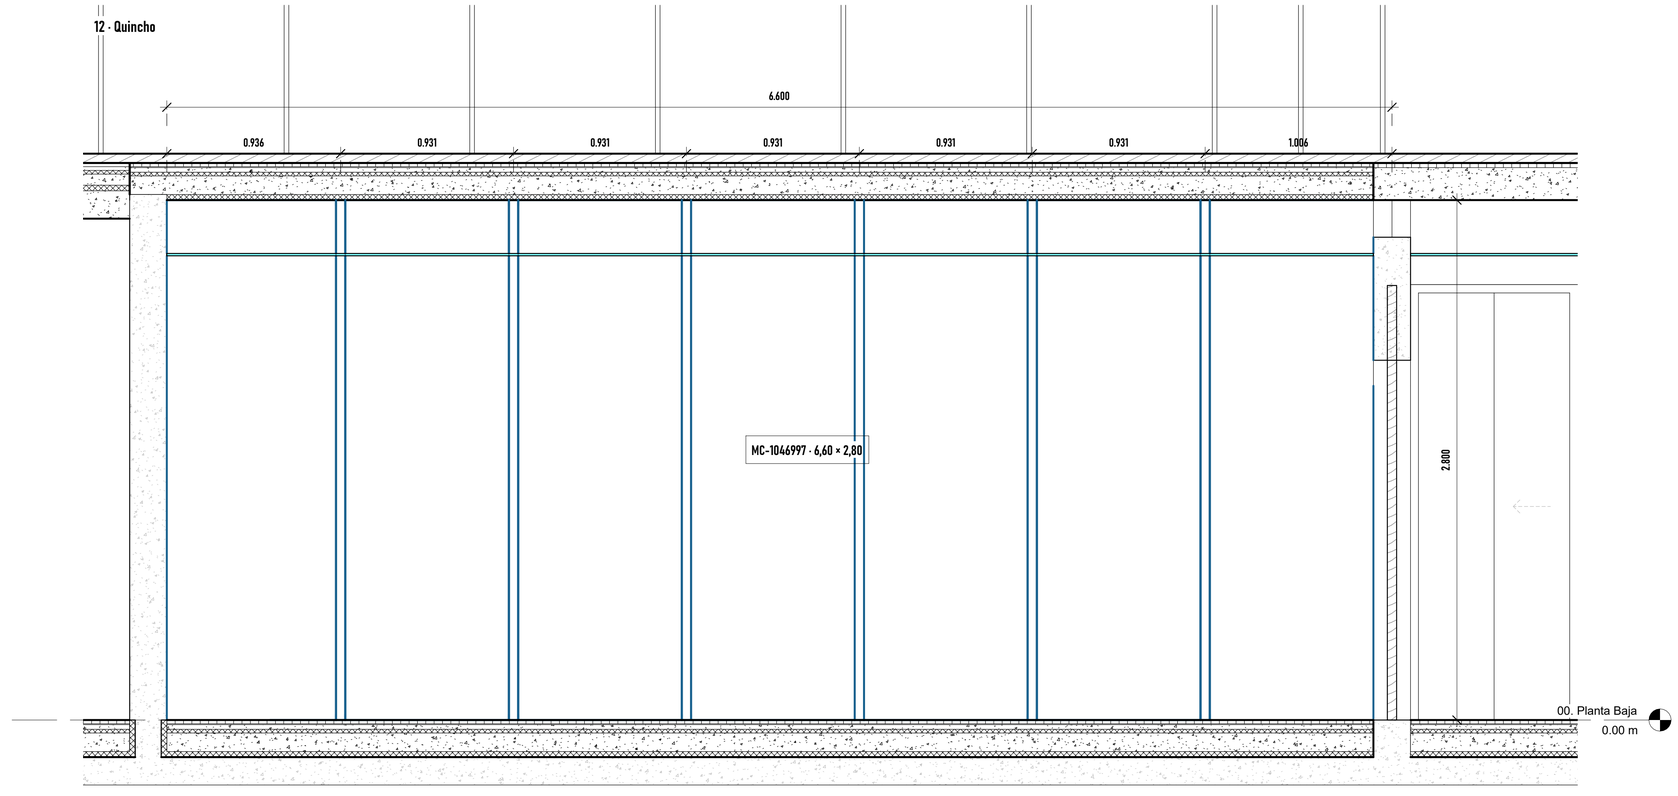

Muro cortina · Vent. Corrediza PB · 7 paneles / 22 montantes
Largo 6.600 · Alto 2.800 · Arranque +0.000 · Superior +2.800 m
Muro 0.025 m

Cotas en metros (0.001 m) sobre geometría nativa. Cotas de muros cortina y cápsula del ascensor: referidas a ejes de grilla, extremos y centros de arcos (no asociativas, salvo radios). Alzados vistos desde el interior del local. Elementos compartidos entre locales: un solo cómputo por código.

https://ezeader.myportfolio.com/ezequiel-ader

Consultant
Address
Address
Phone
Fax
e-mail

Consultant
Address
Address
Phone
Fax
e-mail

Consultant
Address
Address
Phone
Fax
e-mail

Consultant
Address
Address
Phone
Fax
e-mail

No.	Description	Date

Angel Luis Brusca

CASA ANGEL

ABR-R4-PB-12-2

Project number	0001
Date	18 de Agosto, 2025
Drawn by	Author
Checked by	Checker

Quincho · ABR 2/2

Scale	1 : 15

10/23/2026 4:54:47 PM