

CASA ÁNGEL · ABERTURAS · 00. PLANTA BAJA · 16 PASILLO

Hoja 1 de 6 · 9 elementos: V-92, V-123, V-154, P-31, P-63, P-94, MC-1045585, MC-1046251, MC-1046631

Planta del local · 16 · Pasillo 1:40

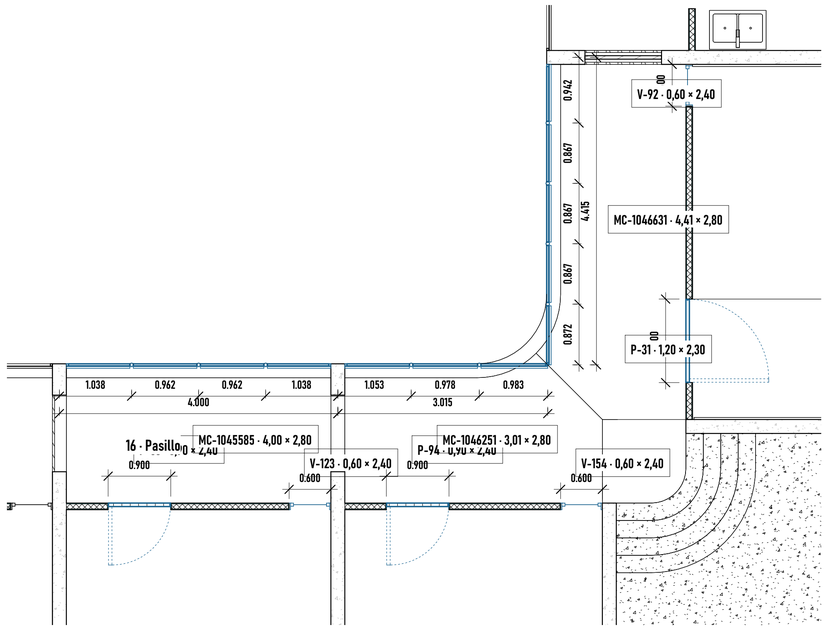

Axonométrica del local · 16 · Pasillo 1:50

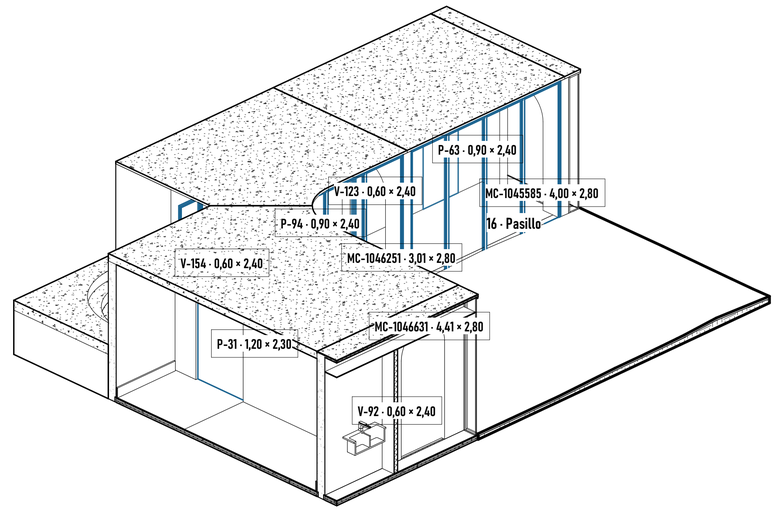

Cotas en metros (0.001 m) sobre geometría nativa. Cotas de muros cortina y cápsula del ascensor: referidas a ejes de grilla, extremos y centros de arcos (no asociativas, salvo radios). Alzados vistos desde el interior del local. Elementos compartidos entre locales: un solo cómputo por código.

https://ezeader.myportfolio.com/ezequiel-ader

Consultant
Address
Address
Phone
Fax
e-mail

Consultant
Address
Address
Phone
Fax
e-mail

Consultant
Address
Address
Phone
Fax
e-mail

Consultant
Address
Address
Phone
Fax
e-mail

No.	Description	Date

Angel Luis Brusca

CASA ANGEL

ABR-R4-PB-16

Project number	0001
Date	18 de Agosto, 2025
Drawn by	Author
Checked by	Checker

Pasillo · ABR 1/6


Scale 1 : 40

10/23/2026 4:57:12 PM

CASA ÁNGEL · ABERTURAS · 00. PLANTA BAJA · 16 PASILLO


Hoja 2 de 6 · 9 elementos: V-92, V-123, V-154, P-31, P-63, P-94, MC-1045585, MC-1046251, MC-1046631

V-92 · alzado interior 1:15

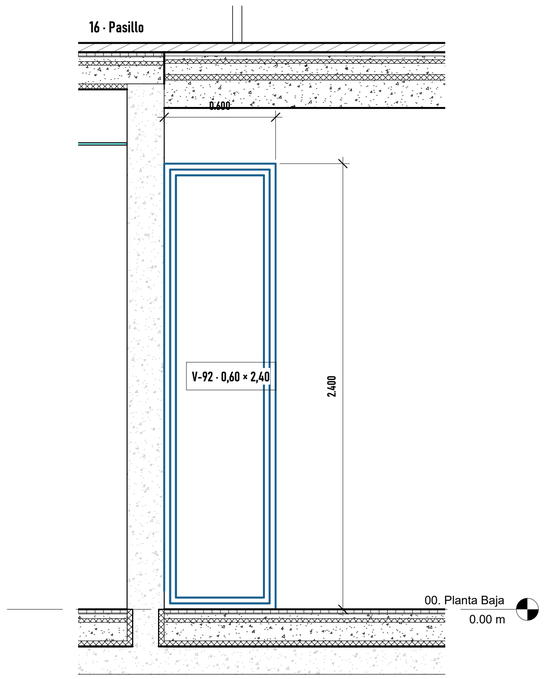

Ventana Cuartos (Muro a techo) · M_Fixed
Ancho 0.600 · Alto 2.400 · Antepecho 0.000 · Dintel 2.400 m
Tipo muro a techo: piso terminado a dintel 2.400 m (verificar con cielorraso)
Muro 0.095 m · Materiales: Glass, Sash
Compartida con: Cuarto ppal (computar una vez)

V-123 · alzado interior 1:15

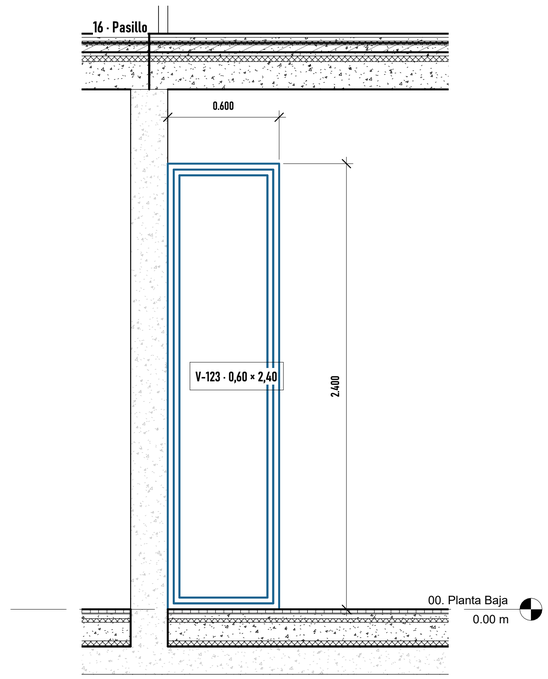

Ventana Cuartos (Muro a techo) · M_Fixed
Ancho 0.600 · Alto 2.400 · Antepecho 0.000 · Dintel 2.400 m
Tipo muro a techo: piso terminado a dintel 2.400 m (verificar con cielorraso)
Muro 0.095 m · Materiales: Glass, Sash
Compartida con: Cuarto B Inv. (computar una vez)

Cotas en metros (0.001 m) sobre geometría nativa. Cotas de muros cortina y cápsula del ascensor: referidas a ejes de grilla, extremos y centros de arcos (no asociativas, salvo radios). Alzados vistos desde el interior del local. Elementos compartidos entre locales: un solo cómputo por código.

https://ezeader.myportfolio.com/ezequiel-ader

Consultant
Address
Address
Phone
Fax
e-mail

Consultant
Address
Address
Phone
Fax
e-mail

Consultant
Address
Address
Phone
Fax
e-mail

Consultant
Address
Address
Phone
Fax
e-mail

No.	Description	Date

Angel Luis Brusca

CASA ANGEL

ABR-R4-PB-16-2

Project number	0001
Date	18 de Agosto, 2025
Drawn by	Author
Checked by	Checker

Pasillo · ABR 2/6


Scale 1 : 15

10/23/2026 4:57:12 PM

CASA ÁNGEL · ABERTURAS · 00. PLANTA BAJA · 16 PASILLO


Hoja 3 de 6 · 9 elementos: V-92, V-123, V-154, P-31, P-63, P-94, MC-1045585, MC-1046251, MC-1046631

V-154 · alzado interior 1:15

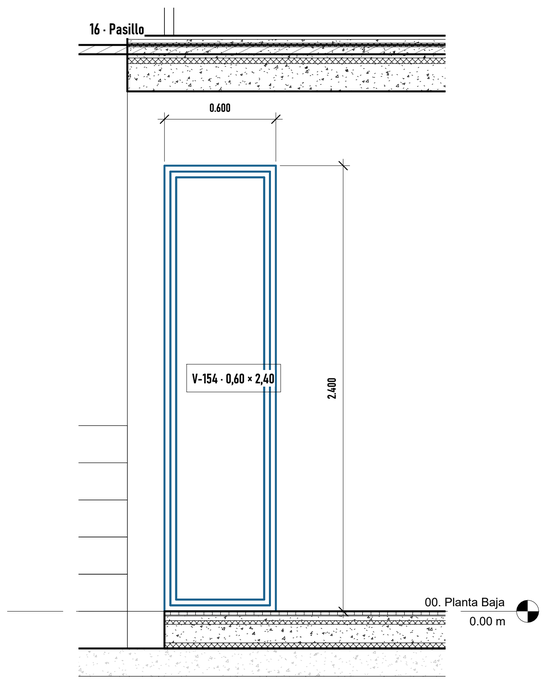

Ventana Cuartos (Muro a techo) · M_Fixed
Ancho 0.600 · Alto 2.400 · Antepecho 0.000 · Dintel 2.400 m
Tipo muro a techo: piso terminado a dintel 2.400 m (verificar con cielorraso)
Muro 0.095 m · Materiales: Glass, Sash
Compartida con: Cuarto C Inv. (computar una vez)

P-31 · alzado interior 1:15

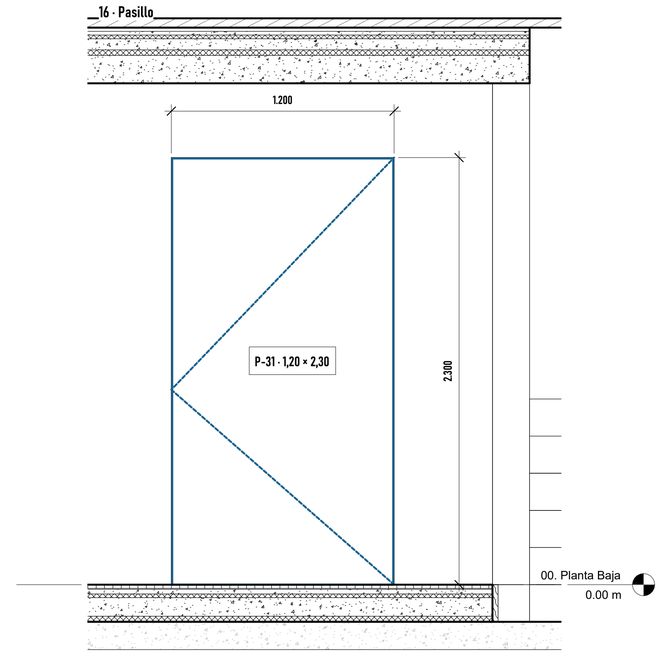

1.20 M - JALO_PUERTA ABATIBLE
Ancho 1.200 · Alto 2.300 · Antepecho 0.000 · Dintel 2.300 m
Muro 0.095 m
Compartida con: Vestidor ppal (computar una vez)

Cotas en metros (0.001 m) sobre geometría nativa. Cotas de muros cortina y cápsula del ascensor: referidas a ejes de grilla, extremos y centros de arcos (no asociativas, salvo radios). Alzados vistos desde el interior del local. Elementos compartidos entre locales: un solo cómputo por código.

https://ezeader.myportfolio.com/ezequiel-ader

Consultant
Address
Address
Phone
Fax
e-mail

Consultant
Address
Address
Phone
Fax
e-mail

Consultant
Address
Address
Phone
Fax
e-mail

Consultant
Address
Address
Phone
Fax
e-mail

No.	Description	Date

Angel Luis Brusca

CASA ANGEL

ABR-R4-PB-16-3

Project number	0001
Date	18 de Agosto, 2025
Drawn by	Author
Checked by	Checker

Pasillo · ABR 3/6


Scale 1 : 15

10/23/2026 4:57:13 PM

CASA ÁNGEL · ABERTURAS · 00. PLANTA BAJA · 16 PASILLO


Hoja 4 de 6 · 9 elementos: V-92, V-123, V-154, P-31, P-63, P-94, MC-1045585, MC-1046251, MC-1046631

P-63 · alzado interior 1:15

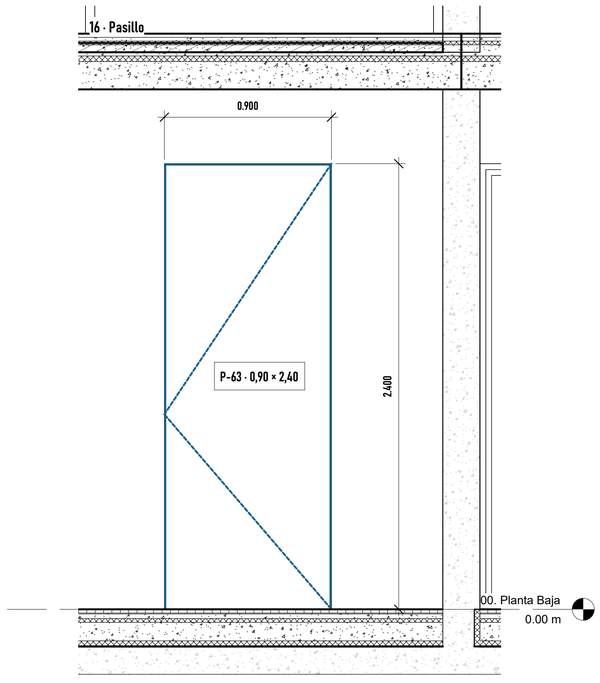

0.90 M · JALO_PUERTA ABATIBLE
Ancho 0.900 · Alto 2.400 · Antepecho 0.000 · Dintel 2.400 m
Muro 0.095 m · Materiales: Puertas
Compartida con: Cuarto B Inv. (computar una vez)

P-94 · alzado interior 1:15

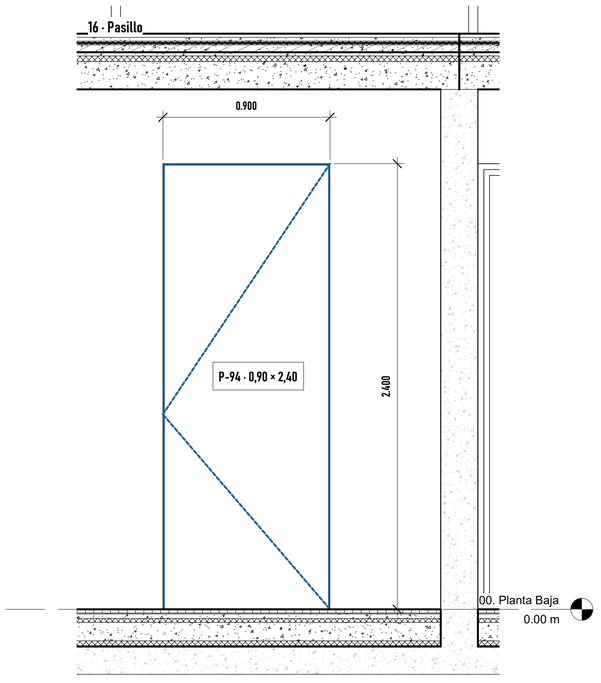

0.90 M · JALO_PUERTA ABATIBLE
Ancho 0.900 · Alto 2.400 · Antepecho 0.000 · Dintel 2.400 m
Muro 0.095 m · Materiales: Puertas
Compartida con: Cuarto C Inv. (computar una vez)

Cotas en metros (0.001 m) sobre geometría nativa. Cotas de muros cortina y cápsula del ascensor: referidas a ejes de grilla, extremos y centros de arcos (no asociativas, salvo radios). Alzados vistos desde el interior del local. Elementos compartidos entre locales: un solo cómputo por código.

https://ezeader.myportfolio.com/ezequiel-ader

Consultant
Address
Address
Phone
Fax
e-mail

Consultant
Address
Address
Phone
Fax
e-mail

Consultant
Address
Address
Phone
Fax
e-mail

Consultant
Address
Address
Phone
Fax
e-mail

No.	Description	Date

Angel Luis Brusca

CASA ANGEL

ABR-R4-PB-16-4

Project number	0001
Date	18 de Agosto, 2025
Drawn by	Author
Checked by	Checker

Pasillo · ABR 4/6


Scale 1 : 15

10/23/2026 4:57:14 PM

CASA ÁNGEL · ABERTURAS · 00. PLANTA BAJA · 16 PASILLO


Hoja 5 de 6 · 9 elementos: V-92, V-123, V-154, P-31, P-63, P-94, MC-1045585, MC-1046251, MC-1046631

MC-1045585 · alzado interior 1:20

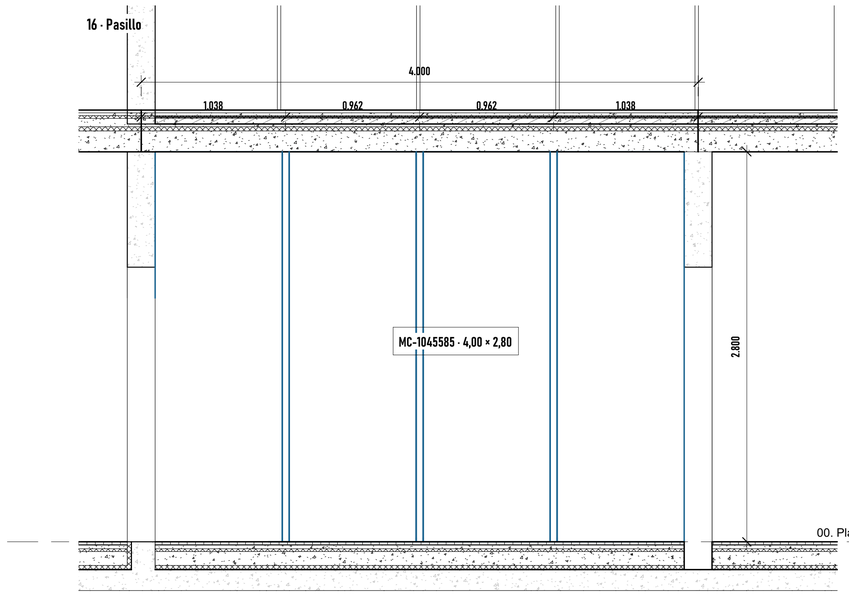

Muro cortina · Vent. Corrediza PB · 4 paneles / 13 montantes
Largo 4.000 · Alto 2.800 · Arranque +0.000 · Superior +2.800 m
Muro 0.025 m

MC-1046251 · alzado interior 1:20

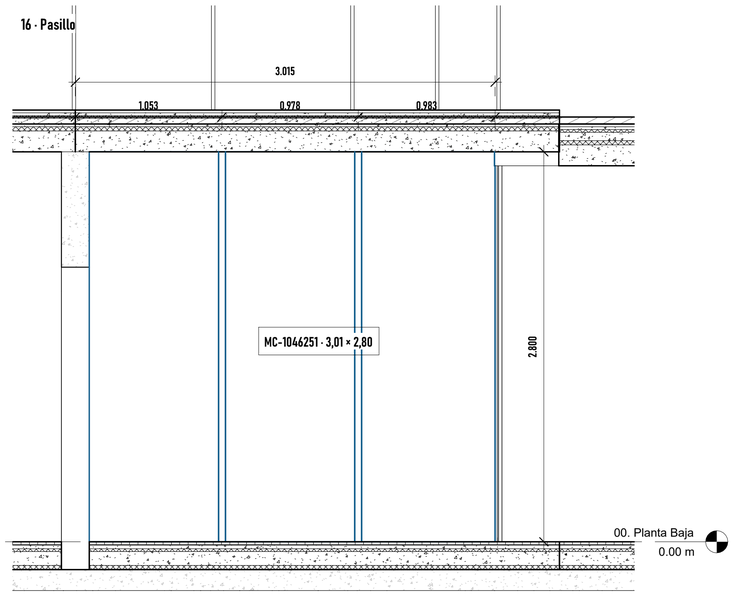

Muro cortina · Vent. Corrediza PB · 3 paneles / 11 montantes
Largo 3.015 · Alto 2.800 · Arranque +0.000 · Superior +2.800 m
Muro 0.025 m

Cotas en metros (0.001 m) sobre geometría nativa. Cotas de muros cortina y cápsula del ascensor: referidas a ejes de grilla, extremos y centros de arcos (no asociativas, salvo radios). Alzados vistos desde el interior del local. Elementos compartidos entre locales: un solo cómputo por código.

https://ezeader.myportfolio.com/ezequiel-ader

Consultant
Address
Address
Phone
Fax
e-mail

Consultant
Address
Address
Phone
Fax
e-mail

Consultant
Address
Address
Phone
Fax
e-mail

Consultant
Address
Address
Phone
Fax
e-mail

No.	Description	Date

Angel Luis Brusca

CASA ANGEL

ABR-R4-PB-16-5

Project number	0001
Date	18 de Agosto, 2025
Drawn by	Author
Checked by	Checker

Pasillo · ABR 5/6


Scale 1 : 20

10/23/2026 4:57:15 PM

CASA ÁNGEL · ABERTURAS · 00. PLANTA BAJA · 16 PASILLO

Hoja 6 de 6 · 9 elementos: V-92, V-123, V-154, P-31, P-63, P-94, MC-1045585, MC-1046251, MC-1046631

MC-1046631 · alzado interior 1:15

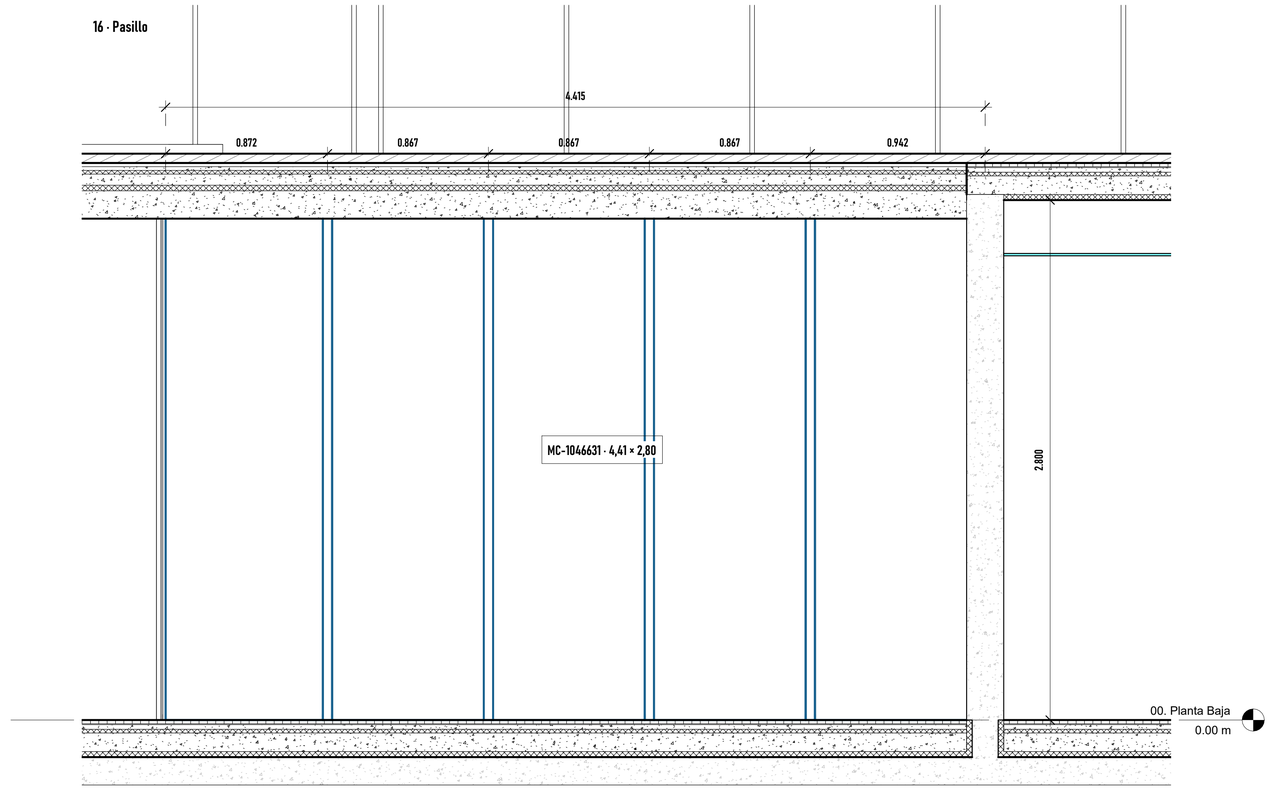

Muro cortina · Vent. Corrediza PB · 5 paneles / 16 montantes
Largo 4.415 · Alto 2.800 · Arranque +0.000 · Superior +2.800 m
Muro 0.025 m

Cotas en metros (0.001 m) sobre geometría nativa. Cotas de muros cortina y cápsula del ascensor: referidas a ejes de grilla, extremos y centros de arcos (no asociativas, salvo radios). Alzados vistos desde el interior del local. Elementos compartidos entre locales: un solo cómputo por código.

https://ezeader.myportfolio.com/ezequiel-ader

Consultant
Address
Address
Phone
Fax
e-mail

Consultant
Address
Address
Phone
Fax
e-mail

Consultant
Address
Address
Phone
Fax
e-mail

Consultant
Address
Address
Phone
Fax
e-mail

No.	Description	Date

Angel Luis Brusca

CASA ANGEL

ABR-R4-PB-16-6

Project number	0001
Date	18 de Agosto, 2025
Drawn by	Author
Checked by	Checker

Pasillo · ABR 6/6

Scale 1 : 15

10/23/2026 4:57:15 PM