

CASA ÁNGEL · ABERTURAS · 01. PLANTA ALTA · 03 PLAYROOM

Hoja 1 de 2 · 4 elementos: V-130, P-22, P-75, MC-373525

Planta del local · 03 · Playroom 1:30

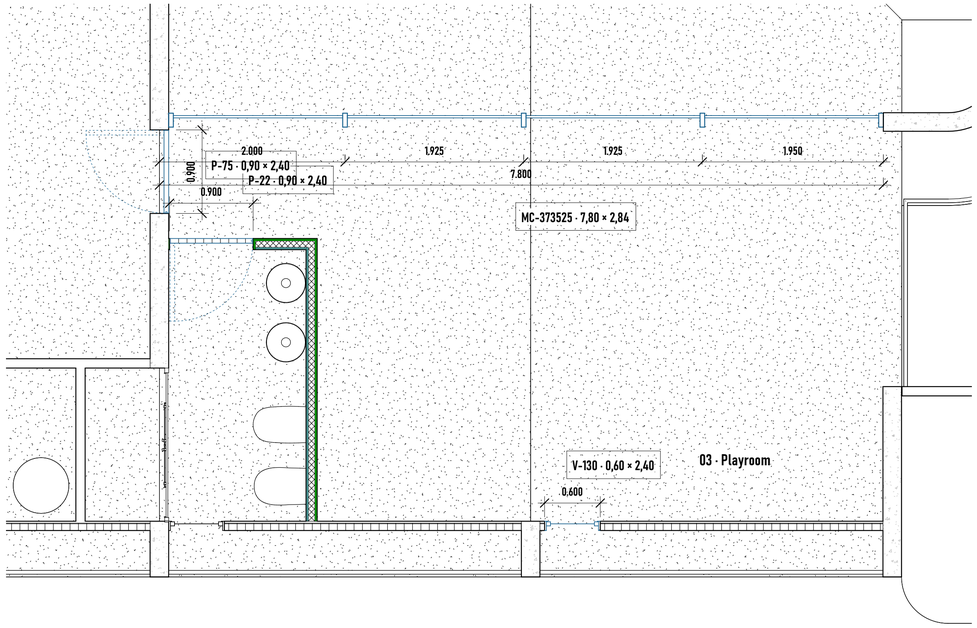

Axonométrica del local · 03 · Playroom 1:50

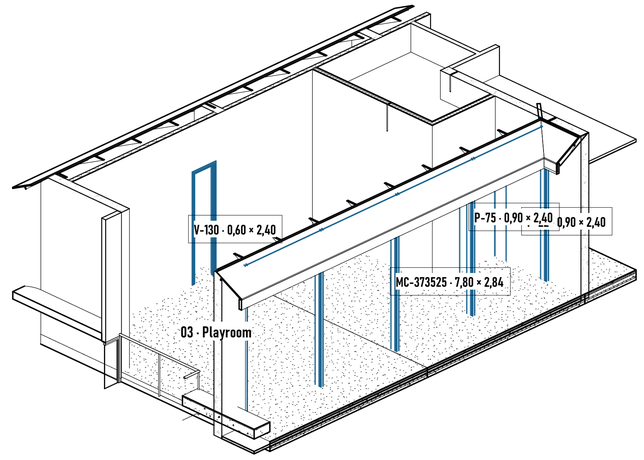

Cotas en metros (0.001 m) sobre geometría nativa. Cotas de muros cortina y cápsula del ascensor: referidas a ejes de grilla, extremos y centros de arcos (no asociativas, salvo radios). Alzados vistos desde el interior del local. Elementos compartidos entre locales: un solo cómputo por código.

https://ezeader.myportfolio.com/ezequiel-ader

Consultant
Address
Address
Phone
Fax
e-mail

Consultant
Address
Address
Phone
Fax
e-mail

Consultant
Address
Address
Phone
Fax
e-mail

Consultant
Address
Address
Phone
Fax
e-mail

No.	Description	Date

Angel Luis Brusca

CASA ANGEL

ABR-R4-PA-03

Project number	0001
Date	18 de Agosto, 2025
Drawn by	Author
Checked by	Checker

Playroom · ABR 1/2


Scale 1 : 30

10/23/2026 4:59:36 PM

CASA ÁNGEL · ABERTURAS · 01. PLANTA ALTA · 03 PLAYROOM


Hoja 2 de 2 · 4 elementos: V-130, P-22, P-75, MC-373525

V-130 · alzado interior 1:20

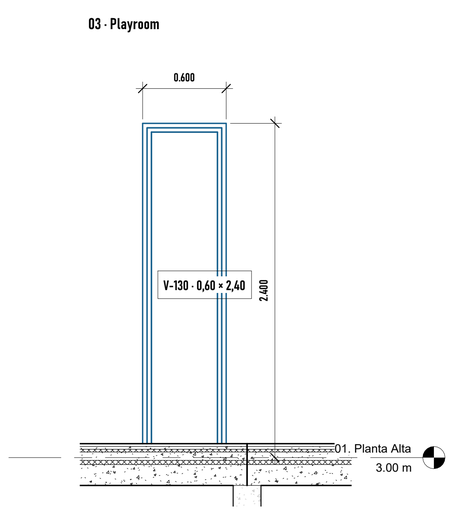


Ventana Cuartos (Muro a techo) · M_Fixed
Ancho 0.600 · Alto 2.400 · Antepecho 0.000 · Dintel 2.400 m
Tipo muro a techo: piso terminado a dintel 2.400 m (verificar con cielorraso)
Muro 0.100 m · Materiales: Glass, Sash

P-22 · alzado interior 1:20

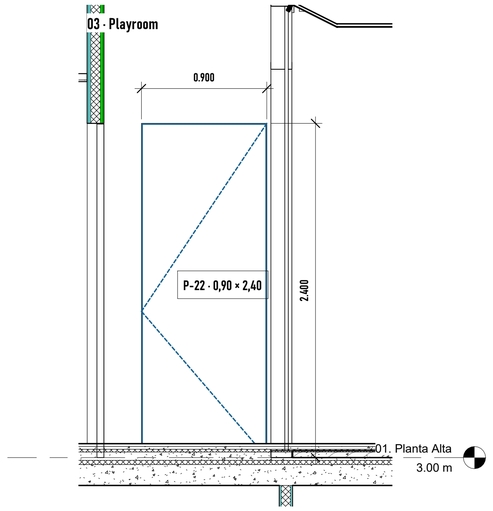


0.90 M · JALO_PUERTA ABATIBLE
Ancho 0.900 · Alto 2.400 · Antepecho 0.000 · Dintel 2.400 m
Muro 0.200 m · Materiales: Puertas
Compartida con: Sala de TV (computar una vez)

P-75 · alzado interior 1:20

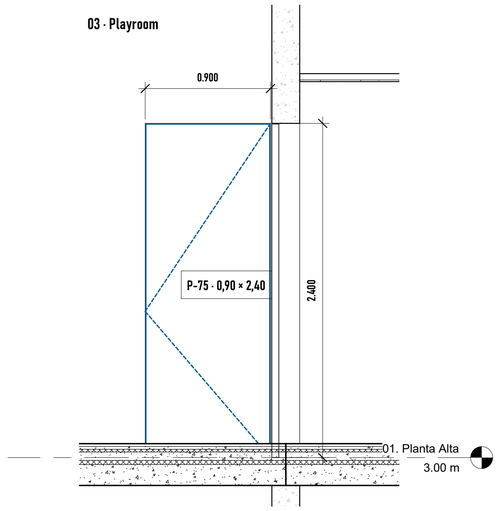

0.90 M · JALO_PUERTA ABATIBLE
Ancho 0.900 · Alto 2.400 · Antepecho 0.000 · Dintel 2.400 m
Muro 0.120 m · Materiales: Puertas
Compartida con: Baño PA (computar una vez)

MC-373525 · alzado interior 1:40

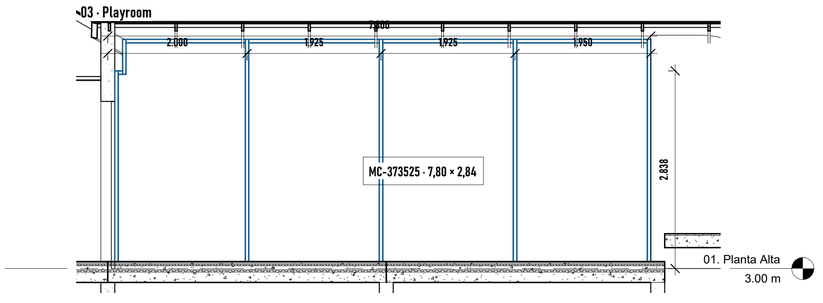

Muro cortina · Ventanales Patio · 4 paneles / 15 montantes
Largo 7.800 · Alto 2.838 · Arranque +0.000 · Superior +2.838 m
Muro 0.025 m

Cotas en metros (0.001 m) sobre geometría nativa. Cotas de muros cortina y cápsula del ascensor: referidas a ejes de grilla, extremos y centros de arcos (no asociativas, salvo radios). Alzados vistos desde el interior del local. Elementos compartidos entre locales: un solo cómputo por código.

https://ezeader.myportfolio.com/ezequiel-ader

Consultant
Address
Address
Phone
Fax
e-mail

Consultant
Address
Address
Phone
Fax
e-mail

Consultant
Address
Address
Phone
Fax
e-mail

Consultant
Address
Address
Phone
Fax
e-mail

No.	Description	Date

Angel Luis Brusca

CASA ANGEL

ABR-R4-PA-03-2

Project number	0001
Date	18 de Agosto, 2025
Drawn by	Author
Checked by	Checker
Playroom · ABR 2/2	
Scale	As indicated

10/23/2026 4:59:37 PM