CASA ÁNGEL · ABERTURAS · 00. PLANTA BAJA · SIN LOCAL ASIGNADO

Hoja 1 de 1 · 2 elementos: MC-2275029, MC-2295997

Planta del local · Sin local asignado 1:25

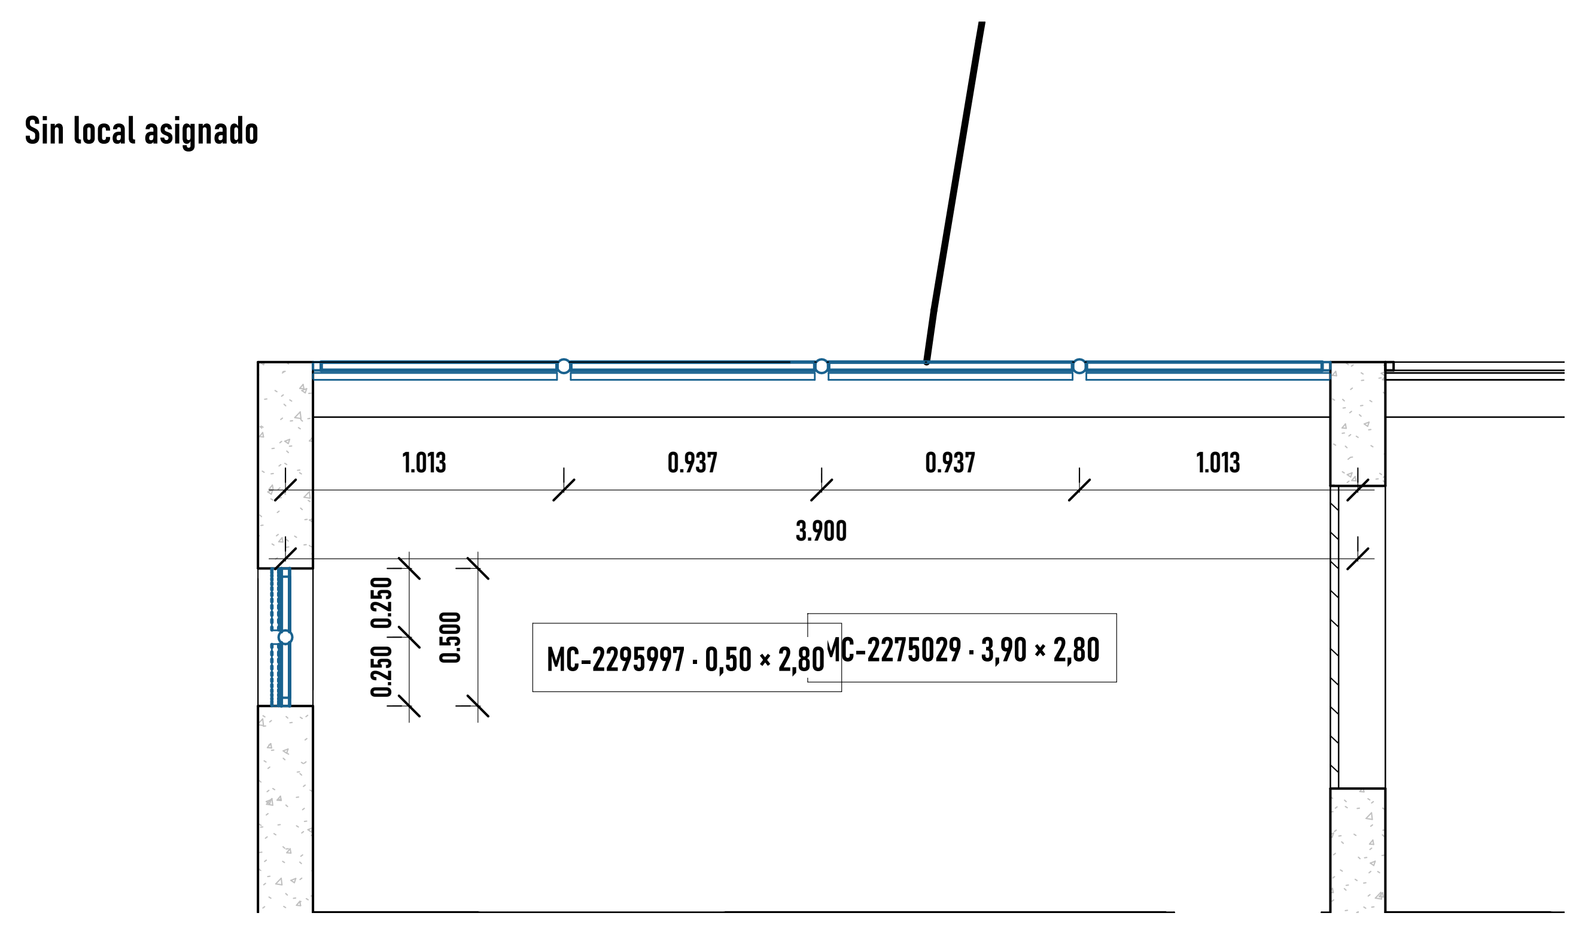

Axonométrica del local · Sin local asignado 1:30

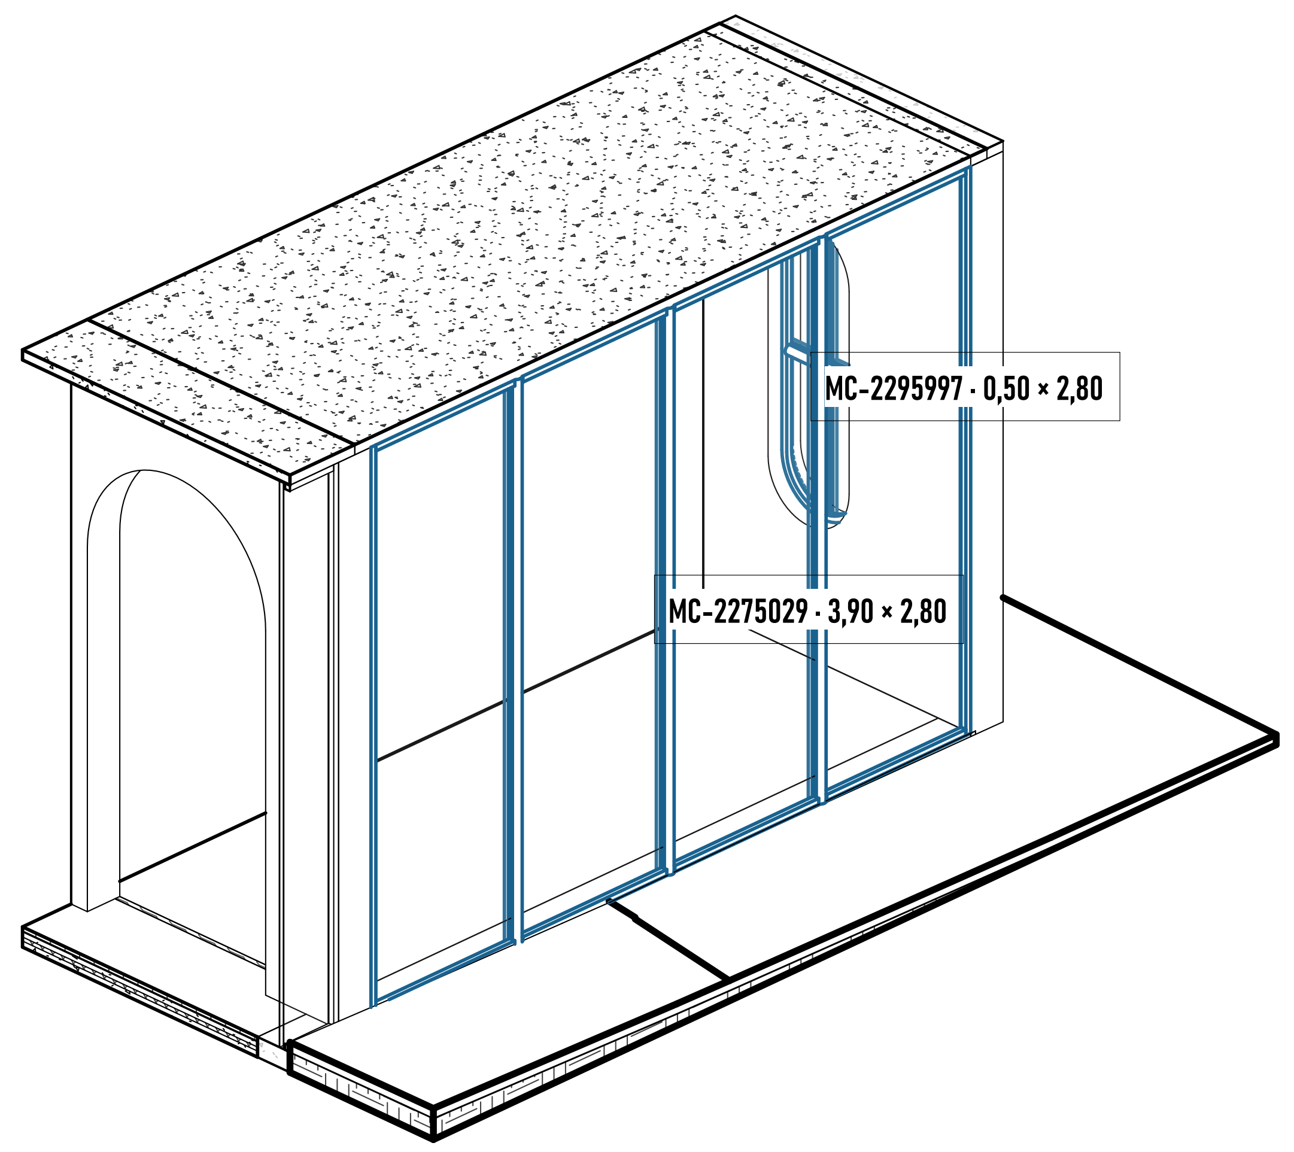

MC-2275029 · alzado interior 1:30

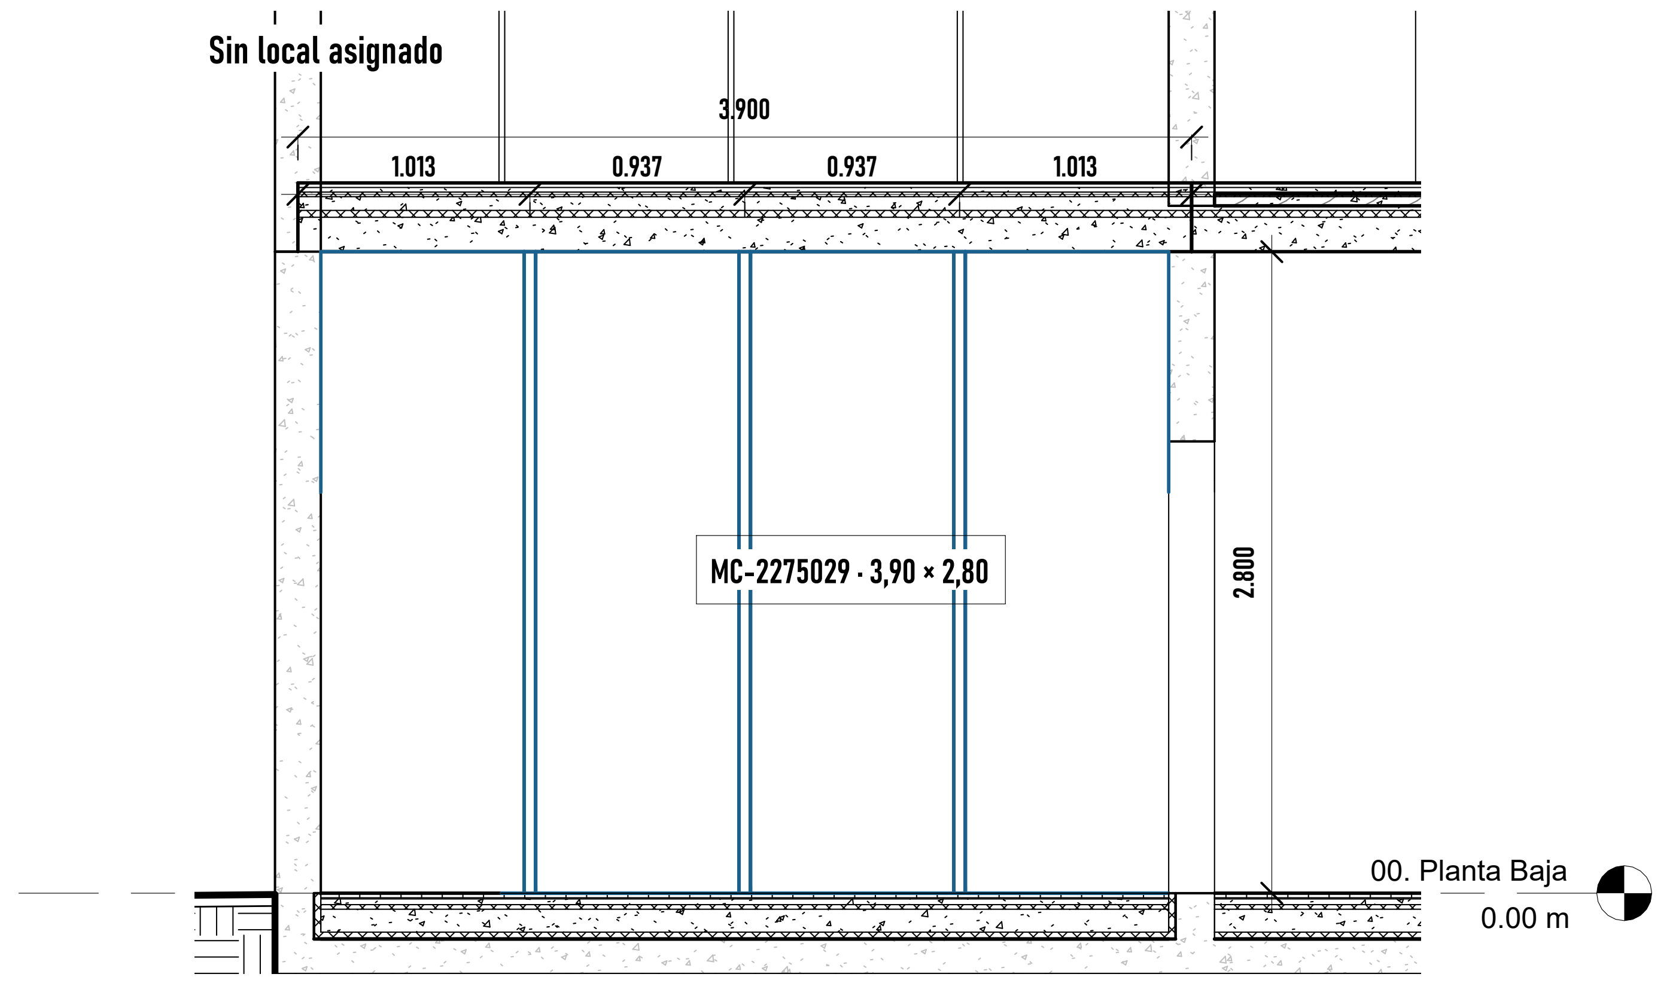

Muro cortina · Vent. Corrediza PB · 4 paneles / 13 montantes
Largo 3.900 · Alto 2.800 · Arranque +0.000 · Superior +2.800 m
Muro 0.025 m

MC-2295997 · alzado interior 1:30

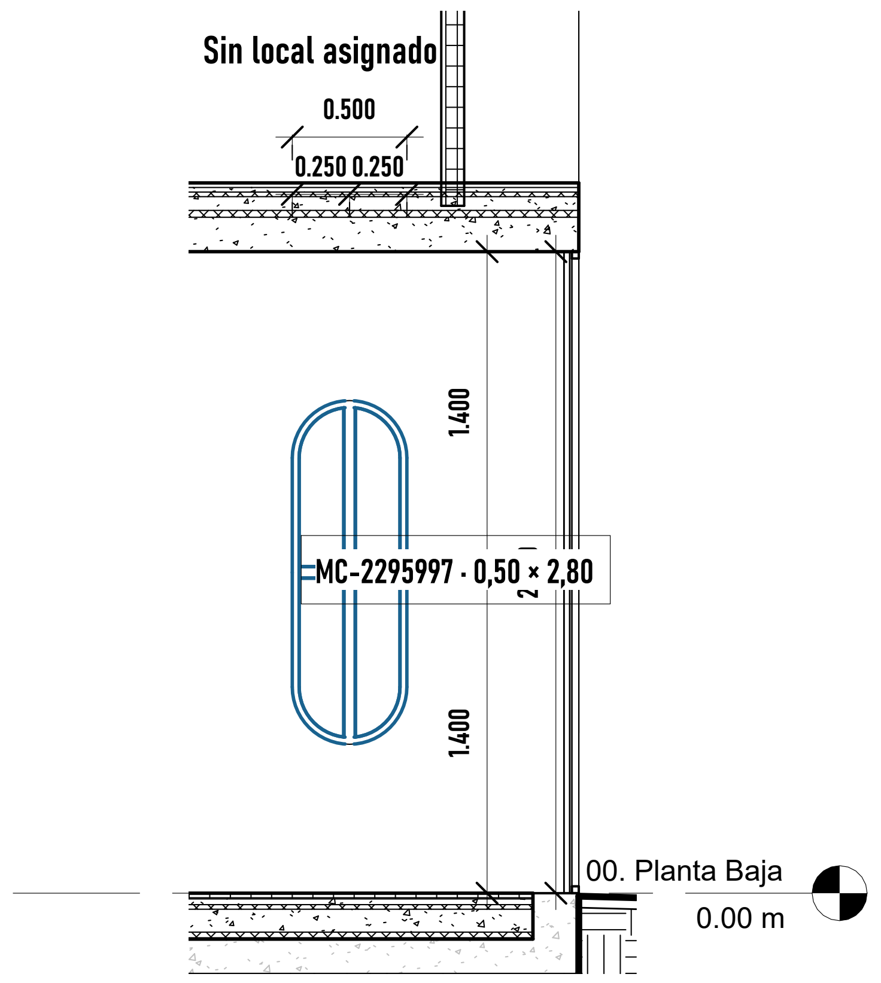

Muro cortina · Vano Pasillo · 4 paneles / 12 montantes
Largo 0.500 · Alto 2.800 · Arranque +0.000 · Superior +2.800 m
Muro 0.025 m

Cotas en metros (0.001 m) sobre geometría nativa. Cotas de muros cortina y cápsula del ascensor: referidas a ejes de grilla, extremos y centros de arcos (no asociativas, salvo radios). Alzados vistos desde el interior del local. Elementos compartidos entre locales: un solo cómputo por código.

https://ezeader.myportfolio.com/ezequiel-ader

Consultant
Address
Address
Phone
Fax
e-mail

Consultant
Address
Address
Phone
Fax
e-mail

Consultant
Address
Address
Phone
Fax
e-mail

Consultant
Address
Address
Phone
Fax
e-mail

No.	Description	Date

Angel Luis Brusca

CASA ANGEL

ABR-R4-PB-SL

Project number 0001
Date 18 de Agosto, 2025
Drawn by Author
Checked by Checker

Sin local asignado · ABR

Scale As indicated

10/23/2025 3:47 PM