
CASA ÁNGEL · CIELORRASOS · PLANTA DE CIELORRASOS · 02. PLANTA ENTREPISO

Planta de cielorrasos · 02. Planta Entrepiso 1:25

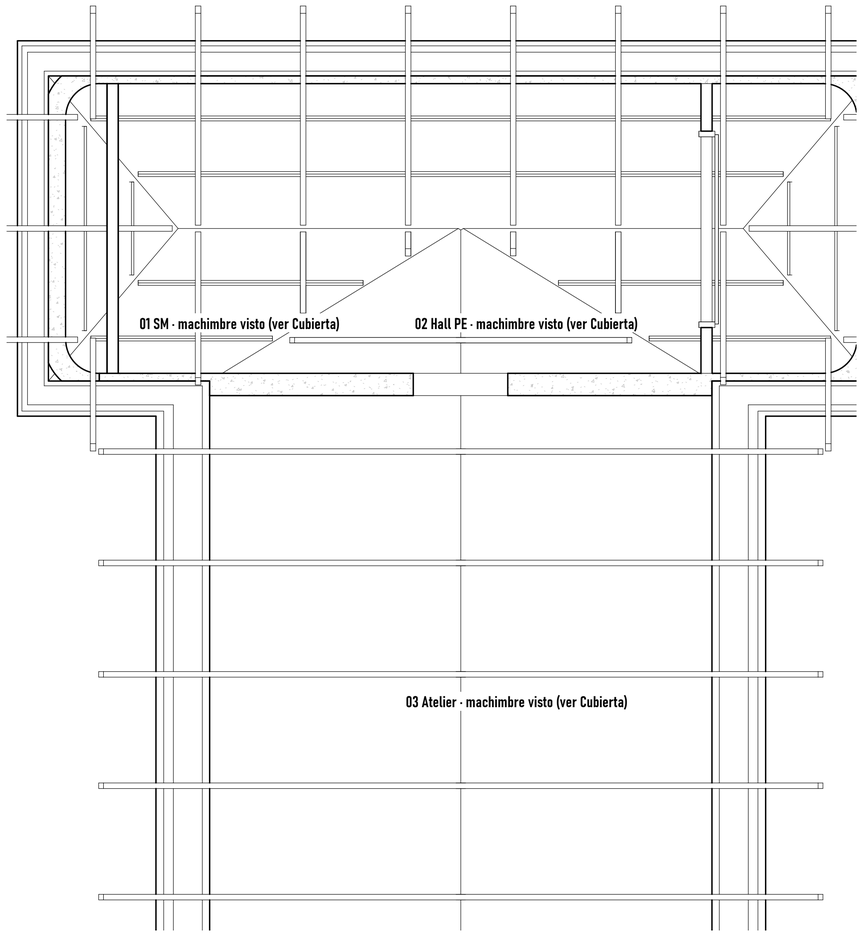

RH 0,00 m² · ST 0,00 m² · 0 cielorrasos · buña 0,00 ml

Cielorrasos R30 (archivo de documentación con el modelo principal vinculado). Suspendidos de placa de yeso 12,5 sobre perfilería galvanizada: TC-01 Knauf RH en zonas húmedas, TC-02 Knauf ST en el resto; buña Z 15; tapas 60×60 en baños y toilettes. Bajo la cubierta de madera: machimbre visto (ver Cubierta). Cotas en metros.

https://ezeader.myportfolio.com/ezequiel-ader

Consultant
Address
Address
Phone
Fax
e-mail

Consultant
Address
Address
Phone
Fax
e-mail

Consultant
Address
Address
Phone
Fax
e-mail

Consultant
Address
Address
Phone
Fax
e-mail

No.	Description	Date

Angel Luis Brusca

CASA ANGEL

CIE-PE-01

Project number	0001
Date	18 de Agosto, 2025
Drawn by	Author
Checked by	Checker

Cielorrasos · PE

Scale 1 : 25

10/24/2026 11:21:40 PM