

CASA ÁNGEL · ABERTURAS · 00. PLANTA BAJA · 08 LAVADERO

Hoja 1 de 1 · 2 elementos: P-90, P-93


Planta del local · 08 · Lavadero 1:20

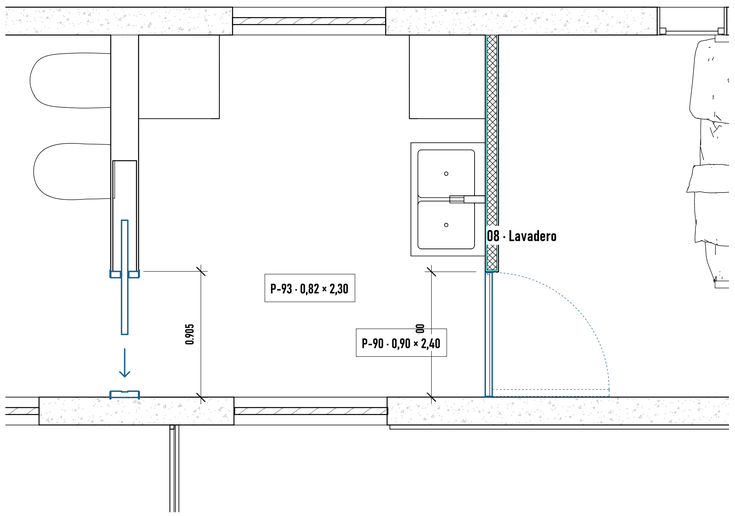

Axonométrica del local · 08 · Lavadero 1:50

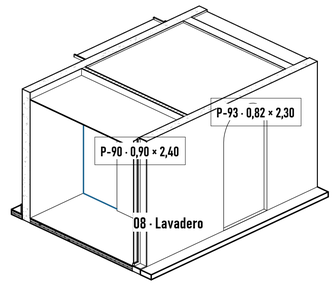


P-90 · alzado interior 1:20

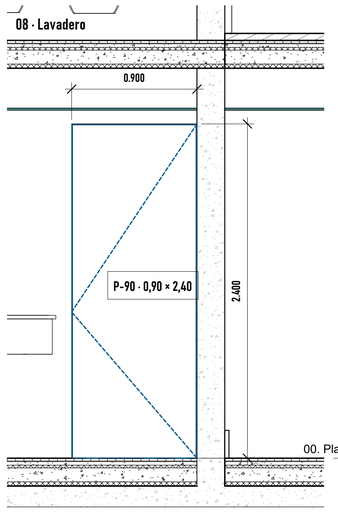

0.90 M · JALO_PUERTA ABATIBLE
Ancho 0.900 · Alto 2.400 · Antepecho 0.000 · Dintel 2.400 m
Muro 0.095 m · Materiales: Puertas
Compartida con: Hab. servicio (computar una vez)

P-93 · alzado interior 1:20

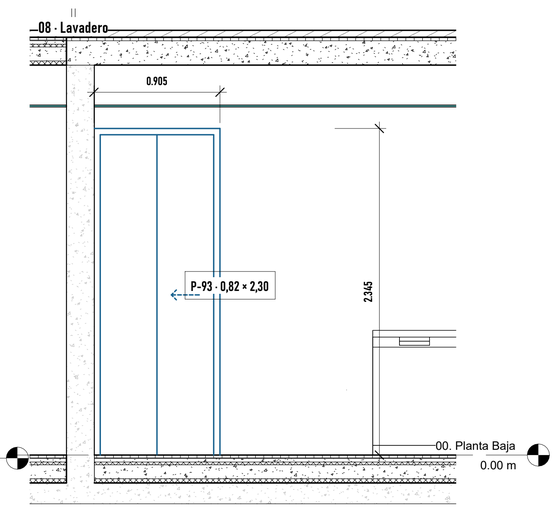

820 x 2000 mm · Puerta interior corredera
Hoja 0.820 × 2.300 · Vano 0.905 × 2.345 m
Muro 0.200 m · Materiales: Acero galvanizado, Acero inoxidable bruñido, Madera (roble), Premarco de pino
Compartida con: Toilette Servicio (computar una vez)

Cotas en metros (0.001 m) sobre geometría nativa. Cotas de muros cortina y cápsula del ascensor: referidas a ejes de grilla, extremos y centros de arcos (no asociativas, salvo radios). Alzados vistos desde el interior del local. Elementos compartidos entre locales: un solo cómputo por código.

https://ezeader.myportfolio.com/ezequiel-ader

Consultant
Address
Address
Phone
Fax
e-mail

Consultant
Address
Address
Phone
Fax
e-mail

Consultant
Address
Address
Phone
Fax
e-mail

Consultant
Address
Address
Phone
Fax
e-mail

No.	Description	Date

Angel Luis Brusca

CASA ANGEL

ABR-R4-PB-08

Project number	0001
Date	18 de Agosto, 2025
Drawn by	Author
Checked by	Checker

Lavadero · ABR

Scale 1 : 20

10/23/2026 3:47:18 PM