

# CASA ÁNGEL · ABERTURAS · 00. PLANTA BAJA · 04 BAÑO B INV.

**Hoja 1 de 2 · 3 elementos: V-57, V-131, P-59**

### Planta del local · 04 · Baño B Inv.  1:20

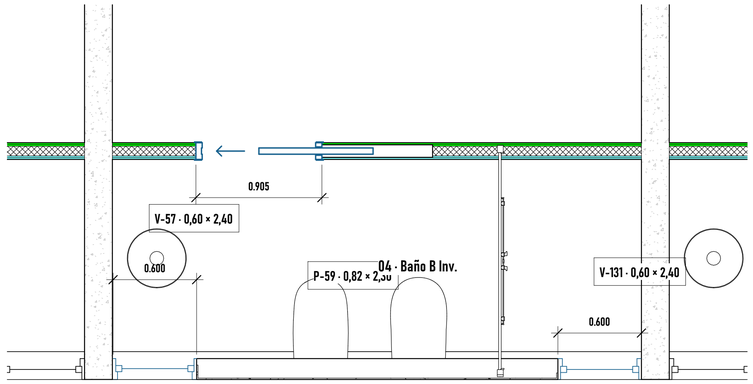


### Axonométrica del local · 04 · Baño B Inv.  1:20

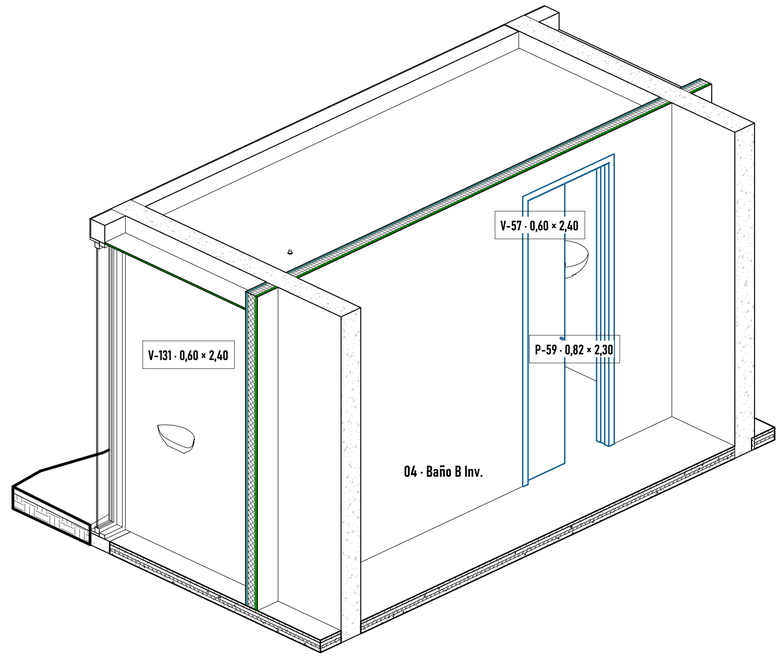


Cotas en metros (0.001 m) sobre geometría nativa. Cotas de muros cortina y cápsula del ascensor: referidas a ejes de grilla, extremos y centros de arcos (no asociativas, salvo radios). Alzados vistos desde el interior del local. Elementos compartidos entre locales: un solo cómputo por código.

https://ezeader.myportfolio.com/ezequiel-ader


Consultant
Address
Address
Phone
Fax
e-mail

Consultant
Address
Address
Phone
Fax
e-mail

Consultant
Address
Address
Phone
Fax
e-mail

Consultant
Address
Address
Phone
Fax
e-mail


| No. | Description | Date |
|---|---|---|
| | | |
| | | |
Angel Luis Brusca

CASA ANGEL

ABR-R4-PB-04

| | |
|---|---|
| Project number | 0001 |
| Date | 18 de Agosto, 2025 |
| Drawn by | Author |
| Checked by | Checker |

Baño B Inv. · ABR 1/2


Scale 1 : 20

10/23/2025 8:36:32 PM

# CASA ÁNGEL · ABERTURAS · 00. PLANTA BAJA · 04 BAÑO B INV.


Hoja 2 de 2 · 3 elementos: V-57, V-131, P-59

## V-57 · alzado interior 1:15

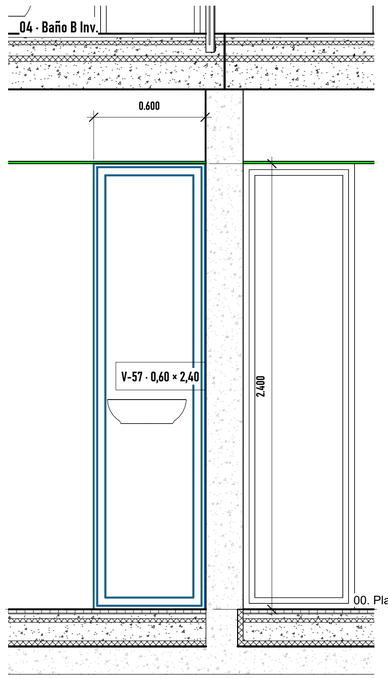



Ventana Cuartos (Muro a techo) · M_Fixed
Ancho 0.600 · Alto 2.400 · Antepecho 0.000 · Dintel 2.400 m
Tipo muro a techo: piso terminado a dintel 2.400 m (verificar con cielorraso)
Muro 0.150 m · Materiales: Glass, Sash

## V-131 · alzado interior 1:15

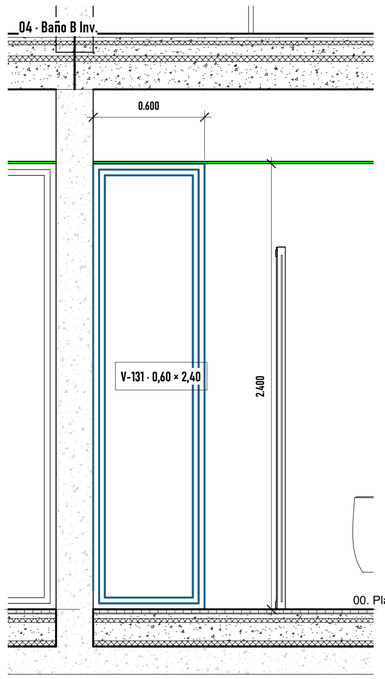


Ventana Cuartos (Muro a techo) · M_Fixed
Ancho 0.600 · Alto 2.400 · Antepecho 0.000 · Dintel 2.400 m
Tipo muro a techo: piso terminado a dintel 2.400 m (verificar con cielorraso)
Muro 0.150 m · Materiales: Glass, Sash

## P-59 · alzado interior 1:15

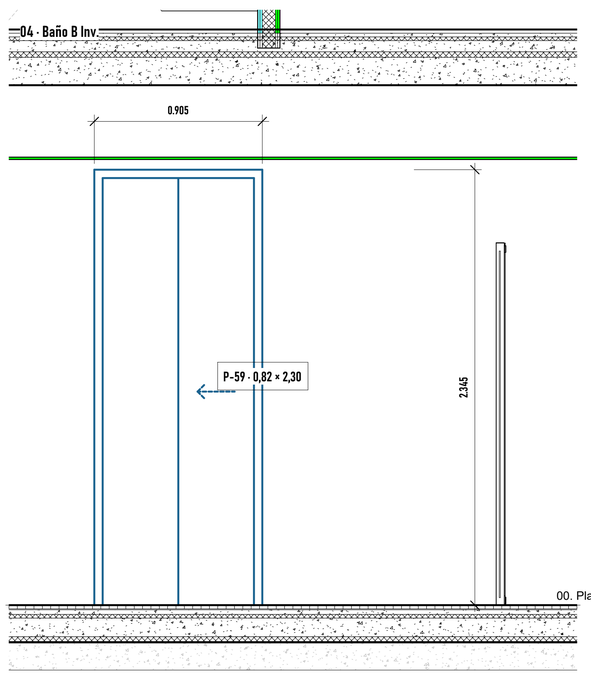


820 x 2000 mm · Puerta interior corredera
Hoja 0.820 × 2.300 · Vano 0.905 × 2.345 m
Muro 0.120 m · Materiales: Acero galvanizado, Acero inoxidable bruñido, Madera (roble), Premarco de pino
Compartida con: Cuarto B Inv. (computar una vez)

Cotas en metros (0.001 m) sobre geometría nativa. Cotas de muros cortina y cápsula del ascensor: referidas a ejes de grilla, extremos y centros de arcos (no asociativas, salvo radios). Alzados vistos desde el interior del local. Elementos compartidos entre locales: un solo cómputo por código.

https://ezeader.myportfolio.com/ezequiel-ader

Consultant
Address
Address
Phone
Fax
e-mail

Consultant
Address
Address
Phone
Fax
e-mail

Consultant
Address
Address
Phone
Fax
e-mail

Consultant
Address
Address
Phone
Fax
e-mail

| No. | Description | Date |
|---|---|---|
| | | |

Angel Luis Brusca

CASA ANGEL

ABR-R4-PB-04-2

| | |
|---|---|
| Project number | 0001 |
| Date | 18 de Agosto, 2025 |
| Drawn by | Author |
| Checked by | Checker |

Baño B Inv. · ABR 2/2

Scale 1 : 15

10/23/2025 6:36:34 PM