

# CASA ÁNGEL · ABERTURAS · 00. PLANTA BAJA · 09 HAB. SERVICIO

**Hoja 1 de 2 · 2 elementos: V-147, P-90**

**Planta del local · 09 · Hab. servicio  1:15**

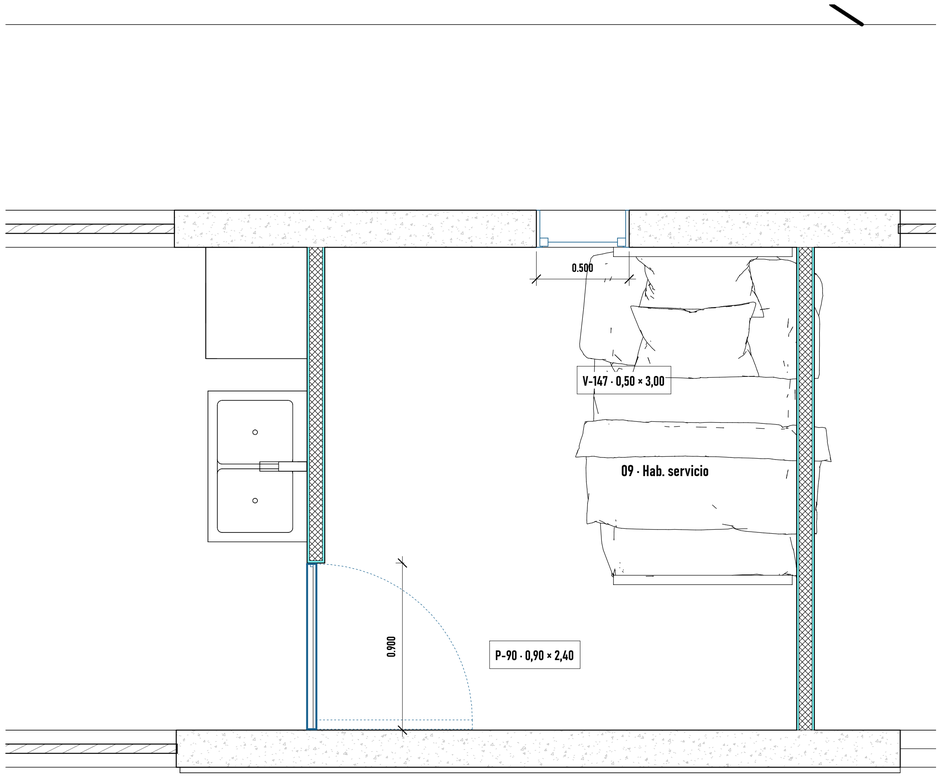


**Axonométrica del local · 09 · Hab. servicio  1:25**

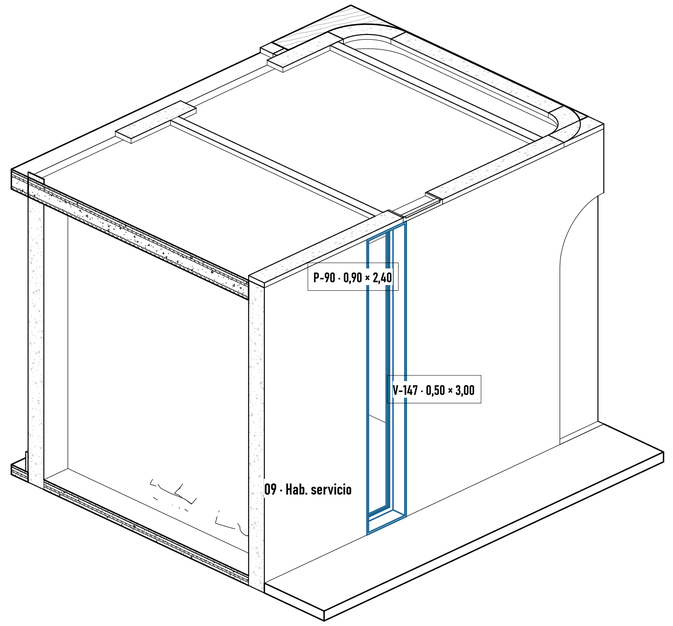


Cotas en metros (0.001 m) sobre geometría nativa. Cotas de muros cortina y cápsula del ascensor: referidas a ejes de grilla, extremos y centros de arcos (no asociativas, salvo radios). Alzados vistos desde el interior del local. Elementos compartidos entre locales: un solo cómputo por código.


https://ezeader.myportfolio.com/ezequiel-ader

Consultant
Address
Address
Phone
Fax
e-mail

Consultant
Address
Address
Phone
Fax
e-mail

Consultant
Address
Address
Phone
Fax
e-mail

Consultant
Address
Address
Phone
Fax
e-mail


| No. | Description | Date |
|---|---|---|
| | | |

Angel Luis Brusca

CASA ANGEL

ABR-R4-PB-09


| | |
|---|---|
| Project number | 0001 |
| Date | 18 de Agosto, 2025 |
| Drawn by | Author |
| Checked by | Checker |
| Hab. servicio · ABR 1/2 | |
| Scale | 1 : 15 |

10/23/2025 9:39:40 PM

# CASA ÁNGEL · ABERTURAS · 00. PLANTA BAJA · 09 HAB. SERVICIO


Hoja 2 de 2 · 2 elementos: V-147, P-90

## V-147 · alzado interior 1:15

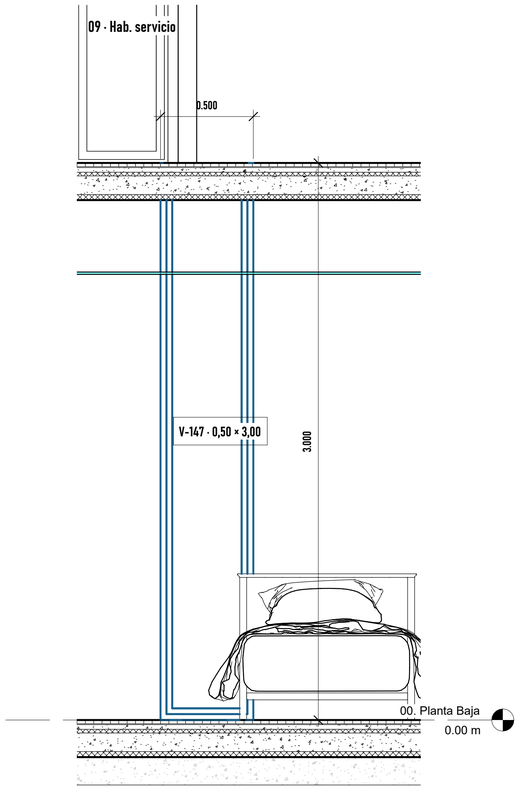


Ventanas Servicios · M_Fixed
Ancho 0.500 · Alto 3.000 · Antepecho 0.000 · Dintel 3.000 m
Muro 0.200 m · Materiales: Glass, Sash

## P-90 · alzado interior 1:15

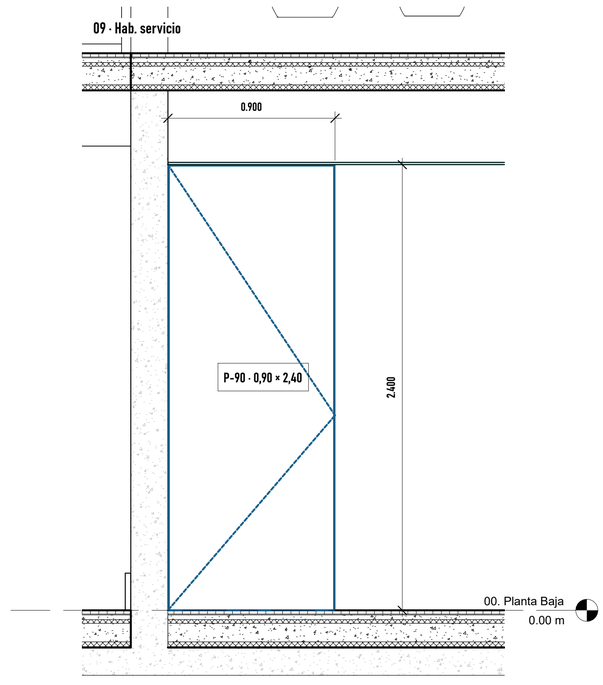


0.90 M - JALO_PUERTA ABATIBLE
Ancho 0.900 · Alto 2.400 · Antepecho 0.000 · Dintel 2.400 m
Muro 0.095 m · Materiales: Puertas
Compartida con: Lavadero (computar una vez)

Cotas en metros (0.001 m) sobre geometría nativa. Cotas de muros cortina y cápsula del ascensor: referidas a ejes de grilla, extremos y centros de arcos (no asociativas, salvo radios). Alzados vistos desde el interior del local. Elementos compartidos entre locales: un solo cómputo por código.

https://ezeader.myportfolio.com/ezequiel-ader


Consultant
Address
Address
Phone
Fax
e-mail

Consultant
Address
Address
Phone
Fax
e-mail

Consultant
Address
Address
Phone
Fax
e-mail

Consultant
Address
Address
Phone
Fax
e-mail


| No. | Description | Date |
|---|---|---|
| | | |

Angel Luis Brusca

CASA ANGEL

ABR-R4-PB-09-2

| | |
|---|---|
| Project number | 0001 |
| Date | 18 de Agosto, 2025 |
| Drawn by | Author |
| Checked by | Checker |

Hab. servicio · ABR 2/2

Scale 1 : 15

10/23/2025 9:09:41 PM