

CASA ÁNGEL · ABERTURAS · 01. PLANTA ALTA · 04 BAÑO PA

Hoja 1 de 1 · 2 elementos: V-101, P-75


Planta del local · 04 · Baño PA 1:15

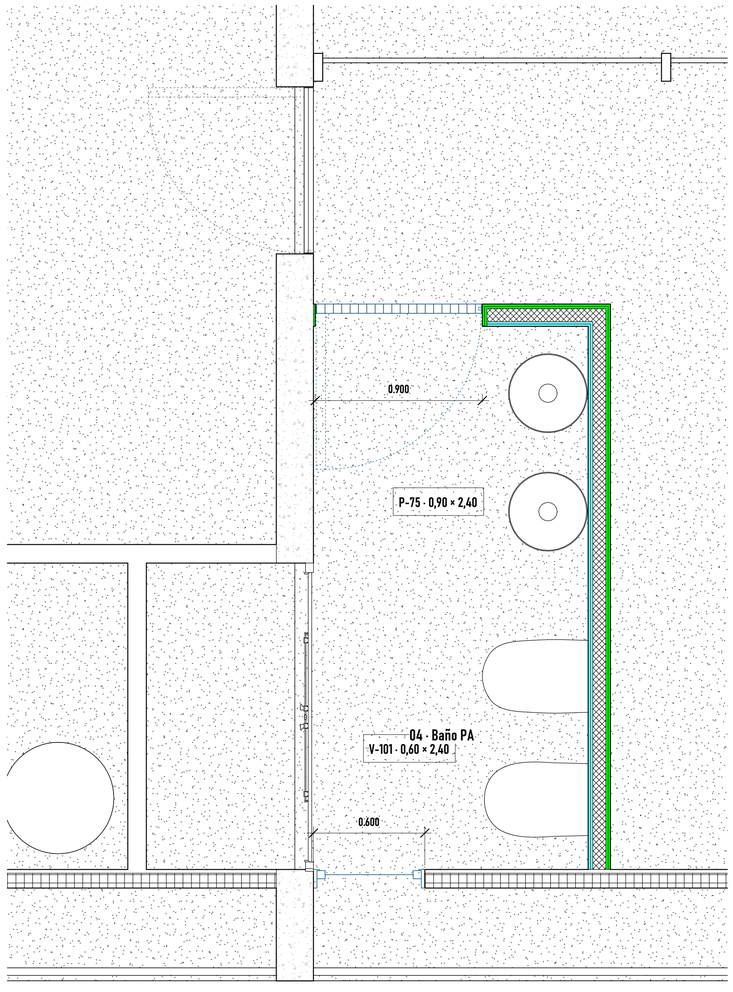

Axonométrica del local · 04 · Baño PA 1:50

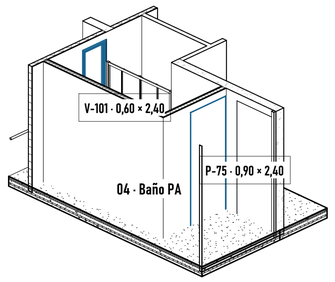


V-101 · alzado interior 1:20

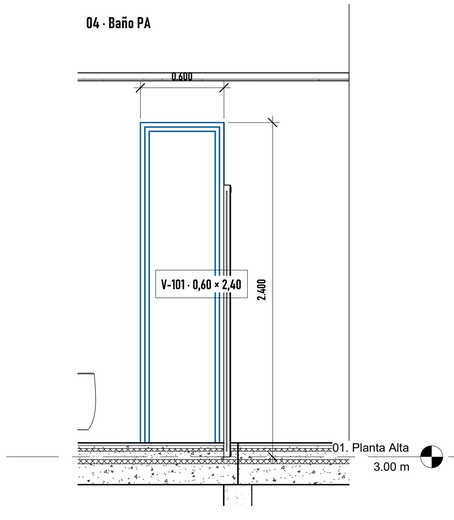

Ventana Cuartos (Muro a techo) · M_Fixed
Ancho 0.600 · Alto 2.400 · Antepecho 0.000 · Dintel 2.400 m
Tipo muro a techo: piso terminado a dintel 2.400 m (verificar con cielorraso)
Muro 0.100 m · Materiales: Glass, Sash

P-75 · alzado interior 1:20

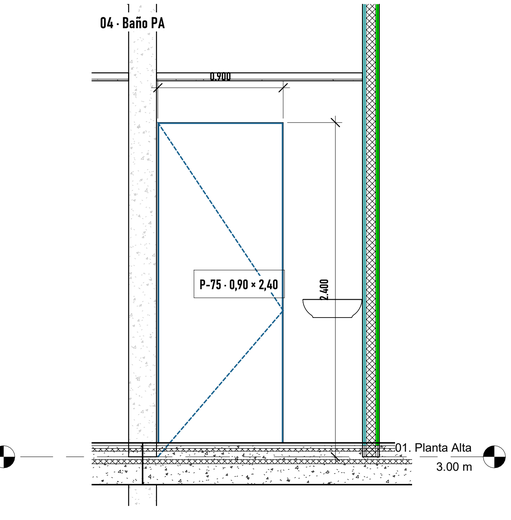

0.90 M · JALO_PUERTA ABATIBLE
Ancho 0.900 · Alto 2.400 · Antepecho 0.000 · Dintel 2.400 m
Muro 0.120 m · Materiales: Puertas
Compartida con: Playroom (computar una vez)

Cotas en metros (0.001 m) sobre geometría nativa. Cotas de muros cortina y cápsula del ascensor: referidas a ejes de grilla, extremos y centros de arcos (no asociativas, salvo radios). Alzados vistos desde el interior del local. Elementos compartidos entre locales: un solo cómputo por código.

https://ezeader.myportfolio.com/ezequiel-ader

Consultant
Address
Address
Phone
Fax
e-mail

Consultant
Address
Address
Phone
Fax
e-mail

Consultant
Address
Address
Phone
Fax
e-mail

Consultant
Address
Address
Phone
Fax
e-mail

No.	Description	Date

Angel Luis Brusca

CASA ANGEL

ABR-R4-PA-04

Project number	0001
Date	18 de Agosto, 2025
Drawn by	Author
Checked by	Checker

Baño PA · ABR

Scale As indicated

10/23/2026 3:44:01 PM