CASA ÁNGEL · ABERTURAS · 00. PLANTA BAJA · SIN LOCAL ASIGNADO

Hoja 1 de 1 · 2 elementos: MC-2275029, MC-2295997

Planta del local · Sin local asignado 1:25

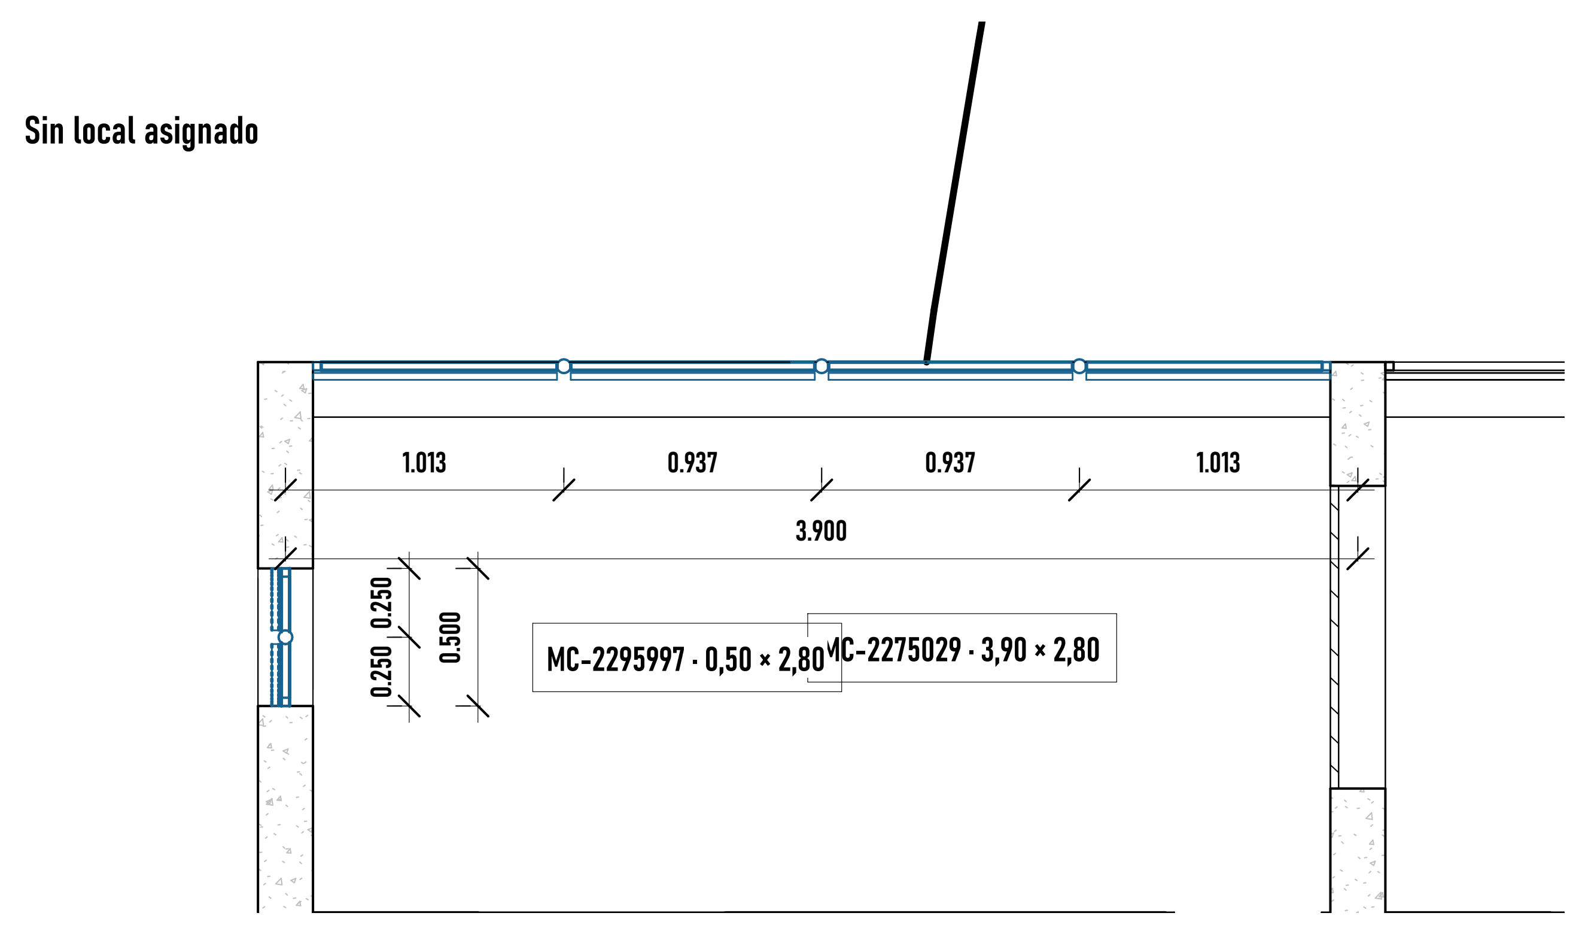
Sin local asignado
1.013
0.937
0.937
1.013
3.900
0.250
0.250
0.500
MC-2295997 · 0,50 × 2,80
MC-2275029 · 3,90 × 2,80

Axonométrica del local · Sin local asignado 1:30

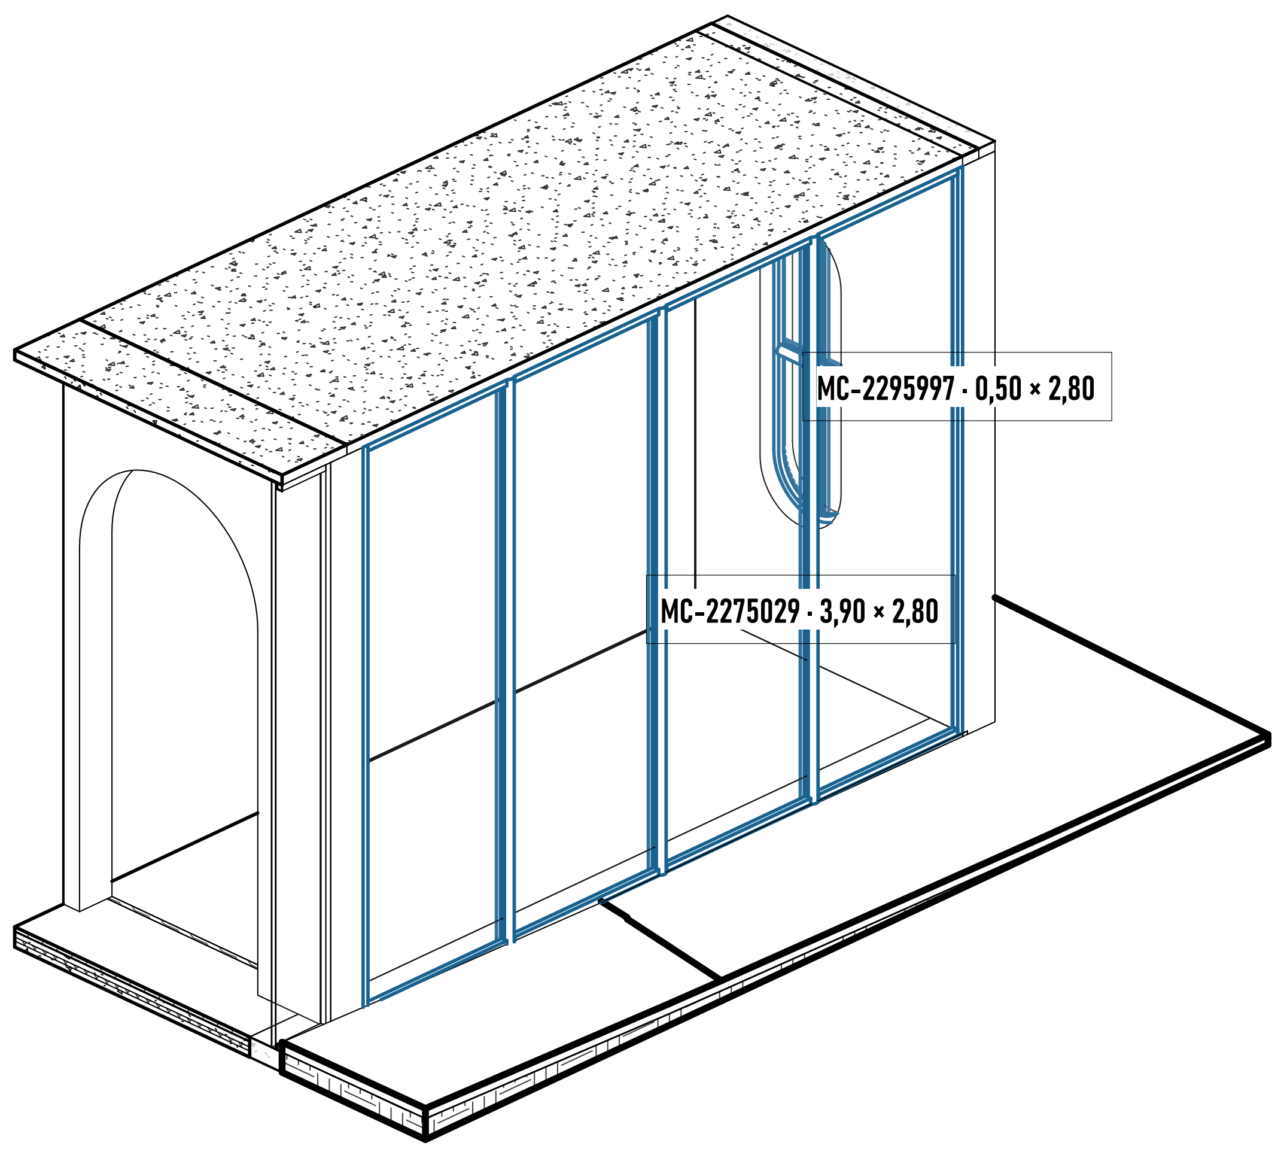
MC-2295997 · 0,50 × 2,80
MC-2275029 · 3,90 × 2,80

MC-2275029 · alzado interior 1:30

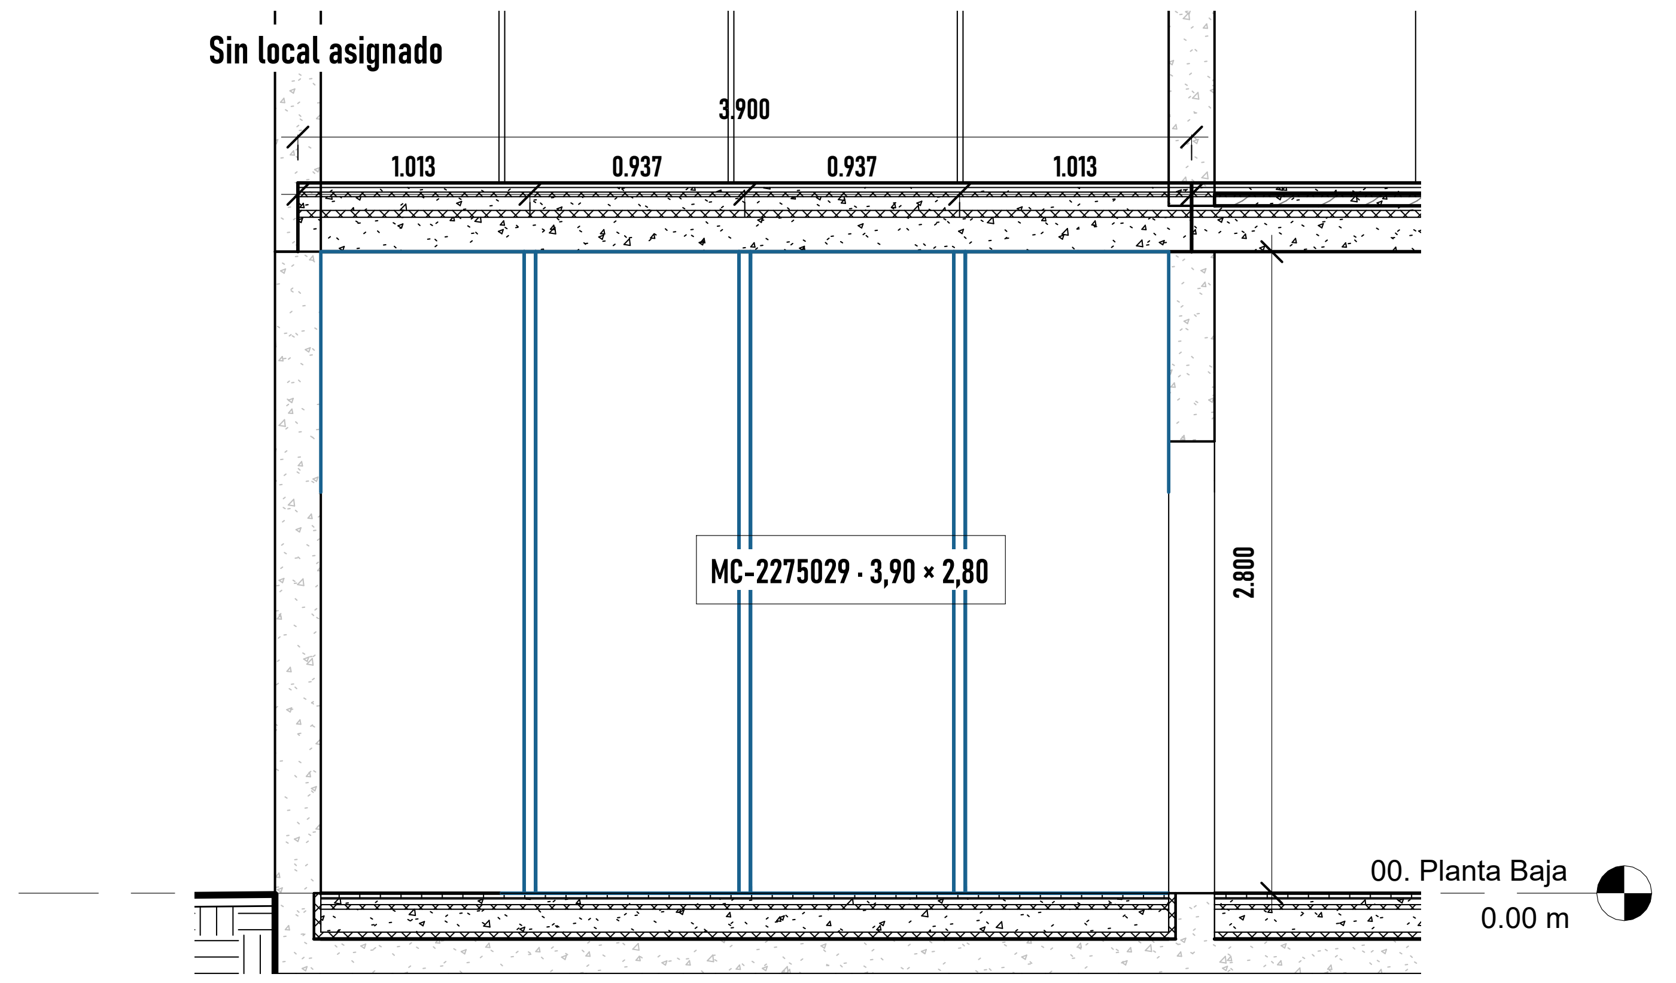
Sin local asignado
3.900
1.013
0.937
0.937
1.013
MC-2275029 · 3,90 × 2,80
2.800
00. Planta Baja
0.00 m

Muro cortina · Vent. Corrediza PB · 4 paneles / 13 montantes
Largo 3.900 · Alto 2.800 · Arranque +0.000 · Superior +2.800 m
Muro 0.025 m

MC-2295997 · alzado interior 1:30

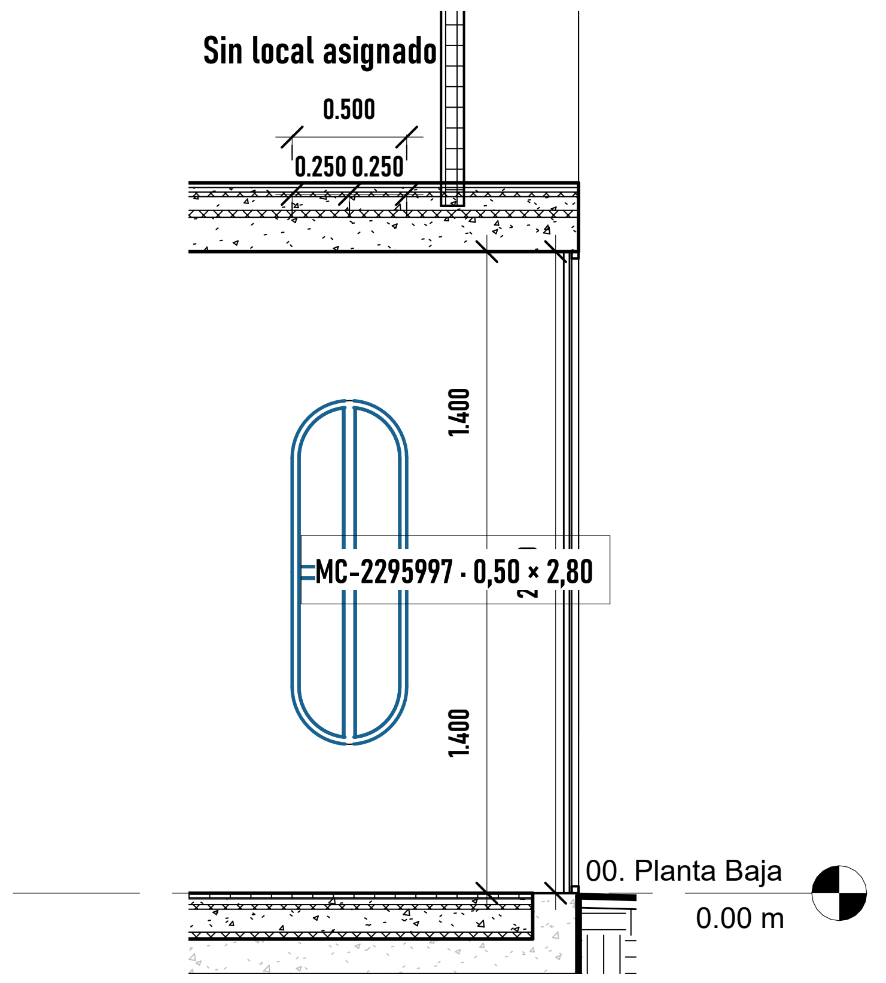
Sin local asignado
0.500
0.250 0.250
1.400
MC-2295997 · 0,50 × 2,80
1.400
00. Planta Baja
0.00 m

Muro cortina · Vano Pasillo · 4 paneles / 12 montantes
Largo 0.500 · Alto 2.800 · Arranque +0.000 · Superior +2.800 m
Muro 0.025 m

Cotas en metros (0.001 m) sobre geometría nativa. Cotas de muros cortina y cápsula del ascensor: referidas a ejes de grilla, extremos y centros de arcos (no asociativas, salvo radios). Alzados vistos desde el interior del local. Elementos compartidos entre locales: un solo cómputo por código.

https://ezeader.myportfolio.com/ezequiel-ader

Consultant
Address
Address
Phone
Fax
e-mail

Consultant
Address
Address
Phone
Fax
e-mail

Consultant
Address
Address
Phone
Fax
e-mail

Consultant
Address
Address
Phone
Fax
e-mail

No.	Description	Date

Angel Luis Brusca

CASA ANGEL

ABR-R4-PB-SL

Project number	0001
Date	18 de Agosto, 2025
Drawn by	Author
Checked by	Checker

Sin local asignado · ABR

Scale	As indicated

10/23/2026 3:47:44 PM