
CASA ÁNGEL · CIELORRASOS · PROPUESTA DE CIELORRASOS · 00. PLANTA BAJA

Cielorrasos propuestos · 00. Planta Baja 1:60

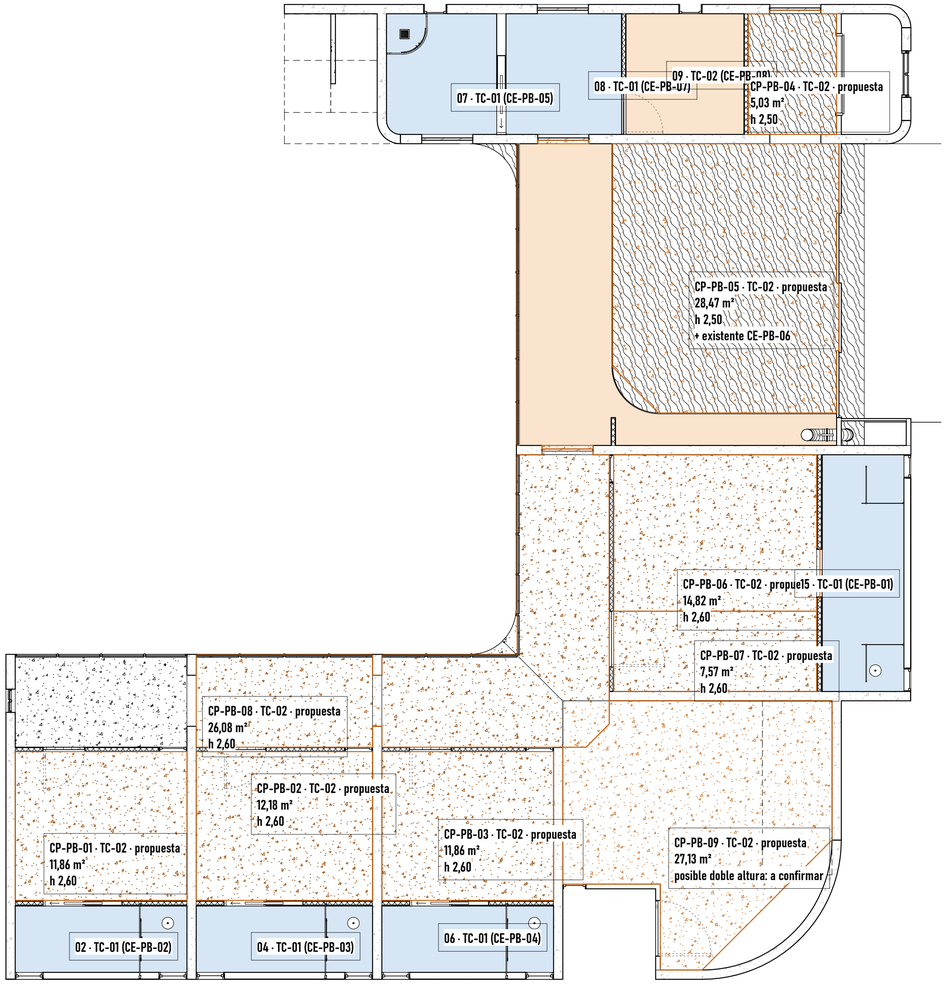

PROPUESTA A CONFIRMAR · RH 37,79 m² · ST 168,14 m² · propuesto 144,99 m² (rayado) · buña 236,52 ml

PROPUESTA A CONFIRMAR · Cielorrasos suspendidos de placa de yeso 12,5 mm sobre perfilería galvanizada: TC-01 placa RH en zonas húmedas (baños, toilettes, cocina, lavadero), TC-02 placa ST en el resto. Buña perimetral Z 15 mm; tapa de inspección 60×60 en baños, toilettes y sala de máquinas. Rayado: cielorraso propuesto (CP); sin rayado: existente en el modelo. El modelo no se modificó.

https://ezeader.myportfolio.com/ezequiel-ader

Consultant
Address
Address
Phone
Fax
e-mail

Consultant
Address
Address
Phone
Fax
e-mail

Consultant
Address
Address
Phone
Fax
e-mail

Consultant
Address
Address
Phone
Fax
e-mail

No.	Description	Date

Angel Luis Brusca

CASA ANGEL

CIE-P-PB

Project number	0001
Date	18 de Agosto, 2025
Drawn by	Author
Checked by	Checker

Cielorrasos · propuesta PB

Scale 1 : 60

10/24/2025 10:35:39 AM