

CASA ÁNGEL · ESTRUCTURA · FICHA LO-PB-01 · PAQUETE DE PISO SOBRE PLATEA

LO-PB-01 no es losa de hormigón: aislación hidrófuga + carpeta sobre la platea PL-02 · ver EST-FU-01

LO-PB-01 · planta 1:75

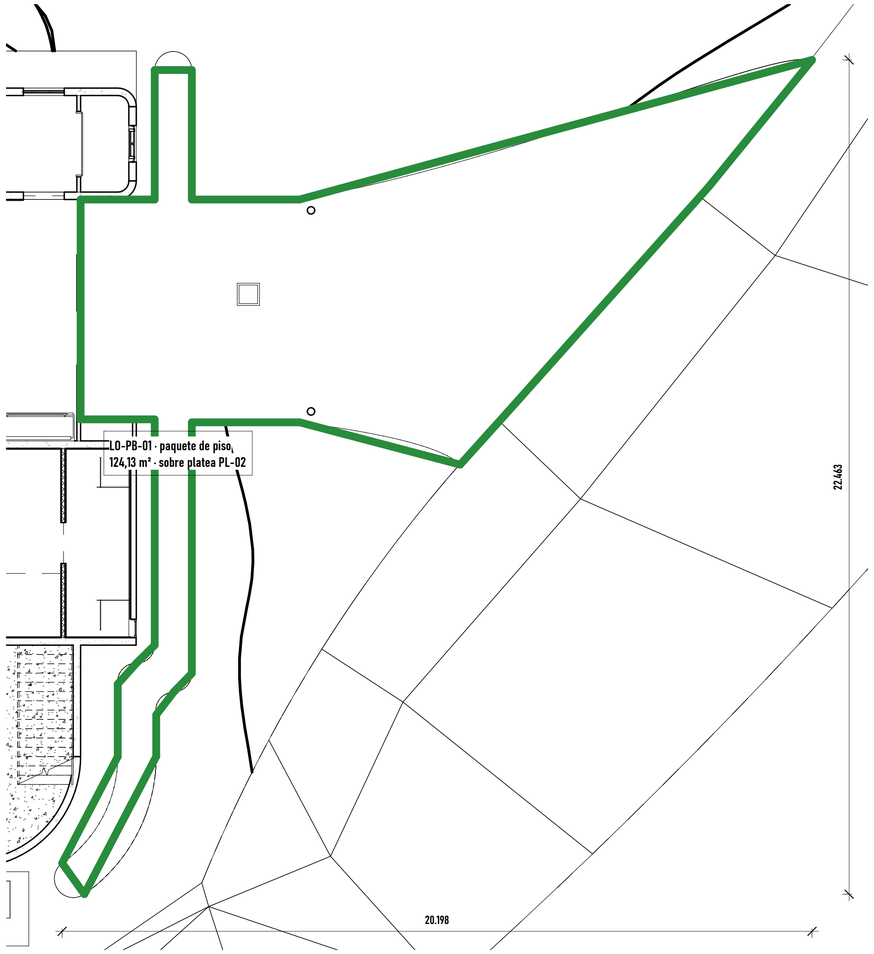

Corte tipo · platea y paquete de piso 1:10

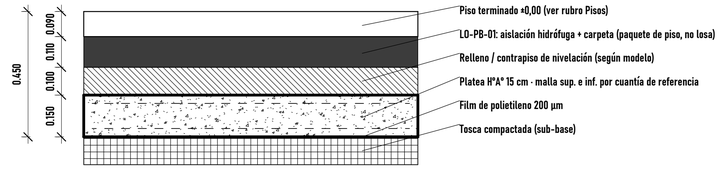

Niveles del modelo: platea −0,45 / −0,20 (tipo «Platea PB 15CM»: tosca + film + H°) · LO-PB-01 −0,61 / −0,09 · NPT ±0,00

LO-PB-01

Verde: LO-PB-01 (paquete de piso)
Naranja: platea PL-02 debajo (misma huella)
Área 124,13 m² · perímetro 86,08 m
En el modelo sigue como «Insitu Concrete 225mm» (−0,61 / −0,09): se superpone con la platea; se documenta como paquete, sin H° propio.
Cambiar el tipo en el modelo: con OK del usuario.

Estructura R31 (archivo de documentación con el modelo principal vinculado). Toda la PB apoya sobre platea H°A° 15 cm (PL-01 + ampliación PL-02 R31) sobre film y tosca compactada; LO-PB-01 se documenta como paquete de piso. Armadura por cuantía de referencia hasta el cálculo. Cotas en metros.

https://ezeader.myportfolio.com/ezequiel-ader

Consultant
Address
Address
Phone
Fax
e-mail

Consultant
Address
Address
Phone
Fax
e-mail

Consultant
Address
Address
Phone
Fax
e-mail

Consultant
Address
Address
Phone
Fax
e-mail

No.	Description	Date

Angel Luis Brusca

CASA ANGEL

EST-F-LO-PB-01

Project number	0001
Date	18 de Agosto, 2025
Drawn by	Author
Checked by	Checker

Estructura · LO-PB-01

Scale: As indicated

10/25/2026 12:07:36 AM