

CASA ÁNGEL · ESTRUCTURA · PLATEA DE FUNDACIÓN PB

Toda la PB sobre platea: PL-01 + ampliación PL-02 (R31) · H°A° 15 cm · niveles y corte tipo

Platea PB · contorno 1:150

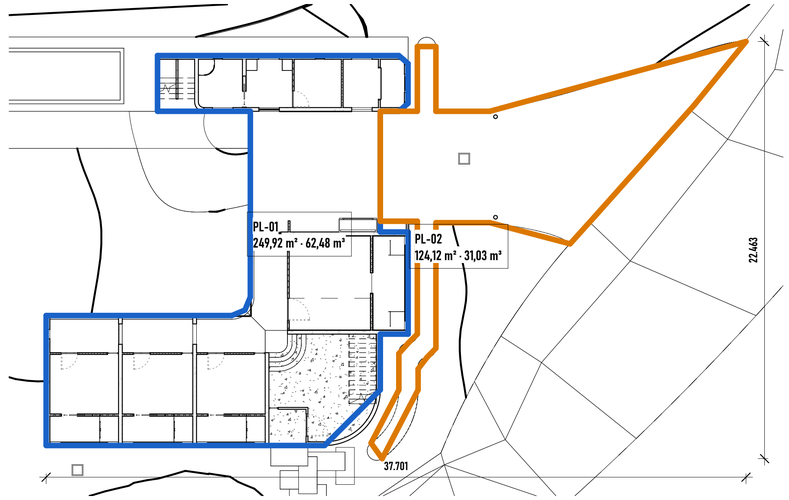

Corte tipo · platea y paquete de piso 1:10

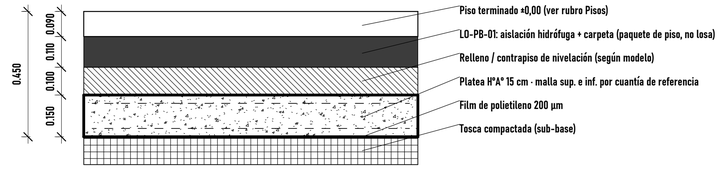

Niveles del modelo: platea −0,45 / −0,20 (tipo «Platea PB 15CM»: tosca + film + H°) · LO-PB-01 −0,61 / −0,09 · NPT ±0,00

Referencias

Azul: PL-01 platea existente
Naranja: PL-02 ampliación R31 (bajo LO-PB-01)
Tipo «Platea PB 15CM»: tosca + film + H°A° 15
Nivel superior −0,20 · fondo −0,45

Platea

PL-01 · 249,92 m² · 62,48 m² · perímetro 91,85 m
PL-02 · 124,12 m² · 31,03 m² · perímetro 86,08 m
Total platea · 374,04 m² · 93,51 m³
(perímetro exterior de la unión: ver EST-00)

Estructura R31 (archivo de documentación con el modelo principal vinculado). Toda la PB apoya sobre platea H°A° 15 cm (PL-01 + ampliación PL-02 R31) sobre film y tosca compactada; LO-PB-01 se documenta como paquete de piso. Armadura por cuantía de referencia hasta el cálculo. Cotas en metros.

https://ezeader.myportfolio.com/ezequiel-ader

Consultant
Address
Address
Phone
Fax
e-mail

Consultant
Address
Address
Phone
Fax
e-mail

Consultant
Address
Address
Phone
Fax
e-mail

Consultant
Address
Address
Phone
Fax
e-mail

No.	Description	Date

Angel Luis Brusca

CASA ANGEL

EST-FU-01

Project number	0001
Date	18 de Agosto, 2025
Drawn by	Author
Checked by	Checker

Estructura · FU-01

Scale As indicated

10/25/2026 12:07:35 AM