

CASA ÁNGEL · CLIMATIZACIÓN · COLECTOR CO-S · DETALLE

CO-S · Colector Sur · Sala de Maquinas · 01. Planta Alta · 12 circuitos · planta, alzado con gabinete y esquema de salidas

CO-S · planta 1:20

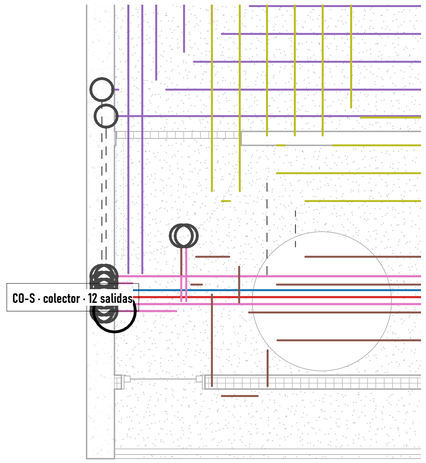


CO-S · alzado frontal con gabinete 1:20

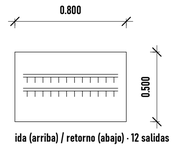

ida (arriba) / retorno (abajo) · 12 salidas

CO-S · esquema de salidas 1:25

CO-S · ida (arriba) / retorno (abajo)

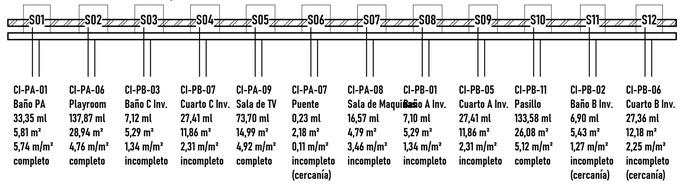

CI-PA-01	CI-PA-06	CI-PB-03	CI-PB-07	CI-PA-09	CI-PA-07	CI-PA-08	CI-PB-01	CI-PB-05	CI-PB-11	CI-PB-02	CI-PB-06
Baño PA	Playroom	Baño C Inv.	Cuarto C Inv.	Sala de TV	Puente	Sala de Maquinas	Baño A Inv.	Cuarto A Inv.	Pasillo	Baño B Inv.	Cuarto B Inv.
33,35 ml	137,87 ml	7,12 ml	27,41 ml	73,70 ml	0,23 ml	16,57 ml	7,10 ml	27,41 ml	133,58 ml	6,90 ml	27,36 ml
5,81 m²	28,94 m²	5,29 m²	11,86 m²	14,99 m²	2,18 m²	4,79 m²	5,29 m²	11,86 m²	26,08 m²	5,43 m²	12,18 m²
5,74 m/m²	4,76 m/m²	1,34 m/m²	2,31 m/m²	4,92 m/m²	0,11 m/m²	3,46 m/m²	1,34 m/m²	2,31 m/m²	5,12 m/m²	1,27 m/m²	2,25 m/m²
completo	completo	incompleto	incompleto	completo	incompleto (cercanía)	incompleto	incompleto	incompleto	completo	incompleto (cercanía)	incompleto (cercanía)

Cuadro CO-S

Salidas usadas: 12
Serpentín: 498,60 ml · 134,70 m² servidos
Completos (≥ 4 m/m²): 4 de 12
Asignados por cercanía: 3

Termostatos que comanda

TE-06 · Baño A Inv.
TE-07 · Baño B Inv.
TE-08 · Baño C Inv.
TE-11 · Playroom

Montantes de llegada

DI-PE · 22 tramos verticales
DI-PA · 31 tramos verticales
DI-PB · 6 tramos verticales

Climatización R32 (archivo de documentación con el modelo principal vinculado). Piso radiante: serpentines PEX Ø20 (mando + retorno) trazados sobre el eje de cada tubo del modelo; colector de cada circuito por conectividad de tubos y accesorios. Densidad completa ≥ 4 m/m². Bomba de calor: no modelada.

https://ezeader.myportfolio.com/ezequiel-ader

Consultant
Address
Address
Phone
Fax
e-mail

Consultant
Address
Address
Phone
Fax
e-mail

Consultant
Address
Address
Phone
Fax
e-mail

Consultant
Address
Address
Phone
Fax
e-mail

No.	Description	Date

Angel Luis Brusca

CASA ANGEL

CLI-CO-S

Project number	0001
Date	18 de Agosto, 2025
Drawn by	Author
Checked by	Checker

Climatización · CO-S

Scale: As indicated

10/25/2026 11:36:37 AM