

CASA ÁNGEL · CLIMATIZACIÓN · CIRCUITO CI-PB-06 · CUARTO B INV.

CI-PB-06 · Cuarto B Inv. · 27,36 ml · 2,25 m/m²

CI-PB-06 · planta 1:15

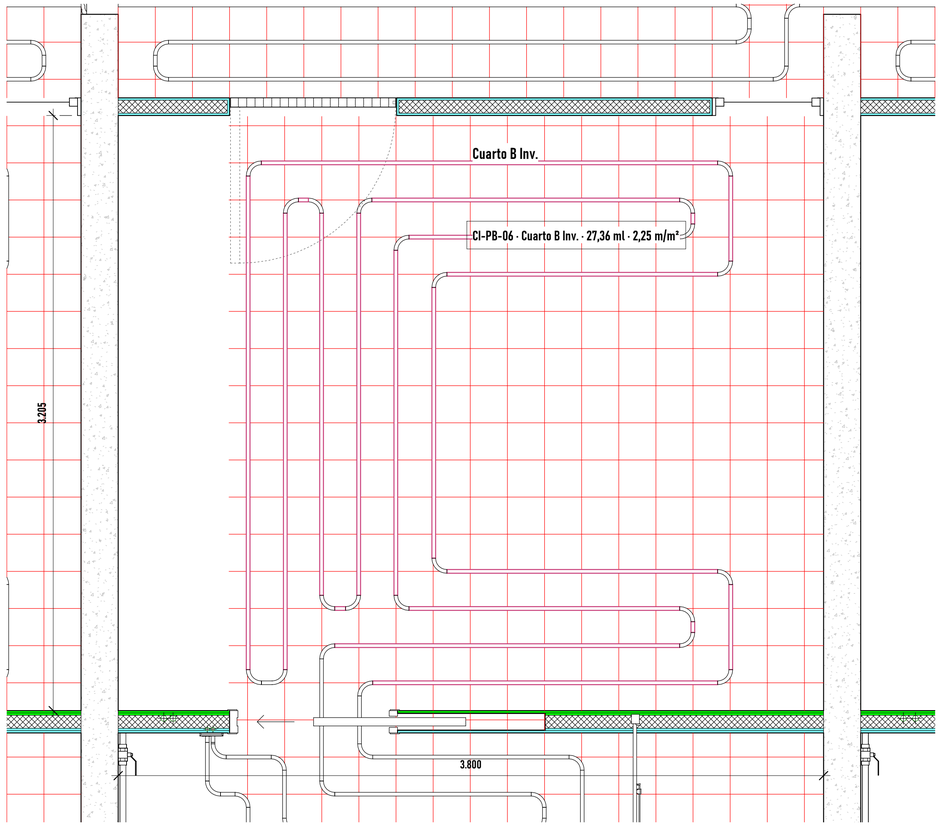

CI-PB-06 · axonométrica 1:25

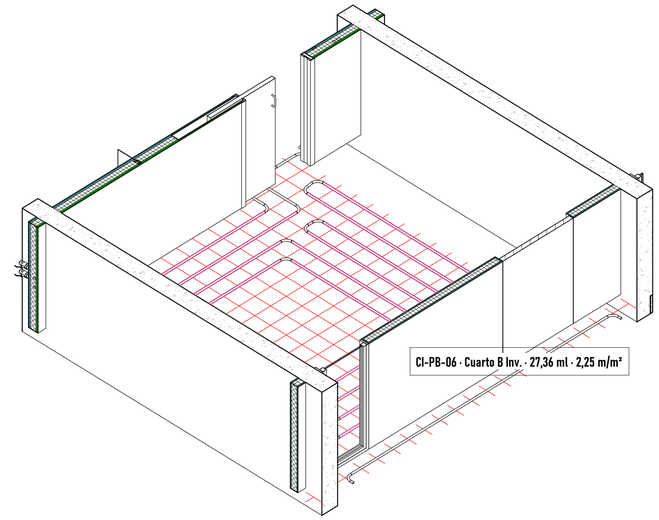

CI-PB-06 · Cuarto B Inv. · 27,36 ml · 2,25 m/m²
Mando 14,78 ml · Retorno 12,58 ml · Local 12,18 m²
Densidad 2,25 m/m² (paso 15 cm ≈ 6,7 m/m²) · incompleto o solo distribución (densidad < 4 m/m²)
Sistemas Revit: Hydronic Supply 19

Climatización: piso radiante con serpentines PEX Ø20 (mando + retorno) según el modelo. Longitudes por local tomadas en el nivel de cada tramo. Bomba de calor, circuitos por salida de colector y sistemas de retorno: no modelado / a definir.

https://ezeader.myportfolio.com/ezequiel-ader

Consultant Address Address Phone Fax e-mail	Consultant Address Address Phone Fax e-mail
Consultant Address Address Phone Fax e-mail	Consultant Address Address Phone Fax e-mail

No.	Description	Date

Angel Luis Brusca

CASA ANGEL

CLI-F-CI-PB-06

Project number	0001
Date	18 de Agosto, 2025
Drawn by	Author
Checked by	Checker

Climatización · CI-PB-06

Scale 1 : 15

10/23/2025 5:15 PM