
CASA ÁNGEL · CLIMATIZACIÓN · CIRCUITO CI-PE-01 · ATELIER


CI-PE-01 · Atelier · 94,62 ml · 4,89 m/m²

CI-PE-01 · planta 1:20

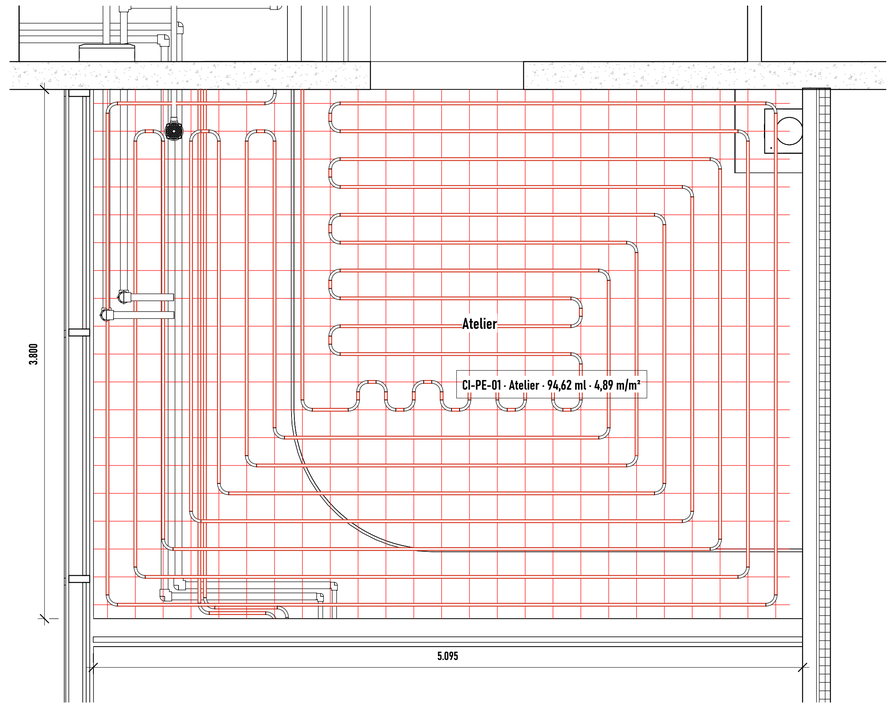

CI-PE-01 · Atelier · 94,62 ml · 4,89 m/m²
Mando 65,79 ml · Retorno 28,84 ml · Local 19,36 m²
Densidad 4,89 m/m² (paso 15 cm ≈ 6,7 m/m²) · completo
Sistemas Revit: Hydronic Supply 1

CI-PE-01 · axonométrica 1:30

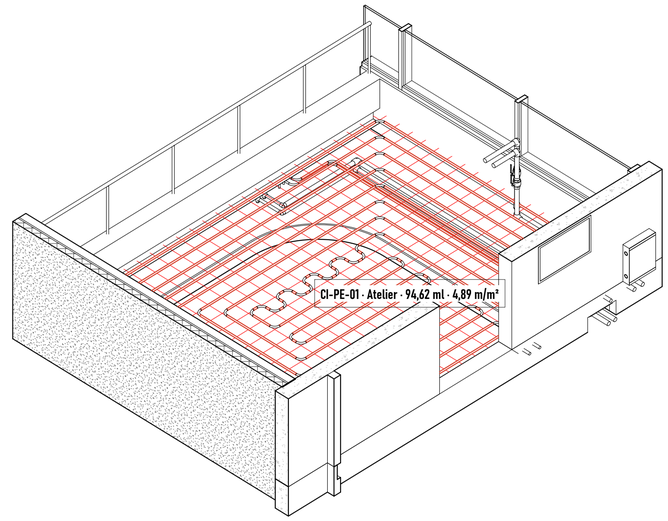

Climatización: piso radiante con serpentines PEX Ø20 (mando + retorno) según el modelo. Longitudes por local tomadas en el nivel de cada tramo. Bomba de calor, circuitos por salida de colector y sistemas de retorno: no modelado / a definir.

https://ezeader.myportfolio.com/ezequiel-ader

Consultant
Address
Address
Phone
Fax
e-mail

Consultant
Address
Address
Phone
Fax
e-mail

Consultant
Address
Address
Phone
Fax
e-mail

Consultant
Address
Address
Phone
Fax
e-mail

No.	Description	Date

Angel Luis Brusca

CASA ANGEL

CLI-F-CI-PE-01

Project number	0001
Date	18 de Agosto, 2025
Drawn by	Author
Checked by	Checker

Climatización · CI-PE-01

Scale 1 : 20

10/23/2025 5:48 PM