# CASA ÁNGEL · CLIMATIZACIÓN · COLECTOR CO-S

CO-S · Colector Sur · Sala de Maquinas

CO-S · vista 1:10

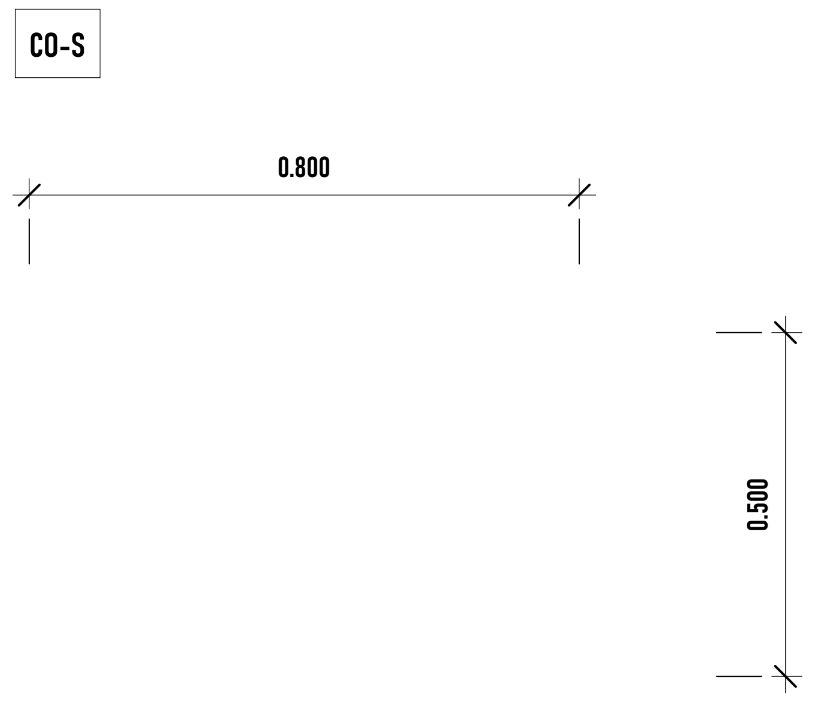

CO-S · planta 1:10

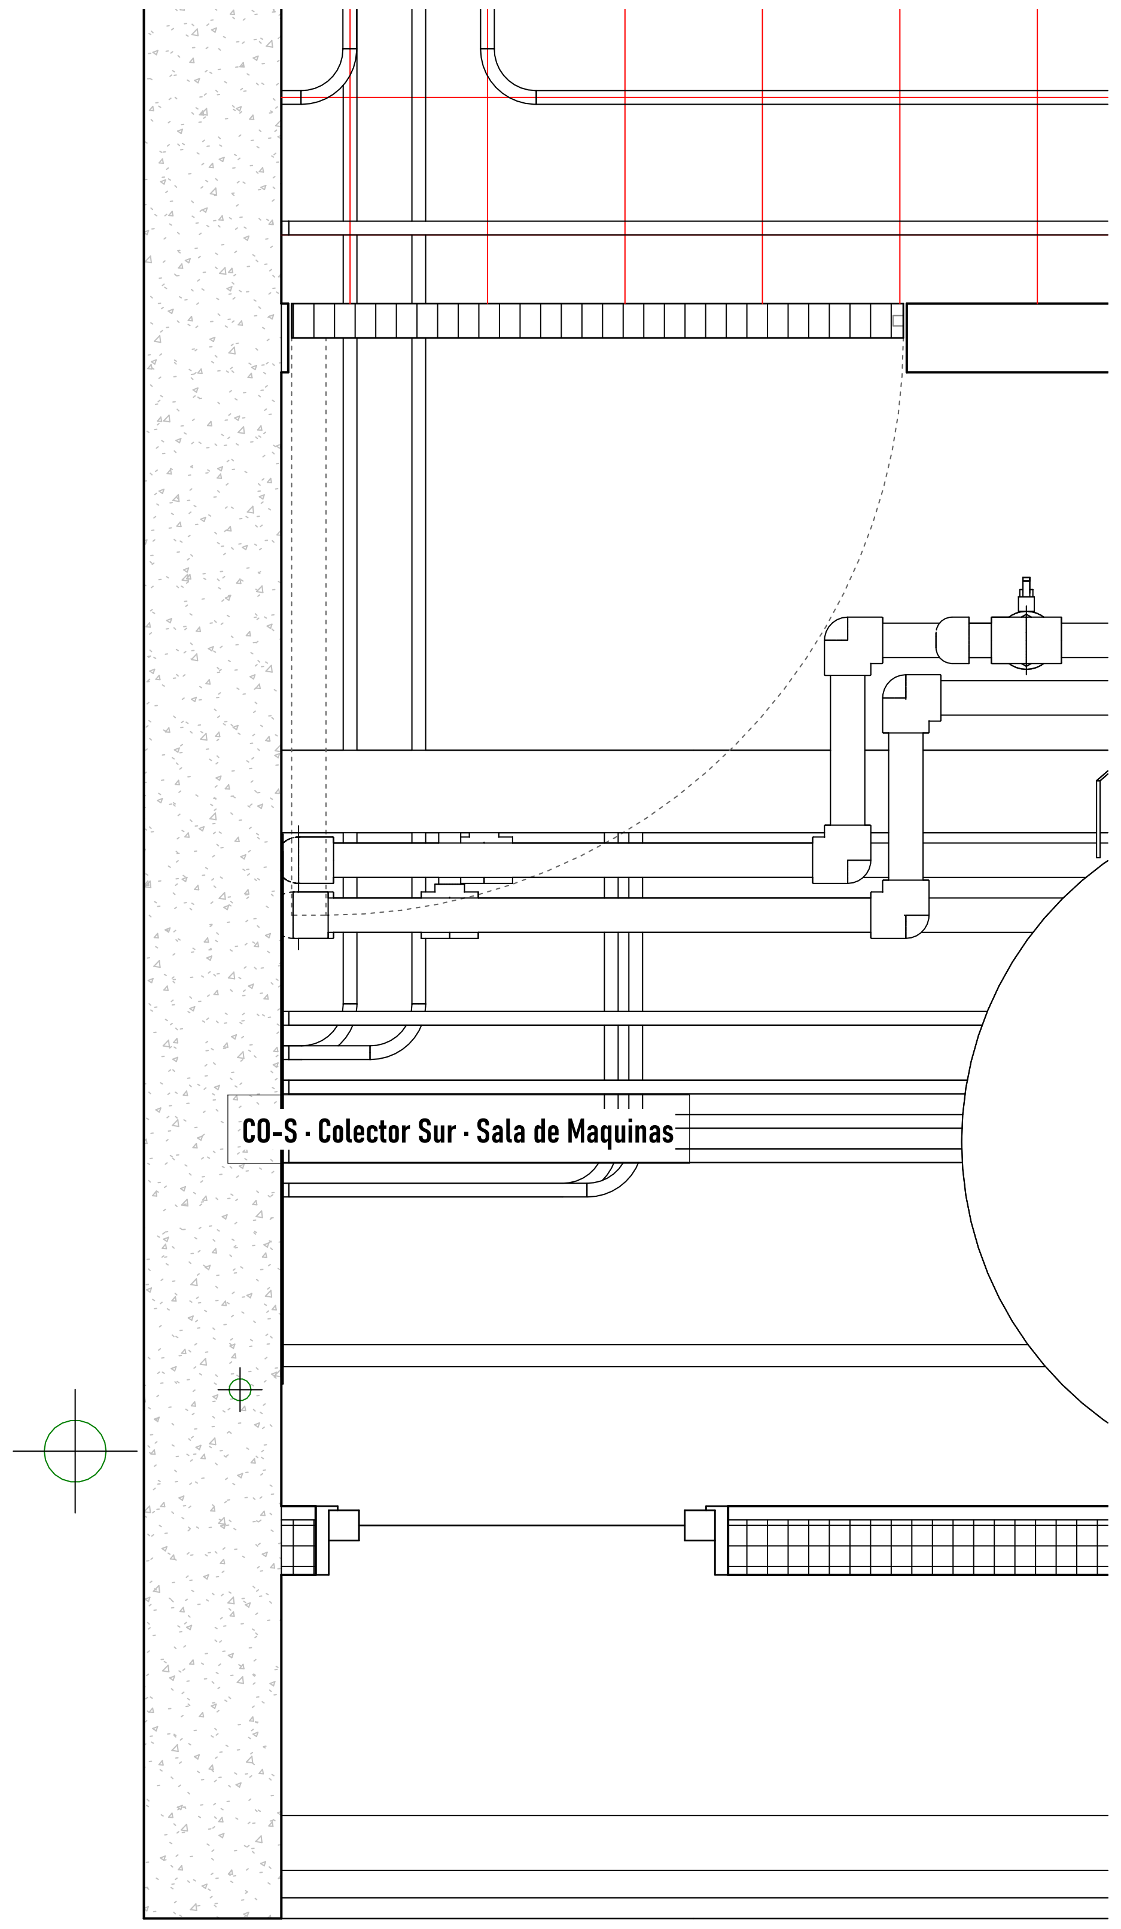

CO-S · axonométrica 1:15

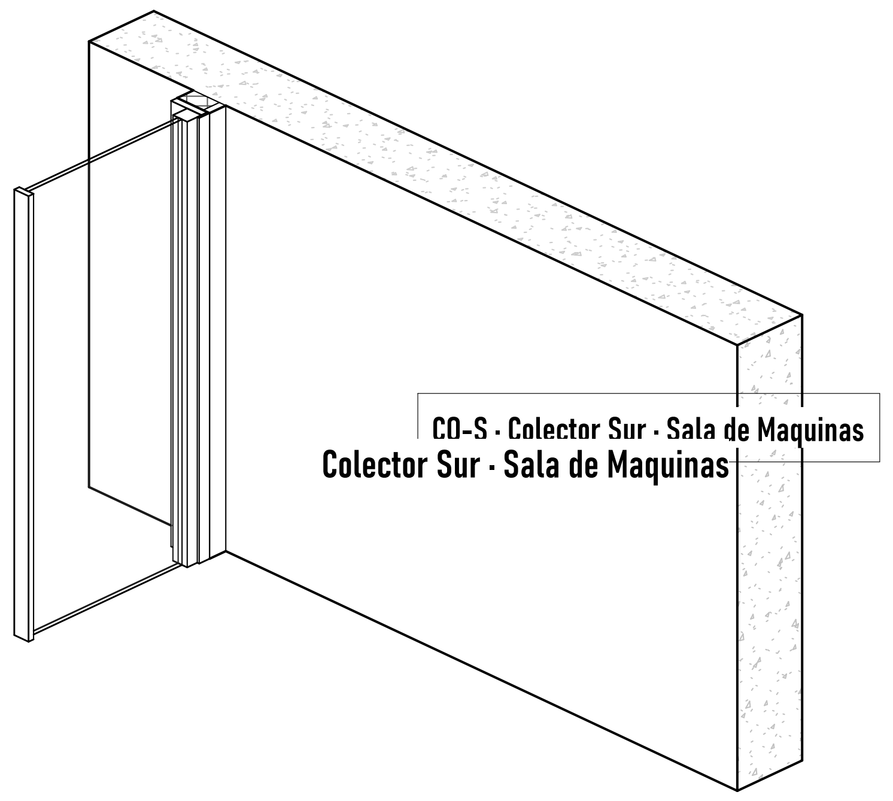
CO-S · Colector Sur · Sala de Maquinas
Colector Sur · Sala de Maquinas

CO-S · Colector Sur · Sala de Maquinas
Hidroflex - Colector Modelo LUXUS Poliamida AR · Industrias - Saladillo
Salidas y circuitos por salida: no definidos en el modelo (a definir).

Climatización: piso radiante con serpentines PEX Ø20 (mando + retorno) según el modelo. Longitudes por local tomadas en el nivel de cada tramo. Bomba de calor, circuitos por salida de colector y sistemas de retorno: no modelado / a definir.

https://ezeader.myportfolio.com/ezequiel-ader

Consultant
Address
Address
Phone
Fax
e-mail

Consultant
Address
Address
Phone
Fax
e-mail

Consultant
Address
Address
Phone
Fax
e-mail

Consultant
Address
Address
Phone
Fax
e-mail

| No. | Description | Date |
|---|---|---|

Angel Luis Brusca

CASA ANGEL

CLI-F-CO-S

Project number 0001

Date 18 de Agosto, 2025

Drawn by Author

Checked by Checker

Climatización · CO-S

Scale 1 : 10

10/23/2026 7:45:59 PM