
CASA ÁNGEL · CLIMATIZACIÓN · PISO RADIANTE · 00. PLANTA BAJA

Serpentines por local · 00. Planta Baja 1:60

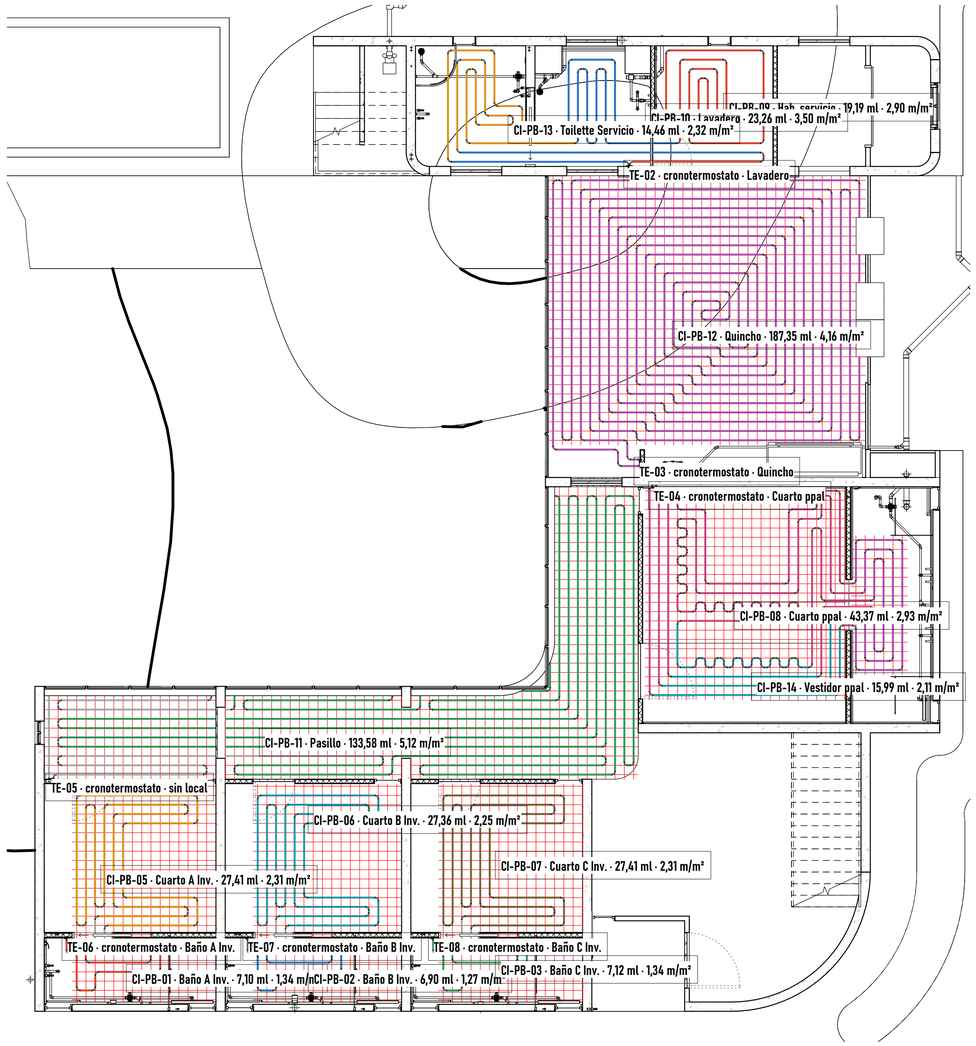

14 locales · 554,8 ml de serpentín en locales · distribución 45,8 ml

Climatización: piso radiante con serpentines PEX Ø20 (mando + retorno) según el modelo. Longitudes por local tomadas en el nivel de cada tramo. Bomba de calor, circuitos por salida de colector y sistemas de retorno: no modelado / a definir.

https://ezeader.myportfolio.com/ezequiel-ader

Consultant
Address
Address
Phone
Fax
e-mail

Consultant
Address
Address
Phone
Fax
e-mail

Consultant
Address
Address
Phone
Fax
e-mail

Consultant
Address
Address
Phone
Fax
e-mail

No.	Description	Date

Angel Luis Brusca

CASA ANGEL

CLI-PB-01

Project number	0001
Date	18 de Agosto, 2025
Drawn by	Author
Checked by	Checker

Climatización · PB

Scale 1 : 60

10/23/2026 7:46:05 PM