
CASA ÁNGEL · CIELORRASOS · PROPUESTA DE CIELORRASOS · 01. PLANTA ALTA

Cielorrasos propuestos · 01. Planta Alta 1:60

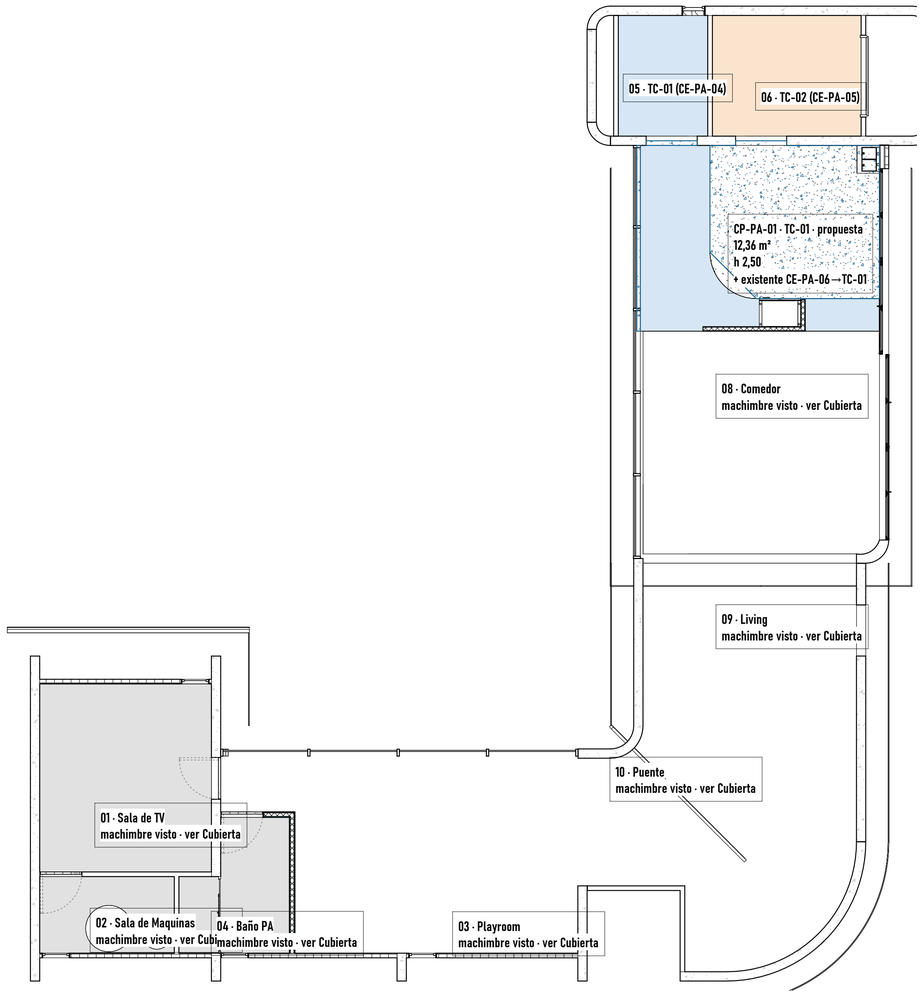

PROPUESTA · RH 25,88 m² · ST 8,33 m² · propuesto 12,36 m² (rayado) · buña 41,30 ml

PROPUESTA · Cielorrasos suspendidos de placa de yeso 12,5 sobre perfilería galvanizada: TC-01 RH en zonas húmedas, TC-02 ST en el resto; buña Z 15; tapas 60×60. Rayado: propuesto (CP); liso: existente. Bajo la cubierta de madera: machimbre visto (ver Cubierta). El modelo no se modificó.

https://ezeader.myportfolio.com/ezequiel-ader

Consultant
Address
Address
Phone
Fax
e-mail

Consultant
Address
Address
Phone
Fax
e-mail

Consultant
Address
Address
Phone
Fax
e-mail

Consultant
Address
Address
Phone
Fax
e-mail

No.	Description	Date

Angel Luis Brusca

CASA ANGEL

CIE-P-PA

Project number	0001
Date	18 de Agosto, 2025
Drawn by	Author
Checked by	Checker

Cielorrasos · propuesta PA

Scale 1 : 60

10/24/2026 9:55:15 AM