
CASA ÁNGEL · ALBAÑILERÍA · PLANO MAESTRO DE MUROS · 01. PLANTA ALTA

Planta · 01. Planta Alta 1:75

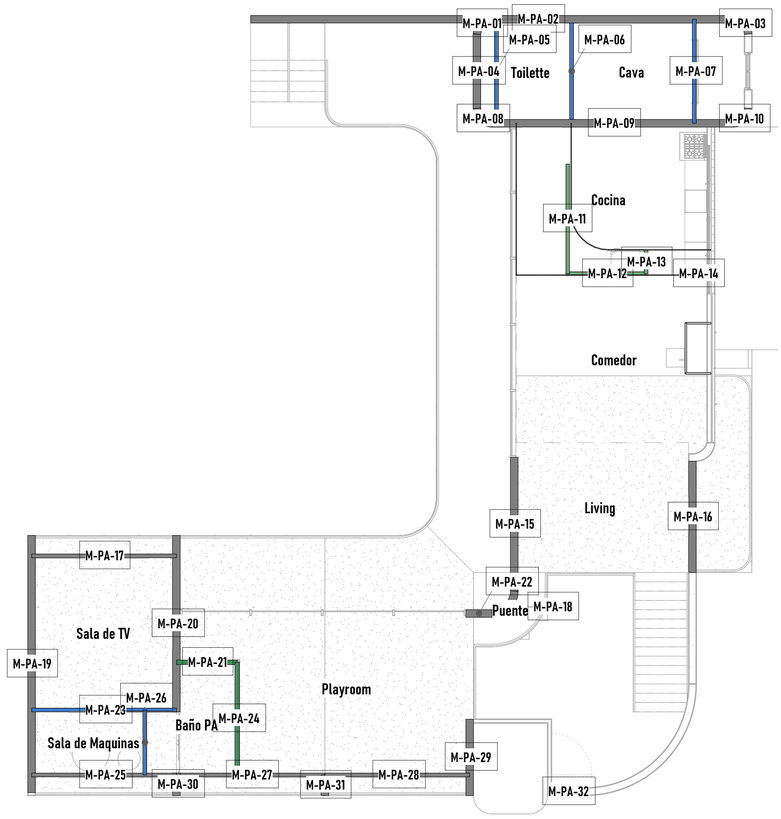

32 muros codificados · color por categoría · medidas en el cuadro

Albañilería R38 (archivo de documentación con el modelo principal vinculado, sin modificarlo). Color por categoría de muro; los muros de H° se computan en Estructura. Códigos M-‹nivel›-nn de izquierda a derecha y de arriba hacia abajo. Medidas en metros: largo × alto × espesor.

Referencias

Gris: H° visto (se computa en Estructura)
Naranja: Exterior – interior (TM-05)
Azules/verdes: Interior – interior · TM-01/02/03 mampostería, TM-07/08 Durlock
Gris claro: Otros (no es muro de albañilería) (TM-09 chimenea, TM-10 cierre de cielorraso), sin código
Medidas: largo × alto × espesor (m)

Muros PA · largo × alto × espesor (m)

M-PA-01 · H° (Estructura) · 0,63 × 3,00 × 0,20
M-PA-02 · H° (Estructura) · 13,00 × 3,00 × 0,20
M-PA-03 · H° (Estructura) · 0,63 × 3,00 × 0,20
M-PA-04 · H° (Estructura) · 2,00 × 3,00 × 0,20
M-PA-05 · TM-01 · 2,60 × 5,50 × 0,10
M-PA-06 · TM-01 · 2,80 × 2,56 × 0,10
M-PA-07 · TM-01 · 2,80 × 3,00 × 0,10
M-PA-08 · H° (Estructura) · 0,63 × 3,00 × 0,20
M-PA-09 · H° (Estructura) · 6,50 × 3,00 × 0,20
M-PA-10 · H° (Estructura) · 0,63 × 3,00 × 0,20
M-PA-11 · TM-07 · 2,95 × 0,90 × 0,10
M-PA-12 · TM-07 · 2,11 × 2,80 × 0,10
M-PA-13 · TM-07 · 0,64 × 2,80 × 0,10
M-PA-14 · TM-07 · 0,70 × 0,90 × 0,10
M-PA-15 · H° (Estructura) · 3,60 × 3,00 × 0,20
M-PA-16 · H° (Estructura) · 3,00 × 3,00 × 0,20
M-PA-17 · TM-06 · 3,90 × 2,80 × 0,10
M-PA-18 · H° (Estructura) · 0,94 × 3,00 × 0,20
M-PA-19 · H° (Estructura) · 6,92 × 2,50 × 0,20
M-PA-20 · H° (Estructura) · 4,75 × 3,00 × 0,20
M-PA-21 · TM-08 · 1,64 × 3,30 × 0,12
M-PA-22 · H° (Estructura) · 0,70 × 3,00 × 0,20
M-PA-23 · TM-01 · 3,90 × 3,30 × 0,10
M-PA-24 · TM-08 · 3,04 × 2,80 × 0,12
M-PA-25 · TM-06 · 3,90 × 2,50 × 0,10
M-PA-26 · TM-01 · 1,75 × 2,70 × 0,10
M-PA-27 · TM-06 · 4,00 × 2,50 × 0,10
M-PA-28 · TM-06 · 3,90 × 2,50 × 0,10
M-PA-29 · H° (Estructura) · 2,05 × 3,30 × 0,20
M-PA-30 · H° (Estructura) · 0,60 × 2,80 × 0,20
M-PA-31 · H° (Estructura) · 0,55 × 2,80 × 0,20
M-PA-32 · H° (Estructura) · 0,95 × 5,50 × 0,20

https://ezeader.myportfolio.com/ezequiel-ader

Consultant
Address
Address
Phone
Fax
e-mail

Consultant
Address
Address
Phone
Fax
e-mail

Consultant
Address
Address
Phone
Fax
e-mail

Consultant
Address
Address
Phone
Fax
e-mail

No.	Description	Date

Angel Luis Brusca

CASA ANGEL

ALB-PA-01

Project number	0001
Date	18 de Agosto, 2025
Drawn by	Author
Checked by	Checker

Albañilería · PA-01

Scale 1 : 75

10/30/2026 6:11:11 PM