

CASA ÁNGEL · ALBAÑILERÍA · MUROS M-PA-09 A M-PA-12 · VISTA Y CORTE

01. Planta Alta · 4 muros · alzado con vanos y medidas + corte con capas


M-PA-09 · vista · H° (Estructura) 1:50

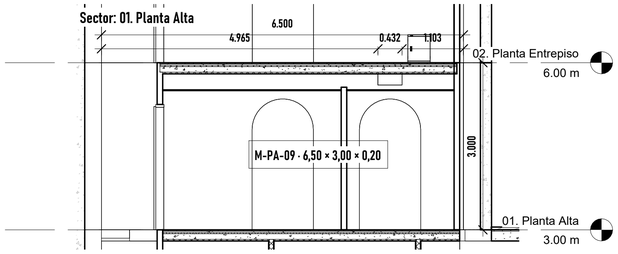


M-PA-10 · vista · H° (Estructura) 1:50

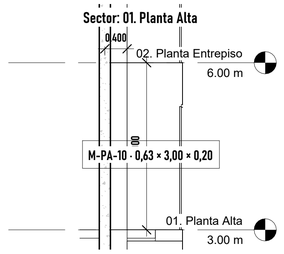

M-PA-11 · vista · TM-07 1:50

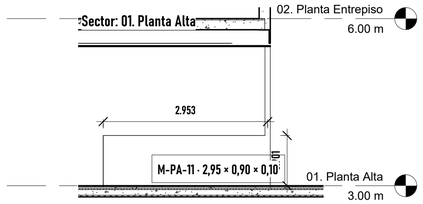


M-PA-12 · vista · TM-07 1:50

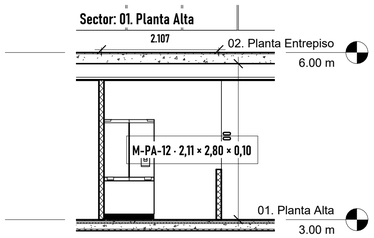


M-PA-09 · corte (capas) 1:50




M-PA-10 · corte (capas) 1:10

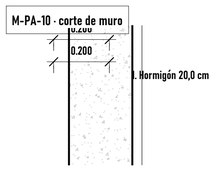

M-PA-11 · corte (capas) 1:10

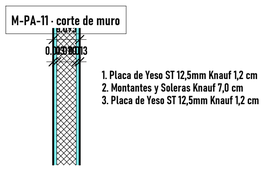

M-PA-12 · corte (capas) 1:10

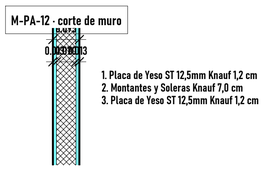

Albañilería R38 (archivo de documentación con el modelo principal vinculado, sin modificarlo). Color por categoría de muro; los muros de H° se computan en Estructura. Códigos M-‹nivel›-nn de izquierda a derecha y de arriba hacia abajo. Medidas en metros: largo × alto × espesor.

https://ezeader.myportfolio.com/ezequiel-ader

Consultant
Address
Address
Phone
Fax
e-mail

Consultant
Address
Address
Phone
Fax
e-mail

Consultant
Address
Address
Phone
Fax
e-mail

Consultant
Address
Address
Phone
Fax
e-mail

No.	Description	Date

Angel Luis Brusca

CASA ANGEL

ALB-PA-04

Project number	0001
Date	18 de Agosto, 2025
Drawn by	Author
Checked by	Checker

Albañilería · PA-04

Scale As indicated

10/30/2026 6:11:47 PM