

CASA ÁNGEL · ALBAÑILERÍA · MUROS M-PB-29 A M-PB-32 · VISTA Y CORTE

00. Planta Baja · 4 muros · alzado con vanos y medidas + corte con capas


M-PB-29 · vista · Hº (Estructura) 1:50

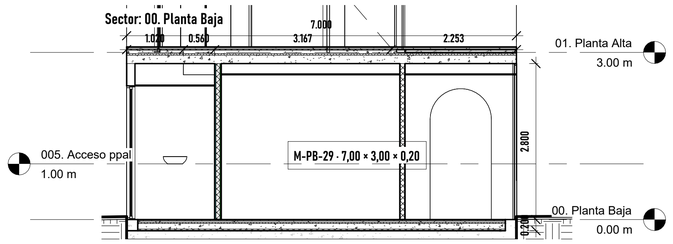


M-PB-30 · vista · TM-07 1:50

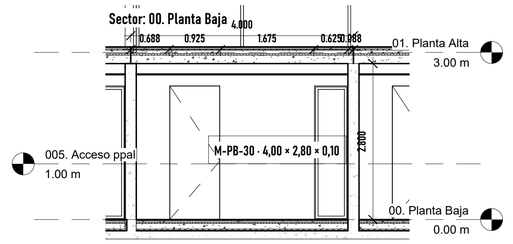


M-PB-31 · vista · Hº (Estructura) 1:50

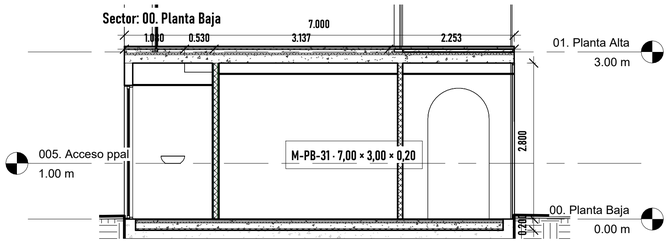


M-PB-32 · vista · TM-07 1:50

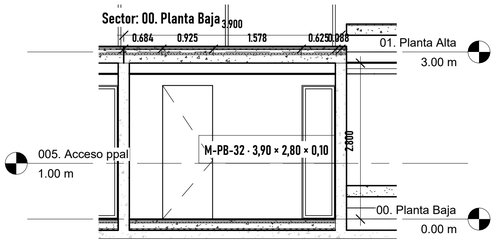


M-PB-29 · corte (capas) 1:50

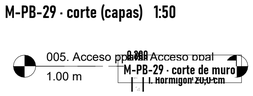


M-PB-30 · corte (capas) 1:10

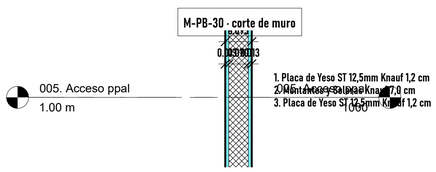

M-PB-31 · corte (capas) 1:10

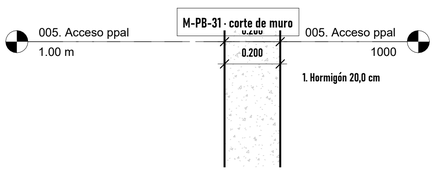

M-PB-32 · corte (capas) 1:10

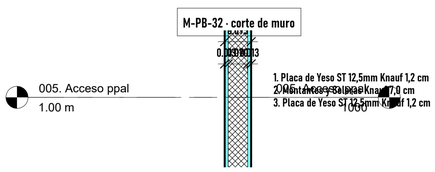

Albañilería R38 (archivo de documentación con el modelo principal vinculado, sin modificarlo). Color por categoría de muro; los muros de Hº se computan en Estructura. Códigos M-‹nivel›-nn de izquierda a derecha y de arriba hacia abajo. Medidas en metros: largo × alto × espesor.

https://ezeader.myportfolio.com/ezequiel-ader

Consultant
Address
Address
Phone
Fax
e-mail

Consultant
Address
Address
Phone
Fax
e-mail

Consultant
Address
Address
Phone
Fax
e-mail

Consultant
Address
Address
Phone
Fax
e-mail

No.	Description	Date

Angel Luis Brusca

CASA ANGEL

ALB-PB-09

Project number	0001
Date	18 de Agosto, 2025
Drawn by	Author
Checked by	Checker

Albañilería · PB-09

Scale: As indicated

10/30/2026 6:13:49 PM