
CASA ÁNGEL · ALBAÑILERÍA · PLANO MAESTRO DE MUROS · 02. PLANTA ENTREPISO

Planta · 02. Planta Entrepiso 1:50

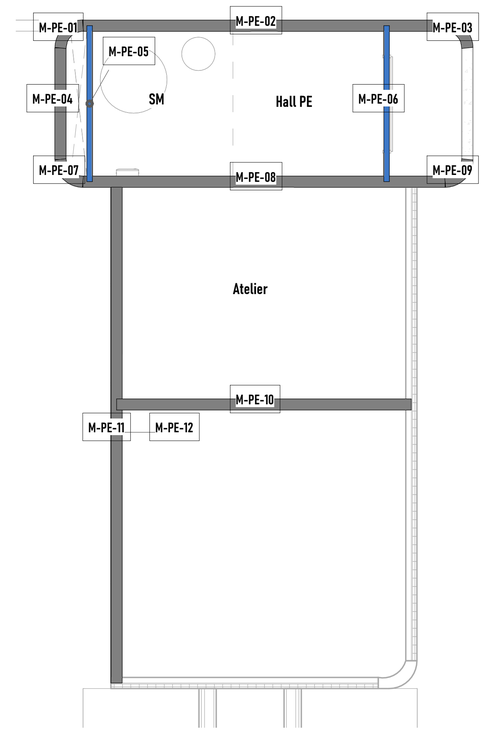

Referencias

Gris: Hº visto (se computa en Estructura)
Naranja: Exterior – interior (TM-05)
Azules/verdes: Interior – interior · TM-01/02/03 mampostería, TM-07/08 Durlock
Gris claro: Otros (no es muro de albañilería) (TM-09 chimenea, TM-10 cierre de cielorraso), sin código
Medidas: largo × alto × espesor (m)

Muros PE · largo × alto × espesor (m)

M-PE-01 · Hº (Estructura) · 0,63 × 3,00 × 0,20
M-PE-02 · Hº (Estructura) · 6,50 × 2,50 × 0,20
M-PE-03 · Hº (Estructura) · 0,63 × 2,50 × 0,20
M-PE-04 · Hº (Estructura) · 2,00 × 3,00 × 0,20
M-PE-05 · TM-01 · 2,80 × 2,30 × 0,10
M-PE-06 · TM-01 · 2,80 × 3,00 × 0,10
M-PE-07 · Hº (Estructura) · 0,63 × 3,00 × 0,20
M-PE-08 · Hº (Estructura) · 6,50 × 2,50 × 0,20
M-PE-09 · Hº (Estructura) · 0,63 × 3,00 × 0,20
M-PE-10 · Hº (Estructura) · 5,29 × 0,60 × 0,20
M-PE-11 · Hº (Estructura) · 9,00 × 0,78 × 0,20
M-PE-12 · Hº (Estructura) · 9,00 × 0,60 × 0,20

12 muros codificados · color por categoría · medidas en el cuadro

Albañilería R38 (archivo de documentación con el modelo principal vinculado, sin modificarlo). Color por categoría de muro; los muros de Hº se computan en Estructura. Códigos M-‹nivel›-nn de izquierda a derecha y de arriba hacia abajo. Medidas en metros: largo × alto × espesor.

https://ezeader.myportfolio.com/ezequiel-ader

Consultant
Address
Address
Phone
Fax
e-mail

Consultant
Address
Address
Phone
Fax
e-mail

Consultant
Address
Address
Phone
Fax
e-mail

Consultant
Address
Address
Phone
Fax
e-mail

No.	Description	Date

Angel Luis Brusca

CASA ANGEL

ALB-PE-01

Project number	0001
Date	18 de Agosto, 2025
Drawn by	Author
Checked by	Checker

Albañilería · PE-01

Scale 1 : 50

10/30/2026 6:14:27 PM