

CASA ÁNGEL · ALBAÑILERÍA · MUROS M-PE-09 A M-PE-12 · VISTA Y CORTE

02. Planta Entrepiso · 4 muros · alzado con vanos y medidas + corte con capas


M-PE-09 · vista · H° (Estructura) 1:50

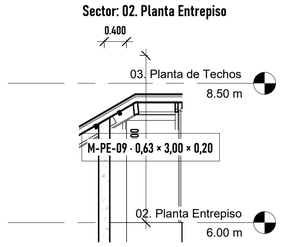


M-PE-10 · vista · H° (Estructura) 1:50

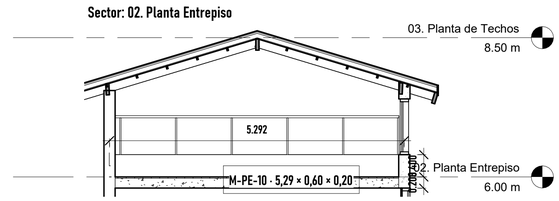

M-PE-11 · vista · H° (Estructura) 1:50

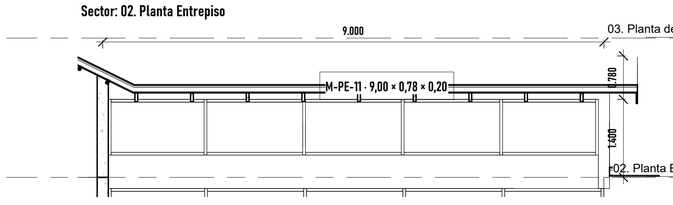


M-PE-12 · vista · H° (Estructura) 1:50

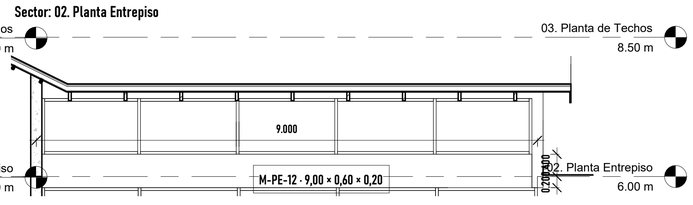


M-PE-09 · corte (capas) 1:50




M-PE-10 · corte (capas) 1:10

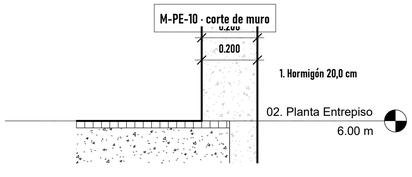

M-PE-11 · corte (capas) 1:10

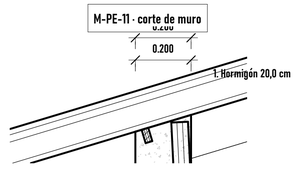

M-PE-12 · corte (capas) 1:10

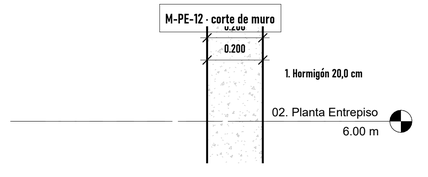

Albañilería R38 (archivo de documentación con el modelo principal vinculado, sin modificarlo). Color por categoría de muro; los muros de H° se computan en Estructura. Códigos M-<nivel>-nn de izquierda a derecha y de arriba hacia abajo. Medidas en metros: largo × alto × espesor.

https://ezeader.myportfolio.com/ezequiel-ader

Consultant
Address
Address
Phone
Fax
e-mail

Consultant
Address
Address
Phone
Fax
e-mail

Consultant
Address
Address
Phone
Fax
e-mail

Consultant
Address
Address
Phone
Fax
e-mail

No.	Description	Date

Angel Luis Brusca

CASA ANGEL

ALB-PE-04

Project number	0001
Date	18 de Agosto, 2025
Drawn by	Author
Checked by	Checker

Albañilería · PE-04

Scale As indicated

10/30/2026 6:14:51 PM