
# CASA ÁNGEL · PARRILLA · CONDUCTO DE HUMOS: CORTE ESQUEMÁTICO

## D-02a · Conducto: corte esquemático 1:50

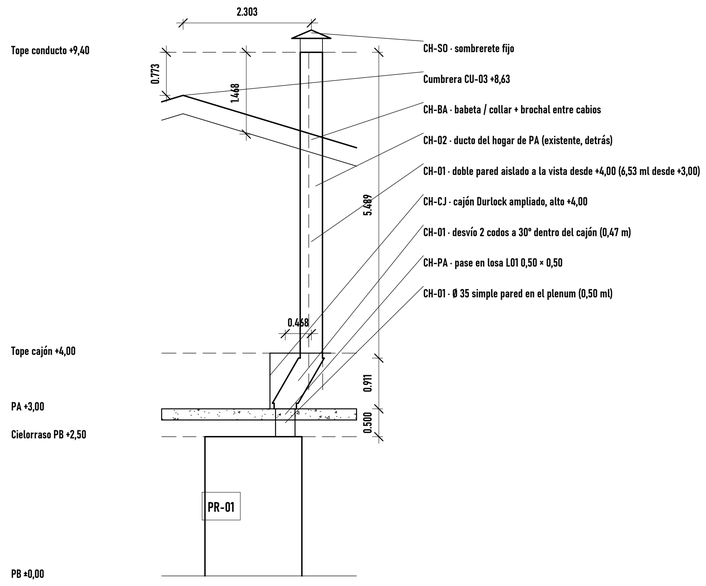


Corte esquemático este-oeste por el eje del conducto
Remate ≥ 0,60 sobre la cumbrera a menos de 3 m · cotas en m

**Ø 35: simple pared en el plenum de PB, doble pared aislado desde la PA · remate +9,40 sobre cumbrera +8,63**

Parrilla R34 (archivo de documentación con el modelo principal vinculado). Parrilla de obra a medida en el Quincho: boca 1,50 m, hogar a +0,90, campana refractaria hasta +2,50, conducto Ø 35 con sombrerete fijo. Modelada en el modelo principal (OK 26/10): reemplaza al K42DB; cajón Durlock ampliado. Cotas en m.


https://ezeader.myportfolio.com/ezequiel-ader

Consultant
Address
Address
Phone
Fax
e-mail

Consultant
Address
Address
Phone
Fax
e-mail

Consultant
Address
Address
Phone
Fax
e-mail

Consultant
Address
Address
Phone
Fax
e-mail


| No. | Description | Date |
|---|---|---|
| | | |

Angel Luis Brusca

CASA ANGEL

PAR-D-02

| | |
|---|---|
| Project number | 0001 |
| Date | 18 de Agosto, 2025 |
| Drawn by | Author |
| Checked by | Checker |

Parrilla · D-02

Scale 1 : 50

10/26/2026 11:55:20 AM