

CASA ÁNGEL · ABERTURAS · 00. PLANTA BAJA · 09 HAB. SERVICIO

Hoja 1 de 2 · 2 elementos: V-147, P-90

Planta del local · 09 · Hab. servicio 1:15

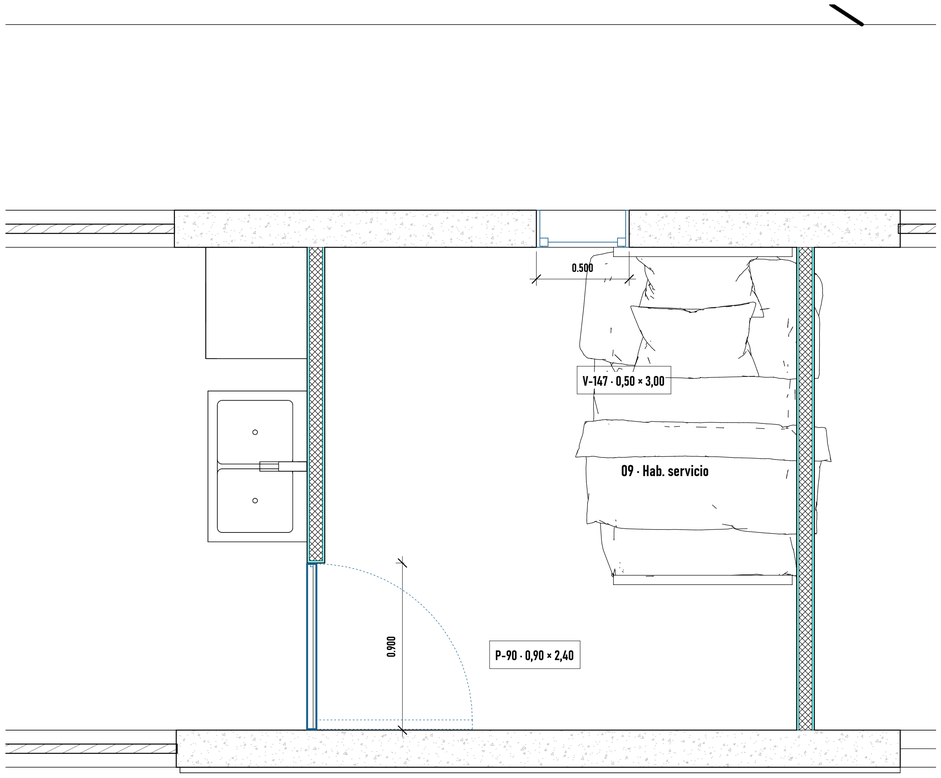

Axonométrica del local · 09 · Hab. servicio 1:25

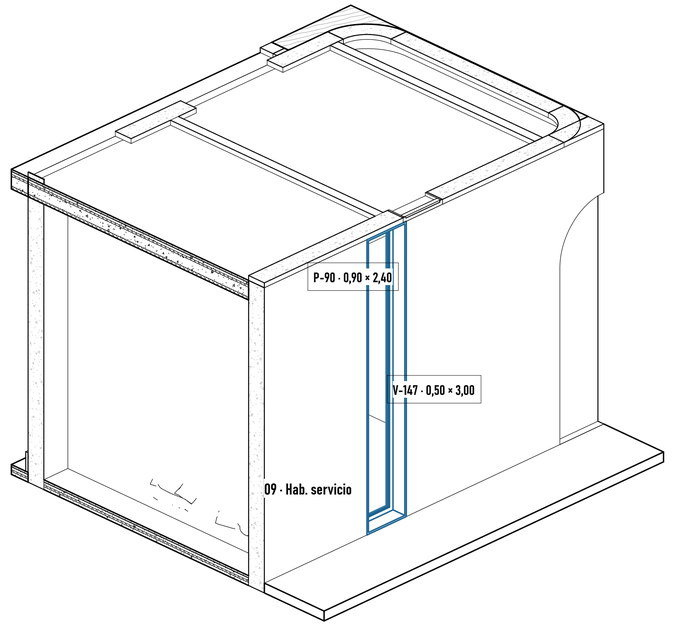

Cotas en metros (0.001 m) sobre geometría nativa. Cotas de muros cortina y cápsula del ascensor: referidas a ejes de grilla, extremos y centros de arcos (no asociativas, salvo radios). Alzados vistos desde el interior del local. Elementos compartidos entre locales: un solo cómputo por código.

https://ezeader.myportfolio.com/ezequiel-ader

Consultant
Address
Address
Phone
Fax
e-mail

Consultant
Address
Address
Phone
Fax
e-mail

Consultant
Address
Address
Phone
Fax
e-mail

Consultant
Address
Address
Phone
Fax
e-mail

No.	Description	Date

Angel Luis Brusca

CASA ANGEL

ABR-R4-PB-09

Project number	0001
Date	18 de Agosto, 2025
Drawn by	Author
Checked by	Checker

Hab. servicio · ABR 1/2


Scale 1 : 15

10/23/2025 5:15 PM

CASA ÁNGEL · ABERTURAS · 00. PLANTA BAJA · 09 HAB. SERVICIO


Hoja 2 de 2 · 2 elementos: V-147, P-90

V-147 · alzado interior 1:15

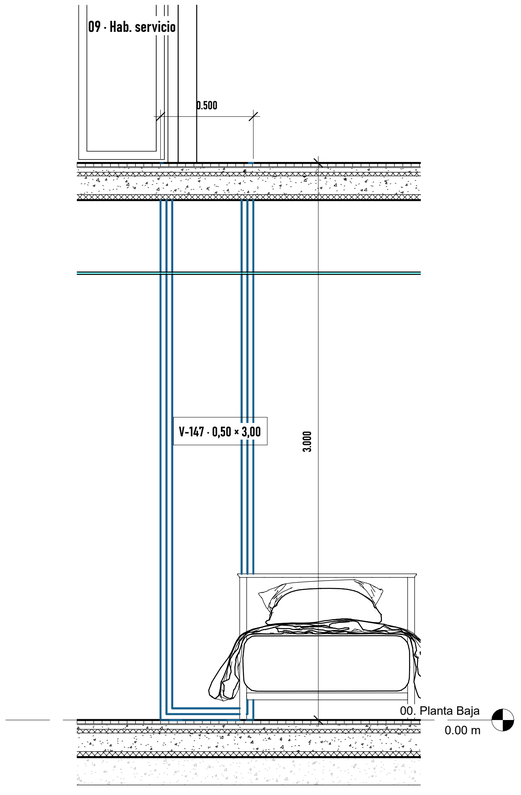

Ventanas Servicios · M_Fixed
Ancho 0.500 · Alto 3.000 · Antepecho 0.000 · Dintel 3.000 m
Muro 0.200 m · Materiales: Glass, Sash

P-90 · alzado interior 1:15

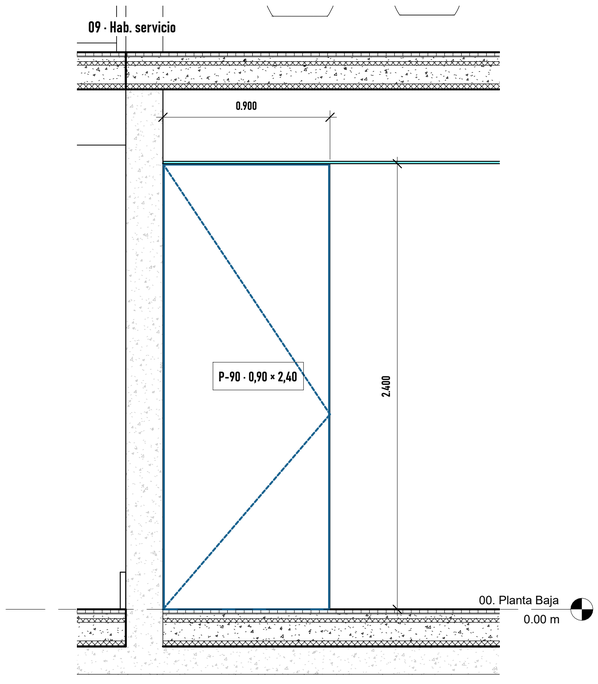

0.90 M · JALO_PUERTA ABATIBLE
Ancho 0.900 · Alto 2.400 · Antepecho 0.000 · Dintel 2.400 m
Muro 0.095 m · Materiales: Puertas
Compartida con: Lavadero (computar una vez)

Cotas en metros (0.001 m) sobre geometría nativa. Cotas de muros cortina y cápsula del ascensor: referidas a ejes de grilla, extremos y centros de arcos (no asociativas, salvo radios). Alzados vistos desde el interior del local. Elementos compartidos entre locales: un solo cómputo por código.

https://ezeader.myportfolio.com/ezequiel-ader

Consultant
Address
Address
Phone
Fax
e-mail

Consultant
Address
Address
Phone
Fax
e-mail

Consultant
Address
Address
Phone
Fax
e-mail

Consultant
Address
Address
Phone
Fax
e-mail

No.	Description	Date

Angel Luis Brusca

CASA ANGEL

ABR-R4-PB-09-2

Project number	0001
Date	18 de Agosto, 2025
Drawn by	Author
Checked by	Checker
Hab. servicio · ABR 2/2	
Scale	1 : 15

10/23/2025 5:15:16 PM