

CASA ÁNGEL · ABERTURAS · 01. PLANTA ALTA · 07 COCINA

Hoja 1 de 2 · 3 elementos: V-157, V-158, MC-612302

Planta del local · 07 · Cocina 1:30

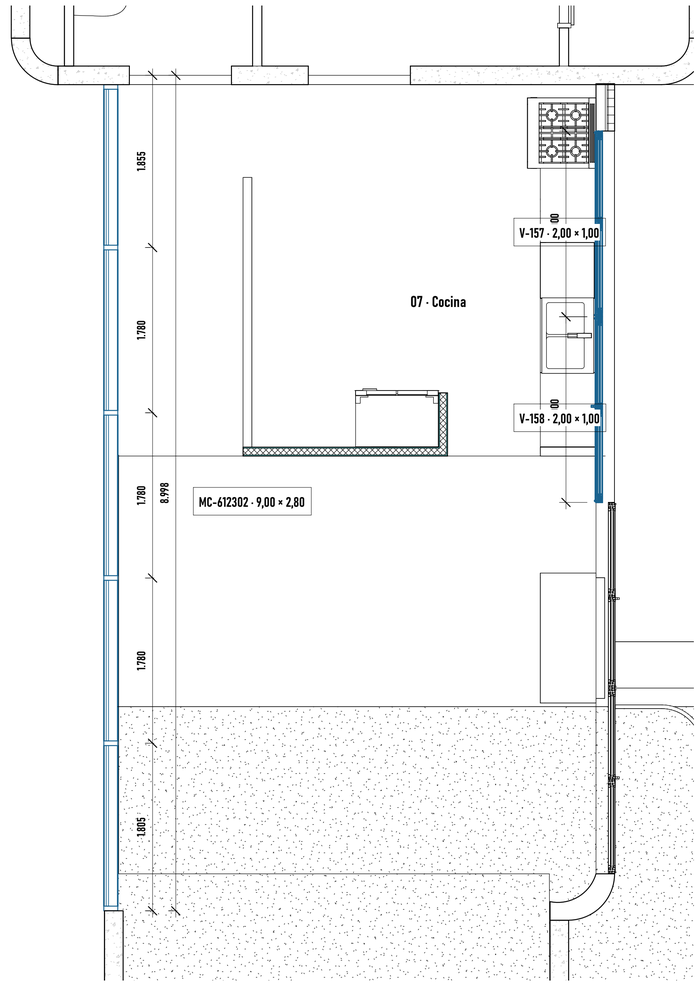

Axonométrica del local · 07 · Cocina 1:40

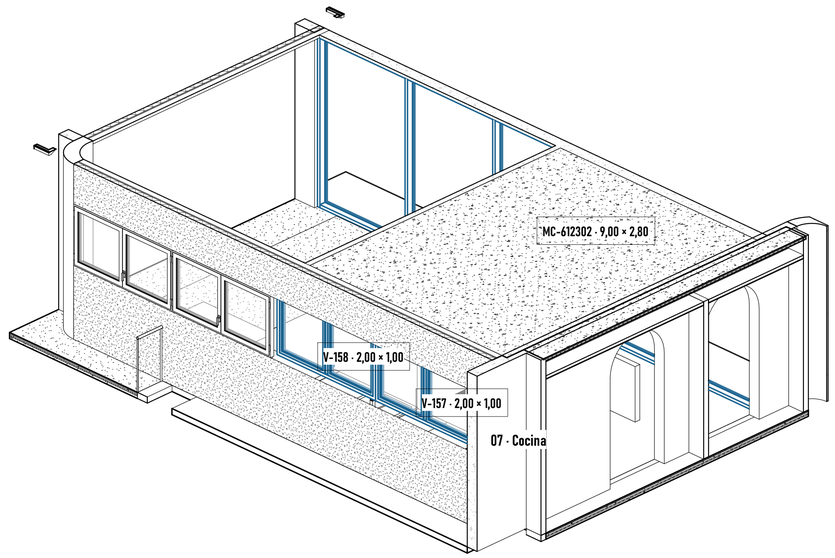

Cotas en metros (0.001 m) sobre geometría nativa. Cotas de muros cortina y cápsula del ascensor: referidas a ejes de grilla, extremos y centros de arcos (no asociativas, salvo radios). Alzados vistos desde el interior del local. Elementos compartidos entre locales: un solo cómputo por código.

https://ezeader.myportfolio.com/ezequiel-ader

Consultant
Address
Address
Phone
Fax
e-mail

Consultant
Address
Address
Phone
Fax
e-mail

Consultant
Address
Address
Phone
Fax
e-mail

Consultant
Address
Address
Phone
Fax
e-mail

No.	Description	Date

Angel Luis Brusca

CASA ANGEL

ABR-R4-PA-07

Project number	0001
Date	18 de Agosto, 2025
Drawn by	Author
Checked by	Checker

Cocina · ABR 1/2


Scale 1 : 30

10/23/2026 5:01:33 PM

CASA ÁNGEL · ABERTURAS · 01. PLANTA ALTA · 07 COCINA


Hoja 2 de 2 · 3 elementos: V-157, V-158, MC-612302

V-157 · alzado interior 1:20

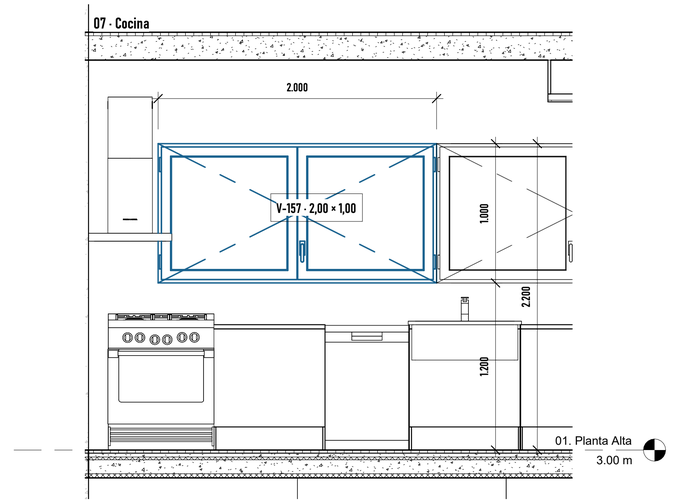


Aluprom 44 - 2 Hojas - Practicable · Ventanas
Ancho 2.000 · Alto 1.000 · Antepecho 1.200 · Dintel 2.200 m
Muro 0.200 m · Materiales: Aluminio, Cristal - Vidrio claro templado, Poliamida

V-158 · alzado interior 1:20

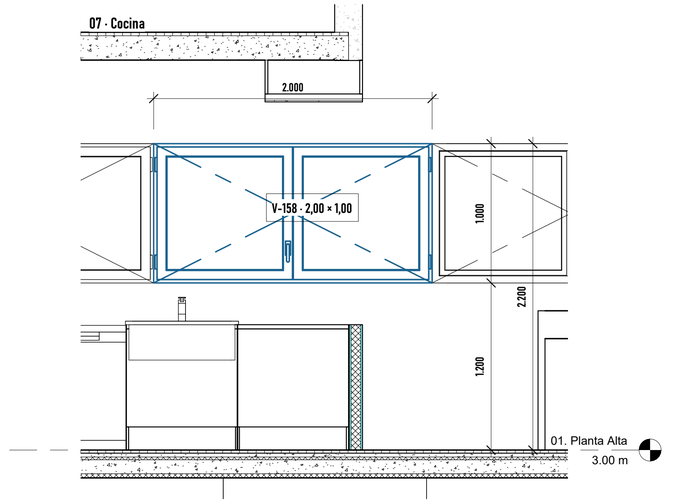

Aluprom 44 - 2 Hojas - Practicable · Ventanas
Ancho 2.000 · Alto 1.000 · Antepecho 1.200 · Dintel 2.200 m
Muro 0.200 m · Materiales: Aluminio, Cristal - Vidrio claro templado, Poliamida

MC-612302 · alzado interior 1:40

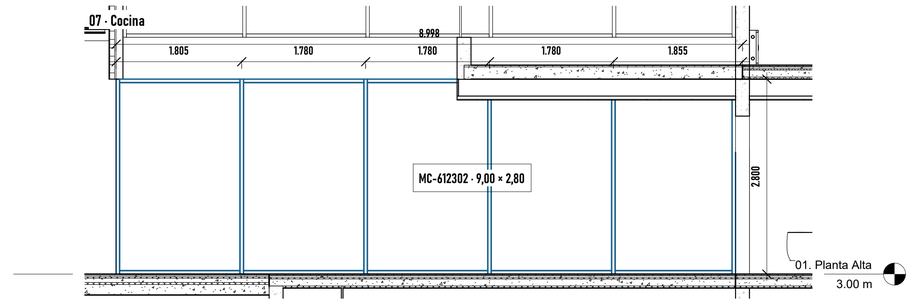

Muro cortina · Ventanales Patio · 5 paneles / 16 montantes
Largo 8.998 · Alto 2.800 · Arranque +0.000 · Superior +2.800 m
Muro 0.025 m
Compartida con: Living (computar una vez)

Cotas en metros (0.001 m) sobre geometría nativa. Cotas de muros cortina y cápsula del ascensor: referidas a ejes de grilla, extremos y centros de arcos (no asociativas, salvo radios). Alzados vistos desde el interior del local. Elementos compartidos entre locales: un solo cómputo por código.

https://ezeader.myportfolio.com/ezequiel-ader

Consultant
Address
Address
Phone
Fax
e-mail

Consultant
Address
Address
Phone
Fax
e-mail

Consultant
Address
Address
Phone
Fax
e-mail

Consultant
Address
Address
Phone
Fax
e-mail

No.	Description	Date

Angel Luis Brusca

CASA ANGEL

ABR-R4-PA-07-2

Project number	0001
Date	18 de Agosto, 2025
Drawn by	Author
Checked by	Checker

Cocina · ABR 2/2

Scale: As indicated

10/23/2026 5:01:35 PM