

CASA ÁNGEL · ABERTURAS · 00. PLANTA BAJA · 03 CUARTO B INV.

Hoja 1 de 1 · 3 elementos: V-123, P-59, P-63

Planta del local · códigos y anchos 1:20

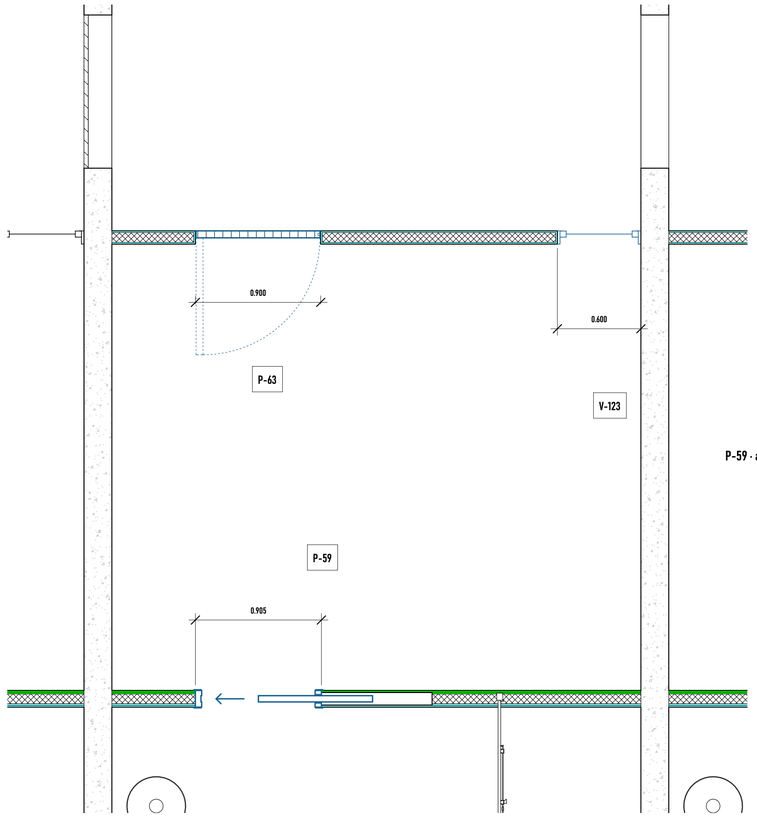


V-123 · alzado interior 1:20

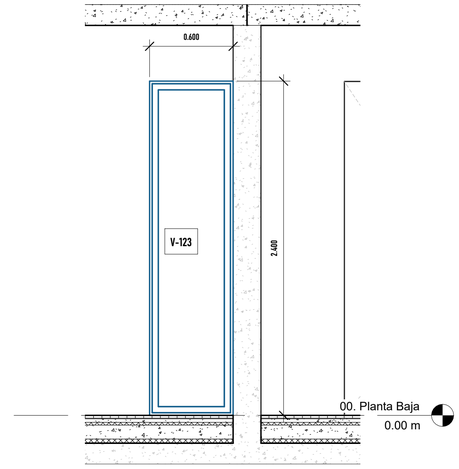


Ventana Cuartos (Muro a techo) · M_Fixed
Ancho 0.600 · Alto 2.400 · Antepecho 0.000 · Dintel 2.400 m
Tipo muro a techo: piso terminado a dintel 2.400 m (verificar con cielorrasa)
Muro 0.095 m · Materiales: Glass, Sash
Compartida con: Pasillo (computar una vez)

P-59 · alzado interior 1:20

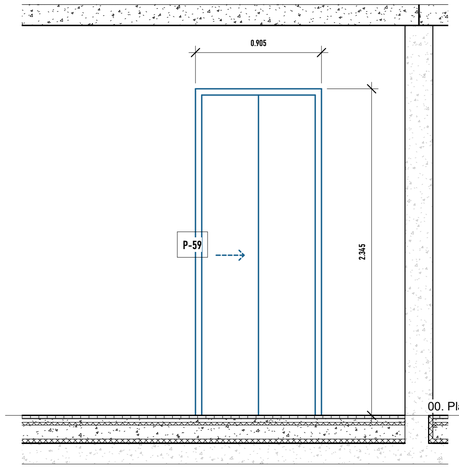

820 x 2000 mm · Puerta interior corredera
Hoja 0.820 × 2.300 · Vano 0.905 × 2.345 m
Muro 0.120 m · Materiales: Acero galvanizado, Acero inoxidable bruñido, Madera (roble), Premarco de pino
Compartida con: Baño B Inv. (computar una vez)

P-63 · alzado interior 1:20

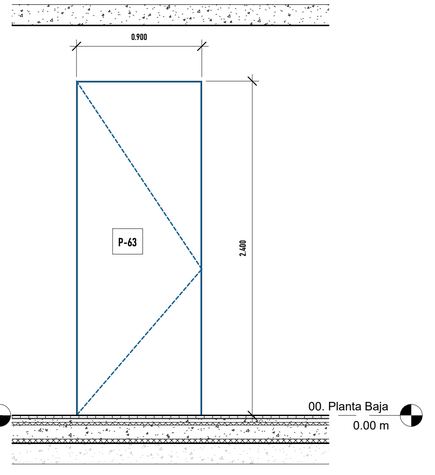

0.90 M - JALO_PUERTA ABATIBLE
Ancho 0.900 · Alto 2.400 · Antepecho 0.000 · Dintel 2.400 m
Muro 0.095 m · Materiales: Puertas
Compartida con: Pasillo (computar una vez)

Cotas en metros (0.001 m) sobre geometría nativa. Cotas de muros cortina y cápsula del ascensor: referidas a ejes de grilla, extremos y centros de arcos (no asociativas, salvo radios). Alzados vistos desde el interior del local. Elementos compartidos entre locales: un solo cómputo por código.

https://ezeader.myportfolio.com/ezequiel-ader

Consultant
Address
Address
Phone
Fax
e-mail

Consultant
Address
Address
Phone
Fax
e-mail

Consultant
Address
Address
Phone
Fax
e-mail

Consultant
Address
Address
Phone
Fax
e-mail

No.	Description	Date

Angel Luis Brusca

CASA ANGEL

ABR-R4-PB-03

Project number	0001
Date	18 de Agosto, 2025
Drawn by	Author
Checked by	Checker

Cuarto B Inv. · ABR

Scale 1 : 20

10/23/2026 3:18:07 PM