
CASA ÁNGEL · ABERTURAS · 00. PLANTA BAJA · 17 HALL

Hoja 1 de 1 · 2 elementos: V-15, P-1

Planta del local · códigos y anchos 1:30




V-15 · alzado interior 1:15

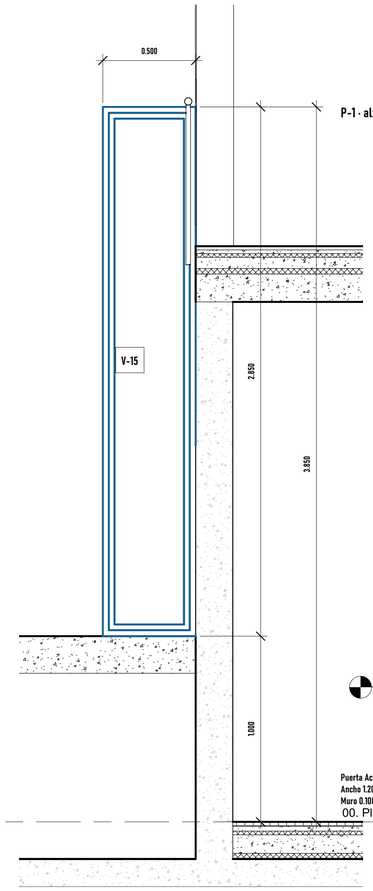

Ventanal acceso 0.5m - M_Fixed
Ancho 0.500 - Alto 2.850 - Antepecho 1.000 - Dintel 3.850 m
Muro 0.100 m - Materiales: Glass, Sash

P-1 · alzado interior 1:15

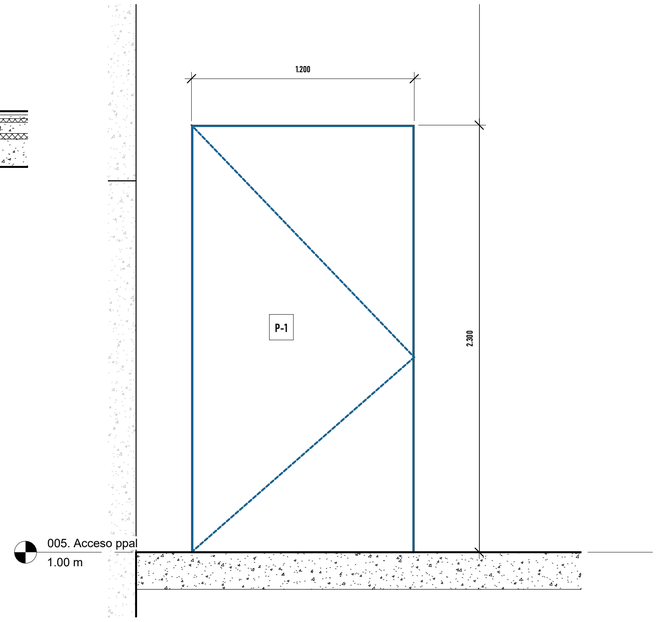

Puerta Acceso 1.20m - JALO_PUERTA ABATIBLE
Ancho 1.200 - Alto 2.300 - Antepecho 0.000 - Dintel 2.300 m
Muro 0.100 m - Materiales: Wood Sheathing, Chipboard

Cotas en metros (0.001 m) sobre geometría nativa. Cotas de muros cortina y cápsula del ascensor: referidas a ejes de grilla, extremos y centros de arcos (no asociativas, salvo radios). Alzados vistos desde el interior del local. Elementos compartidos entre locales: un solo cómputo por código.

https://ezeader.myportfolio.com/ezequiel-ader

Consultant
Address
Address
Phone
Fax
e-mail

Consultant
Address
Address
Phone
Fax
e-mail

Consultant
Address
Address
Phone
Fax
e-mail

Consultant
Address
Address
Phone
Fax
e-mail

No.	Description	Date

Angel Luis Brusca

CASA ANGEL

ABR-R4-PB-17

Project number	0001
Date	18 de Agosto, 2025
Drawn by	Author
Checked by	Checker

Hall · ABR

Scale: As indicated

10/23/2026 3:21:12 PM