

CASA ÁNGEL · ABERTURAS · 01. PLANTA ALTA · 05 TOILETTE

Hoja 1 de 1 · 1 elementos: V-151

Planta del local · códigos y anchos 1:15

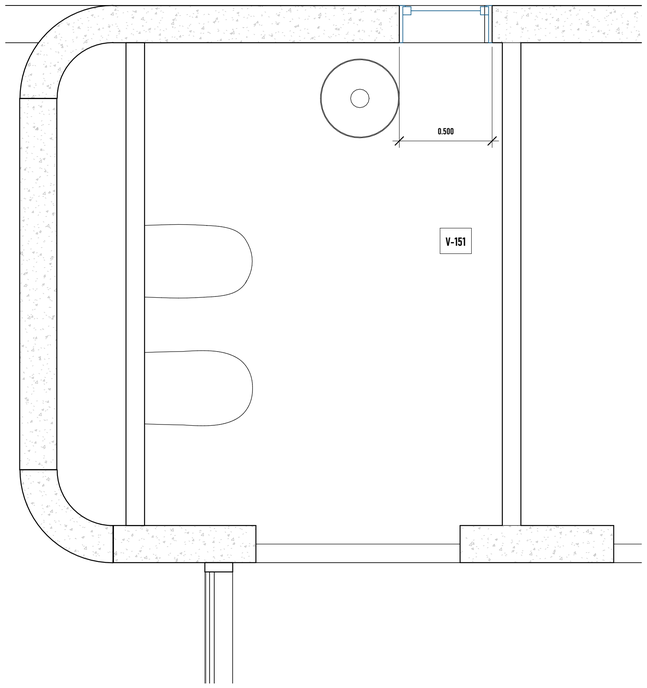

V-151 · alzado interior 1:10

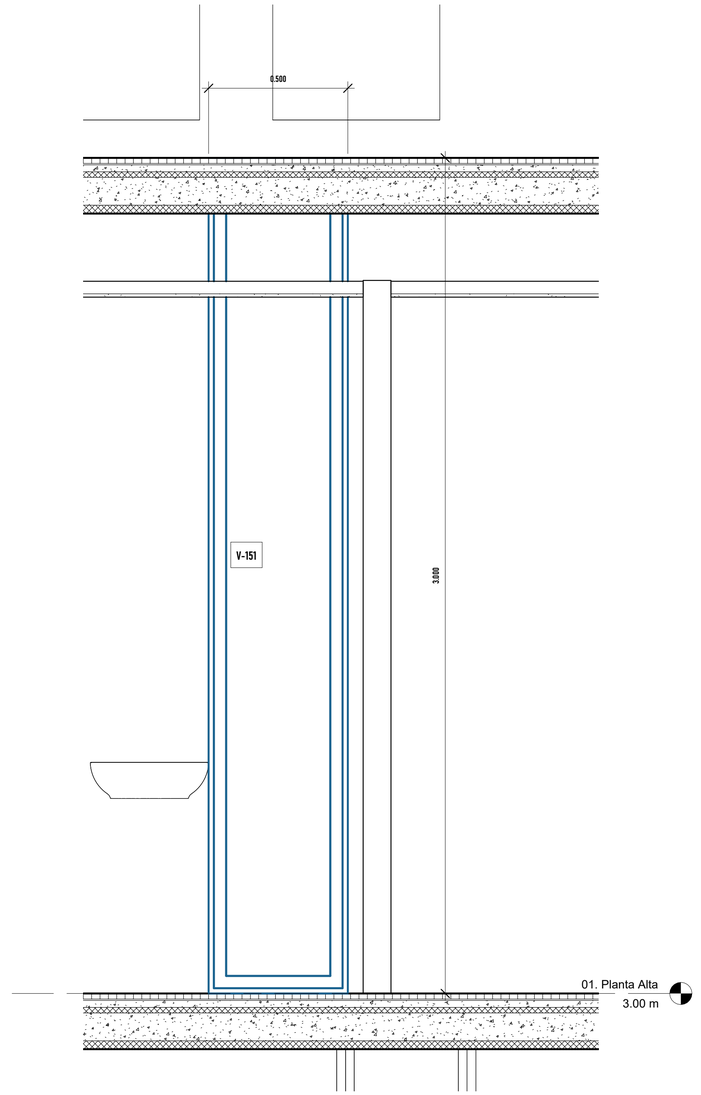

Ventanas Servicios · M_Fixed
Ancho 0.500 · Alto 3.000 · Antepecho 0.000 · Dintel 3.000 m
Muro 0.200 m · Materiales: Glass, Sash

Cotas en metros (0.001 m) sobre geometría nativa. Cotas de muros cortina y cápsula del ascensor: referidas a ejes de grilla, extremos y centros de arcos (no asociativas, salvo radios). Alzados vistos desde el interior del local. Elementos compartidos entre locales: un solo cómputo por código.

https://ezeader.myportfolio.com/ezequiel-ader

Consultant
Address
Address
Phone
Fax
e-mail

Consultant
Address
Address
Phone
Fax
e-mail

Consultant
Address
Address
Phone
Fax
e-mail

Consultant
Address
Address
Phone
Fax
e-mail

No.	Description	Date

Angel Luis Brusca

CASA ANGEL

ABR-R4-PA-05

Project number	0001
Date	18 de Agosto, 2025
Drawn by	Author
Checked by	Checker

Toilette · ABR

Scale: As indicated

10/23/2026 3:22:12 PM