

CASA ÁNGEL · ABERTURAS · 01. PLANTA ALTA · 08 COMEDOR

Hoja 1 de 1 · 2 elementos: V-77, V-135

Planta del local · códigos y anchos 1:20

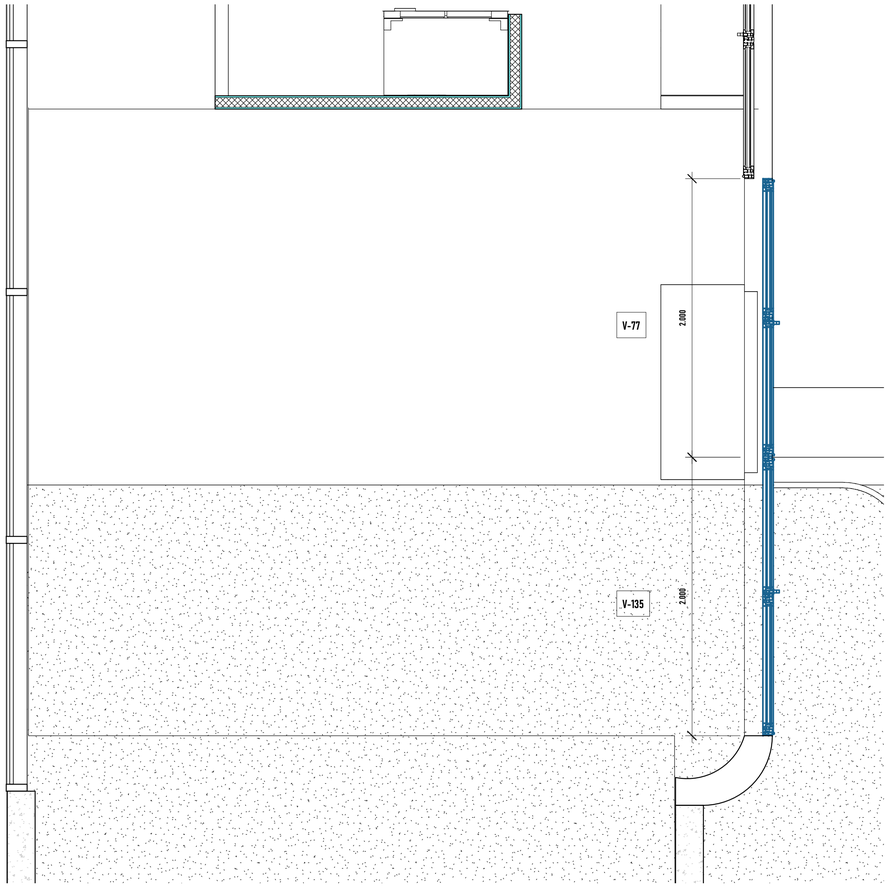


V-77 · alzado interior 1:20

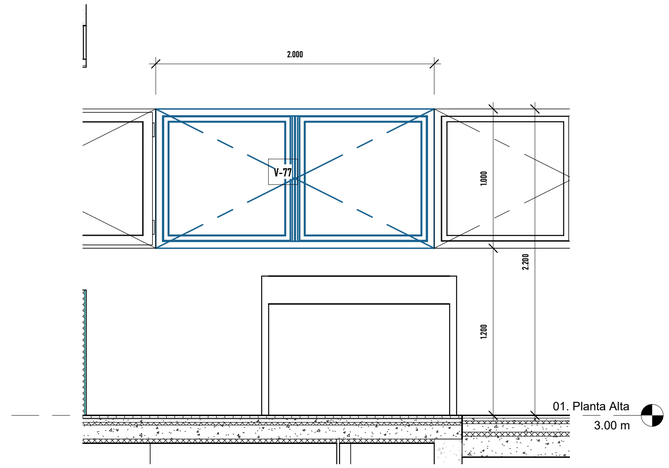

Aluprom 44 - 2 Hojas - Practicable · Ventanas
Ancho 2.000 · Alto 1.000 · Antepecho 1.200 · Dintel 2.200 m
Muro 0.200 m · Materiales: Aluminio, Cristal - Vidrio claro templado, Poliamida

V-135 · alzado interior 1:20

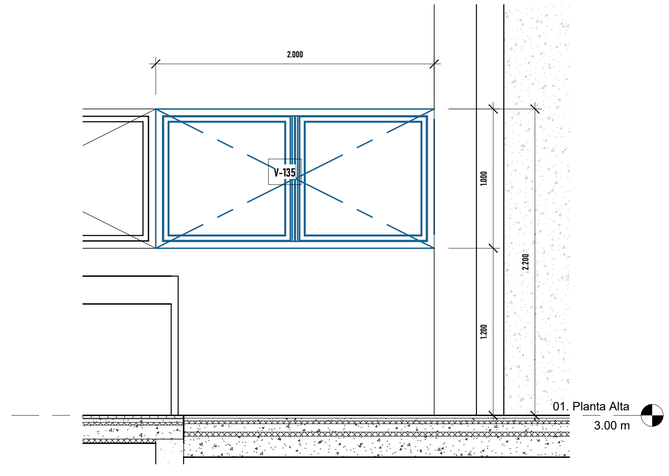

Aluprom 44 - 2 Hojas - Practicable · Ventanas
Ancho 2.000 · Alto 1.000 · Antepecho 1.200 · Dintel 2.200 m
Muro 0.200 m · Materiales: Aluminio, Cristal - Vidrio claro templado, Poliamida

Cotas en metros (0.001 m) sobre geometría nativa. Cotas de muros cortina y cápsula del ascensor: referidas a ejes de grilla, extremos y centros de arcos (no asociativas, salvo radios). Alzados vistos desde el interior del local. Elementos compartidos entre locales: un solo cómputo por código.

https://ezeader.myportfolio.com/ezequiel-ader

Consultant
Address
Address
Phone
Fax
e-mail

Consultant
Address
Address
Phone
Fax
e-mail

Consultant
Address
Address
Phone
Fax
e-mail

Consultant
Address
Address
Phone
Fax
e-mail

No.	Description	Date

Angel Luis Brusca

CASA ANGEL

ABR-R4-PA-08

Project number	0001
Date	18 de Agosto, 2025
Drawn by	Author
Checked by	Checker

Comedor · ABR

Scale 1 : 20

10/23/2026 3:23:29 PM