

CASA ÁNGEL · ABERTURAS · 01. PLANTA ALTA · 09 LIVING

Hoja 1 de 1 · 1 elementos: MC-612302

Planta del local · códigos y anchos 1:40

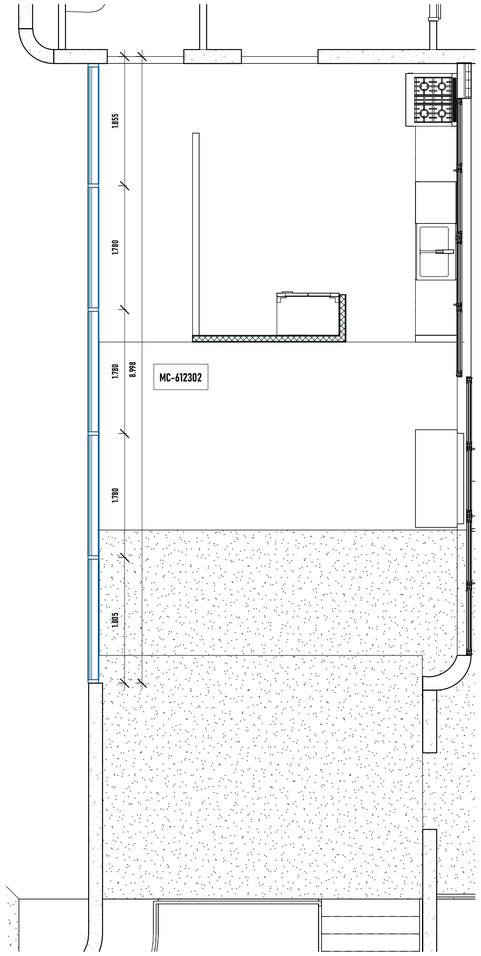

MC-612302 · alzado interior 1:30

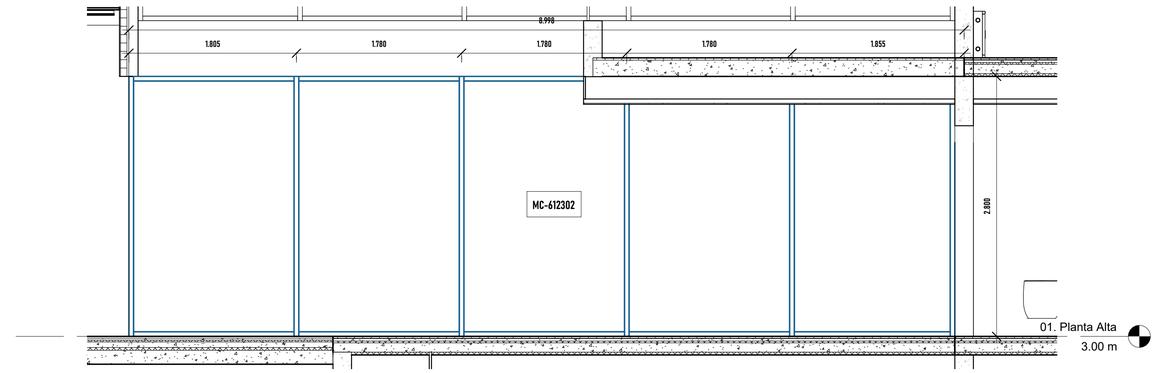

Muro cortina · Ventanales Patio · 5 paneles / 16 montantes
Largo 8.998 · Alto 2.800 · Arranque +0.000 · Superior +2.800 m
Muro 0.025 m
Compartida con: Cocina (computar una vez)

Cotas en metros (0.001 m) sobre geometría nativa. Cotas de muros cortina y cápsula del ascensor: referidas a ejes de grilla, extremos y centros de arcos (no asociativas, salvo radios). Alzados vistos desde el interior del local. Elementos compartidos entre locales: un solo cómputo por código.

https://ezeader.myportfolio.com/ezequiel-ader

Consultant
Address
Address
Phone
Fax
e-mail

Consultant
Address
Address
Phone
Fax
e-mail

Consultant
Address
Address
Phone
Fax
e-mail

Consultant
Address
Address
Phone
Fax
e-mail

No.	Description	Date

Angel Luis Brusca

CASA ANGEL

ABR-R4-PA-09

Project number	0001
Date	18 de Agosto, 2025
Drawn by	Author
Checked by	Checker

Living · ABR

Scale: As indicated

10/23/2026 3:25:56 PM