

CASA ÁNGEL · ABERTURAS · 01. PLANTA ALTA · 02 SALA DE MAQUINAS

Hoja 1 de 1 · 2 elementos: V-121, P-72

Planta del local · códigos y anchos 1:20

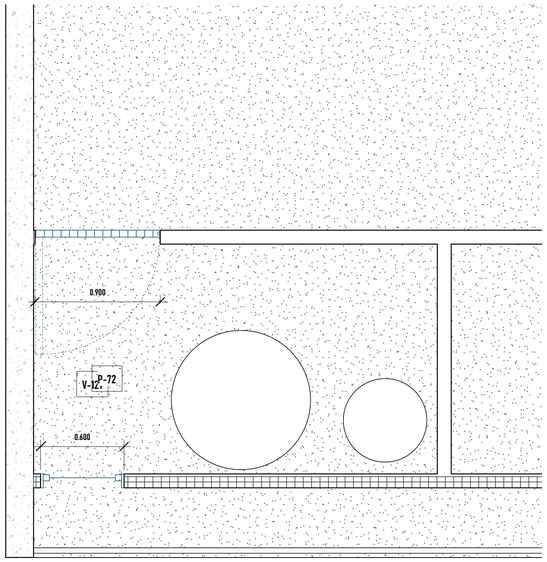


V-121 · alzado interior 1:15

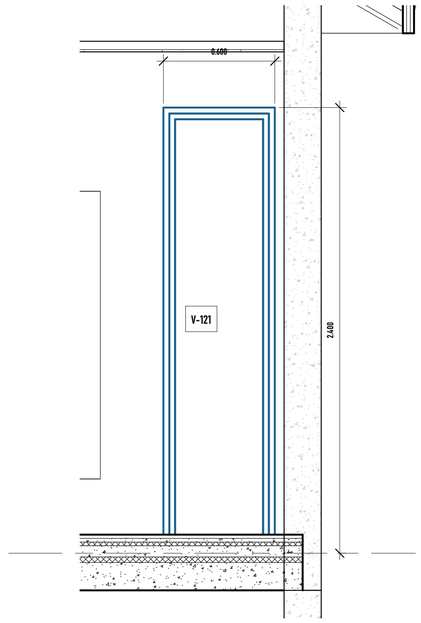

Ventana Cuartos (Muro a techo) - M_Fixed
Ancho 0.600 - Alto 2.400 - Antepecho 0.000 - Dintel 2.400 m
Tipo muro a techo: piso terminado a dintel 2.400 m (verificar con cielorraso)
Muro 0.100 m - Materiales: Glass, Sash

P-72 · alzado interior 1:15

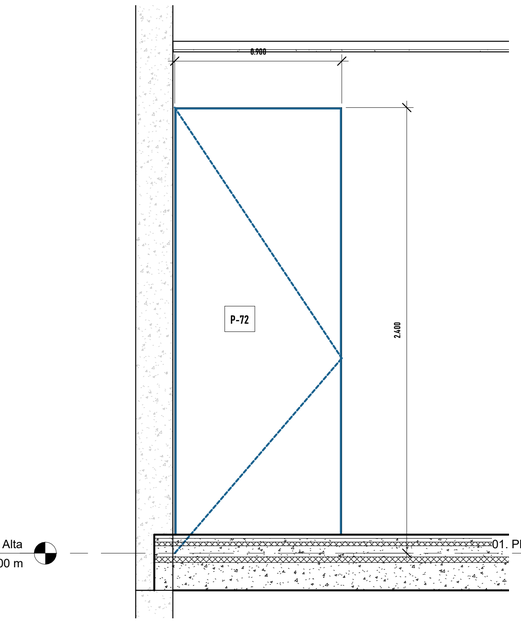

0.90 M - JALO_PUERTA ABATIBLE
Ancho 0.900 - Alto 2.400 - Antepecho 0.000 - Dintel 2.400 m
Muro 0.100 m - Materiales: Puertas
Compartida con: Sala de TV (computar una vez)

Cotas en metros (0.001 m) sobre geometría nativa. Cotas de muros cortina y cápsula del ascensor: referidas a ejes de grilla, extremos y centros de arcos (no asociativas, salvo radios). Alzados vistos desde el interior del local. Elementos compartidos entre locales: un solo cómputo por código.

https://ezeader.myportfolio.com/ezequiel-ader

Consultant
Address
Address
Phone
Fax
e-mail

Consultant
Address
Address
Phone
Fax
e-mail

Consultant
Address
Address
Phone
Fax
e-mail

Consultant
Address
Address
Phone
Fax
e-mail

No.	Description	Date

Angel Luis Brusca

CASA ANGEL

ABR-R4-PA-02

Project number	0001
Date	18 de Agosto, 2025
Drawn by	Author
Checked by	Checker

Sala de Maquinas · ABR

Scale: As indicated

10/23/2025 6:17 PM