
CASA ÁNGEL · ESTRUCTURA · FICHA MH-PE-01


MH-PE-01 · 9,00 × 0,60 · e 20 · Armadura: a definir por el calculista.

MH-PE-01 · planta 1:30

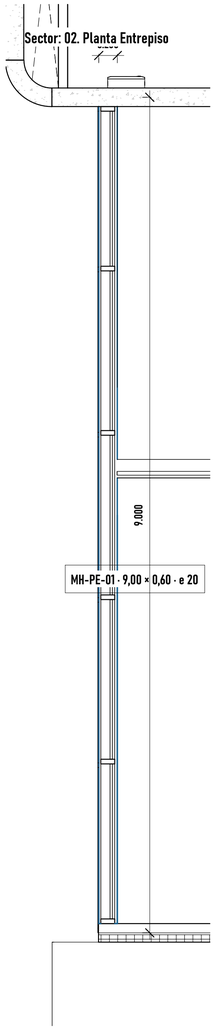


MH-PE-01 · vista (alzado) 1:30


Sector: 02. Planta Entrepiso

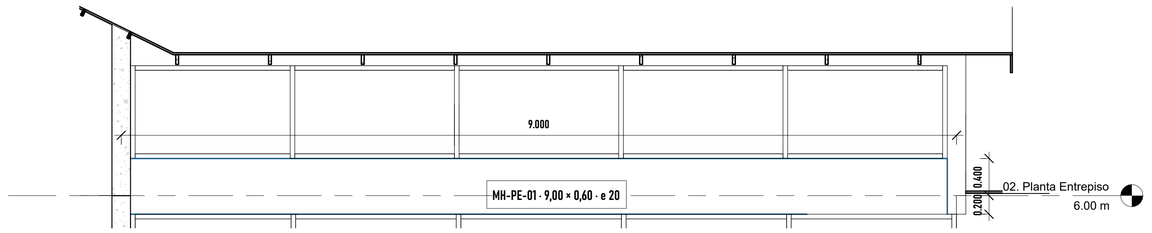

MH-PE-01 · corte 1:30

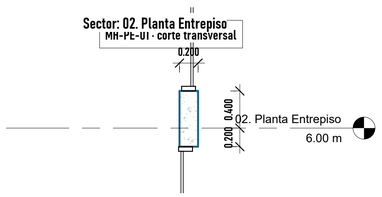

MH-PE-01 · axonométrica 1:30

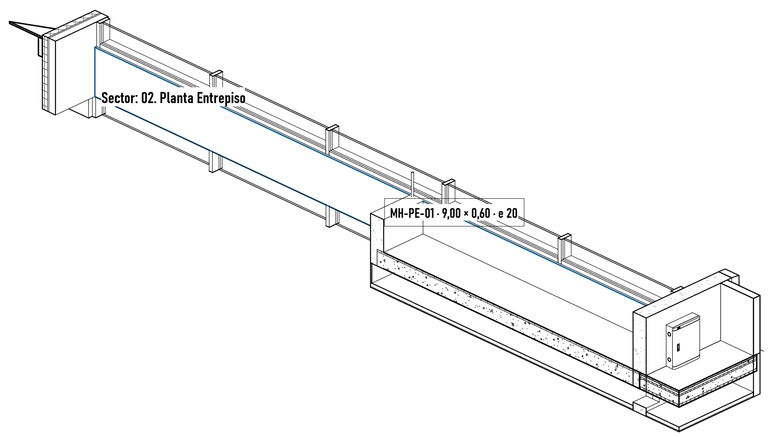

MH-PE-01 · 9,00 × 0,60 · e 20
Hormigón armado (tipo Muro Hormigón 20cm)
Largo 9,00 m · Alto 0,60 m · Espesor 0,20 m · Área 5,34 m² · Volumen 1,07 m³
Armadura: a definir por el calculista.

Ficha de elemento estructural: geometría nativa, cotas en metros (ancladas a extremos, no asociativas). Códigos como anotación. Armadura: a definir por el calculista.

https://ezeader.myportfolio.com/ezequiel-ader

Consultant
Address
Address
Phone
Fax
e-mail

Consultant
Address
Address
Phone
Fax
e-mail

Consultant
Address
Address
Phone
Fax
e-mail

Consultant
Address
Address
Phone
Fax
e-mail

No.	Description	Date

Angel Luis Brusca

CASA ANGEL

EST-F-MH-PE-01

Project number	0001
Date	18 de Agosto, 2025
Drawn by	Author
Checked by	Checker

Estructura · F-MH-PE-01

Scale 1 : 30

10/23/2025 5:30 PM