
# CASA ÁNGEL · ESTRUCTURA · FUNDACIÓN · PLATEA PB

**Platea de fundación PL-01  1:60**

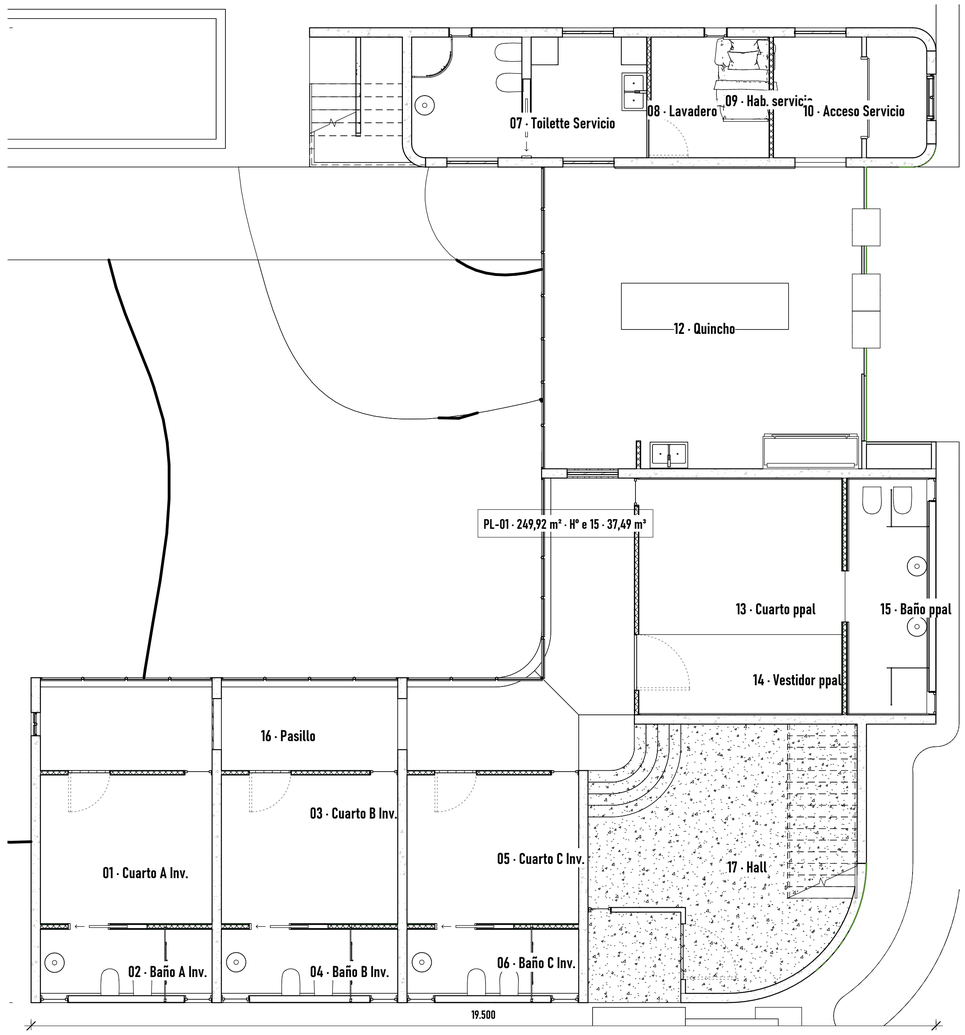


**PL-01 · 249,92 m² · Hº e 15 · 37,49 m³ · resto de fundaciones: no modelado / a definir**

**Estructura: documentación sobre geometría nativa. Códigos MH/VE/LO/PL solo como anotación (no se escribieron en el modelo). Cotas en metros; largos y vanos anclados a extremos (no asociativos). Losas LO1.00 de PA/PE: a confirmar.**

https://ezeader.myportfolio.com/ezequiel-ader


Consultant
Address
Address
Phone
Fax
e-mail

Consultant
Address
Address
Phone
Fax
e-mail

Consultant
Address
Address
Phone
Fax
e-mail

Consultant
Address
Address
Phone
Fax
e-mail


| No. | Description | Date |
|---|---|---|
| | | |

Angel Luis Brusca

CASA ANGEL

EST-FU-01

| | |
|---|---|
| Project number | 0001 |
| Date | 18 de Agosto, 2025 |
| Drawn by | Author |
| Checked by | Checker |

Estructura · FU-01

Scale 1 : 60

10/23/2026 6:26:50 PM