
CASA ÁNGEL · ESTRUCTURA · ALZADOS · 01. PLANTA ALTA · 2/6


Alzados de muros y encadenados · MH-PA-04, MH-PA-05, MH-PA-06

MH-PA-04 · alzado 1:25

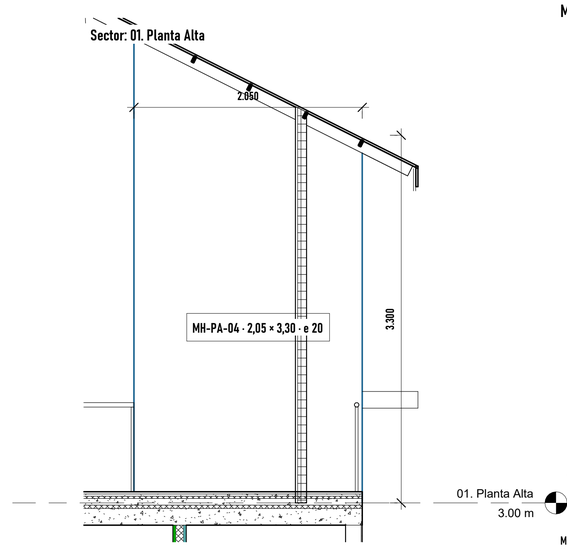


MH-PA-04 · 2,05 × 3,30 · e 20
Hormigón armado (tipo Muro Hormigón 20cm)

MH-PA-05 · alzado 1:25

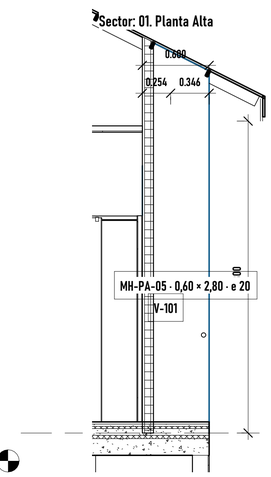

MH-PA-05 · 0,60 × 2,80 · e 20
Hormigón armado (tipo Muro Hormigón 20cm)

MH-PA-06 · alzado 1:25

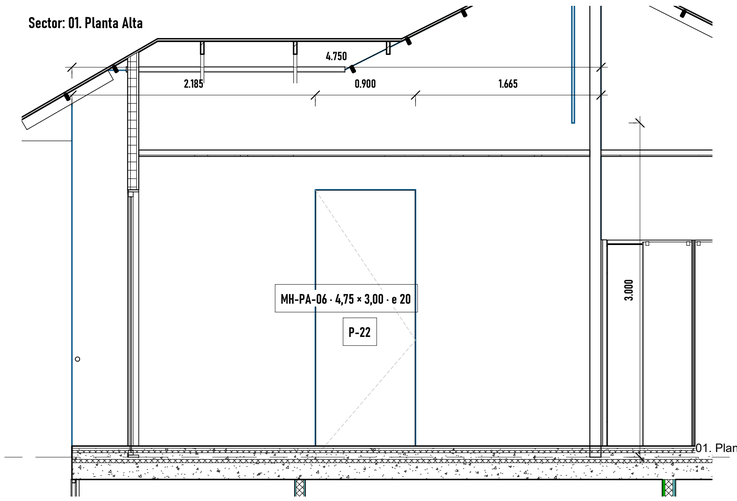

MH-PA-06 · 4,75 × 3,00 · e 20
Hormigón armado (tipo Muro Hormigón 20cm)

Estructura: documentación sobre geometría nativa. Códigos MH/VE/LO/PL solo como anotación (no se escribieron en el modelo). Cotas en metros; largos y vanos anclados a extremos (no asociativos). Losas L01.00 de PA/PE: a confirmar.

https://ezeader.myportfolio.com/ezequiel-ader

Consultant
Address
Address
Phone
Fax
e-mail

Consultant
Address
Address
Phone
Fax
e-mail

Consultant
Address
Address
Phone
Fax
e-mail

Consultant
Address
Address
Phone
Fax
e-mail

No.	Description	Date

Angel Luis Brusca

CASA ANGEL

EST-SEC-PA-02

Project number	0001
Date	18 de Agosto, 2025
Drawn by	Author
Checked by	Checker

Estructura · SEC-PA-02

Scale 1 : 25

10/23/2025 7:21 PM