
CASA ÁNGEL · ESTRUCTURA · ALZADOS · 01. PLANTA ALTA · 6/6


Alzados de muros y encadenados · MH-PA-16, MH-PA-17, VE-PA-01

MH-PA-16 · alzado 1:40

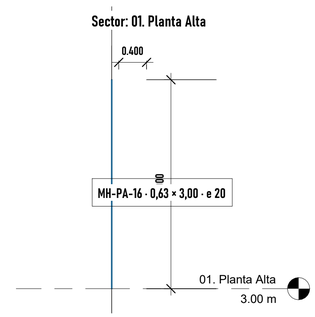


MH-PA-16 · 0,63 × 3,00 · e 20
Hormigón armado (tipo Muro Hormigón 20cm)

MH-PA-17 · alzado 1:40

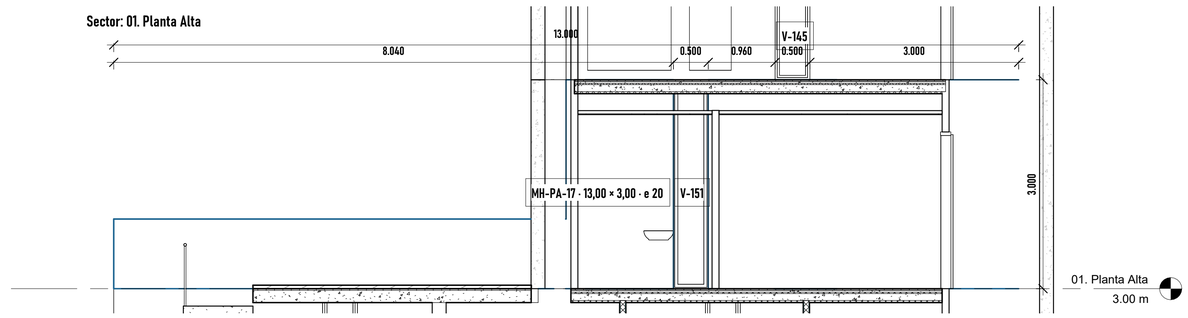

MH-PA-17 · 13,00 × 3,00 · e 20
Hormigón armado (tipo Muro Hormigón 20cm)

VE-PA-01 · alzado 1:40

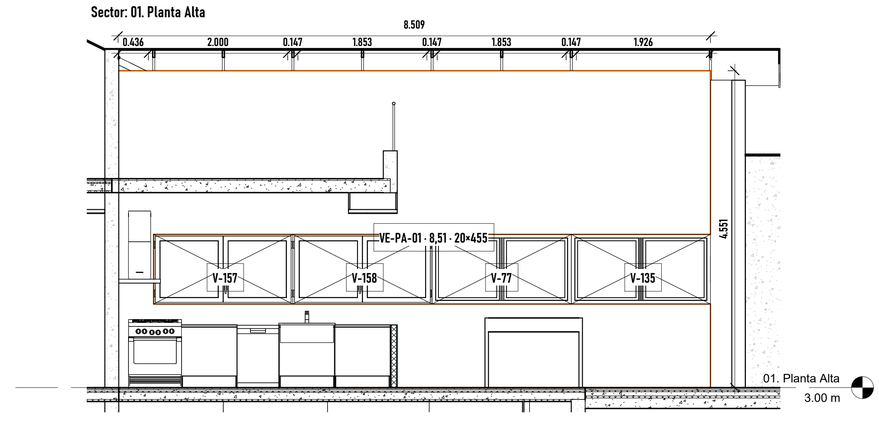

VE-PA-01 · 8,51 · 20×455
VIGA encuentro 2 techos, revestimiento fachada (modelado como muro)

Estructura: documentación sobre geometría nativa. Códigos MH/VE/LO/PL solo como anotación (no se escribieron en el modelo). Cotas en metros; largos y vanos anclados a extremos (no asociativos). Losas LO1.00 de PA/PE: a confirmar.

https://ezeader.myportfolio.com/ezequiel-ader

Consultant
Address
Address
Phone
Fax
e-mail

Consultant
Address
Address
Phone
Fax
e-mail

Consultant
Address
Address
Phone
Fax
e-mail

Consultant
Address
Address
Phone
Fax
e-mail

No.	Description	Date

Angel Luis Brusca

CASA ANGEL

EST-SEC-PA-06

Project number	0001
Date	18 de Agosto, 2025
Drawn by	Author
Checked by	Checker

Estructura · SEC-PA-06

Scale 1 : 40

10/23/2025 11:19 PM