
CASA ÁNGEL · ESTRUCTURA · ALZADOS · 00. PLANTA BAJA · 3/5


Alzados de muros y encadenados · MH-PB-11, MH-PB-12, MH-PB-13, MH-PB-14, MH-PB-15

MH-PB-11 · alzado 1:50

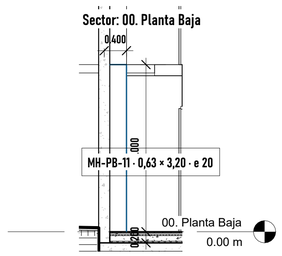


MH-PB-11 · 0,63 × 3,20 · e 20
Hormigón armado (tipo Muro Hormigón 20cm)

MH-PB-12 · alzado 1:50

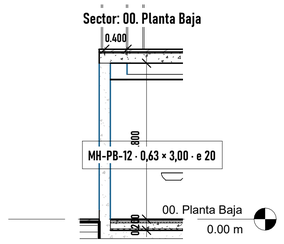


MH-PB-12 · 0,63 × 3,00 · e 20
Hormigón armado (tipo Muro Hormigón 20cm)

MH-PB-13 · alzado 1:50

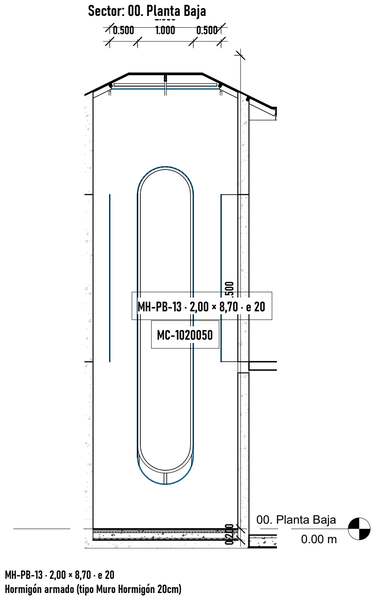


MH-PB-13 · 2,00 × 8,70 · e 20
Hormigón armado (tipo Muro Hormigón 20cm)

MH-PB-14 · alzado 1:50

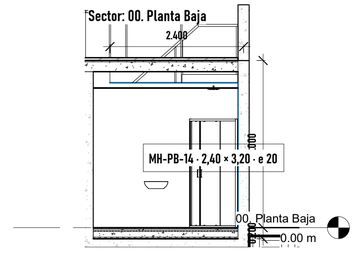

MH-PB-14 · 2,40 × 3,20 · e 20
Hormigón armado (tipo Muro Hormigón 20cm)

MH-PB-15 · alzado 1:50

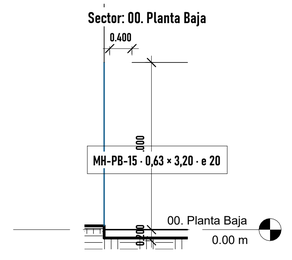

MH-PB-15 · 0,63 × 3,20 · e 20
Hormigón armado (tipo Muro Hormigón 20cm)

Estructura: documentación sobre geometría nativa. Códigos MH/VE/LO/PL solo como anotación (no se escribieron en el modelo). Cotas en metros; largos y vanos anclados a extremos (no asociativos). Losas LO1.00 de PA/PE: a confirmar.

https://ezeader.myportfolio.com/ezequiel-ader

Consultant
Address
Address
Phone
Fax
e-mail

Consultant
Address
Address
Phone
Fax
e-mail

Consultant
Address
Address
Phone
Fax
e-mail

Consultant
Address
Address
Phone
Fax
e-mail

No.	Description	Date

Angel Luis Brusca

CASA ANGEL

EST-SEC-PB-03

Project number	0001
Date	18 de Agosto, 2025
Drawn by	Author
Checked by	Checker

Estructura · SEC-PB-03

Scale 1 : 50

10/23/2025 11:02 PM