

CASA ÁNGEL · ESTRUCTURA · FICHA PL-02 · AMPLIACIÓN DE PLATEA

PL-02: platea H°A° 15 cm bajo LO-PB-01 · 124,12 m² · H° 18,62 m³ · ver EST-FU-01

PL-02 · planta 1:75

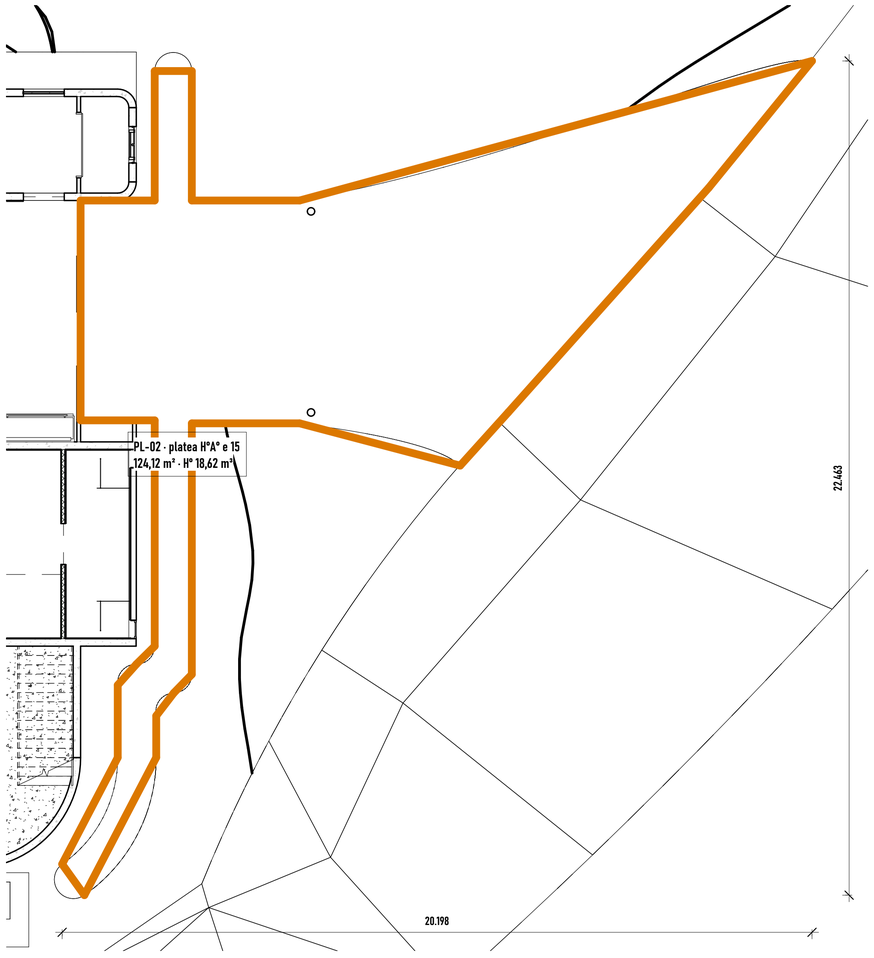

Corte tipo · platea y paquete de piso 1:10

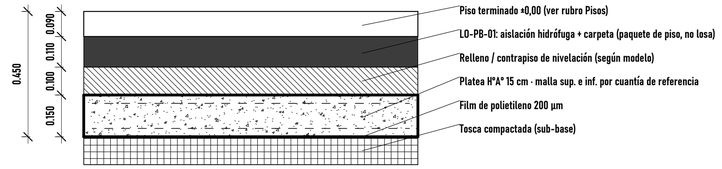

Niveles del modelo: platea −0,45 / −0,20 (tipo «Platea PB 15CM»: tosca + film + H°) · LO-PB-01 −0,20 / −0,09 (R31) · NPT +0,00

PL-02

Naranja: PL-02 ampliación de platea (R31)
Tipo «Platea PB 15CM»: tosca + film + H°A° 15
Nivel superior −0,20 · fondo −0,45
Área 124,12 m² · perímetro 86,08 m
Hormigón: 124,12 m² × 0,15 = 18,62 m³
Volumen del tipo (0,25 total): 31,03 m³
Encima: LO-PB-01 paquete de piso 11 cm (sin H°)
Armadura: malla sup. e inf. por cuantía de referencia

Estructura R31 (archivo de documentación con el modelo principal vinculado). Toda la PB apoya sobre platea H°A° 15 cm (PL-01 + ampliación PL-02 R31) sobre film y tosca compactada; LO-PB-01 se documenta como paquete de piso. Armadura por cuantía de referencia hasta el cálculo. Cotas en metros.

https://ezeader.myportfolio.com/ezequiel-ader

Consultant
Address
Address
Phone
Fax
e-mail

Consultant
Address
Address
Phone
Fax
e-mail

Consultant
Address
Address
Phone
Fax
e-mail

Consultant
Address
Address
Phone
Fax
e-mail

No.	Description	Date

Angel Luis Brusca

CASA ANGEL

EST-F-PL-02

Project number	0001
Date	18 de Agosto, 2025
Drawn by	Author
Checked by	Checker

Estructura · PL-02

Scale As indicated

10/26/2026 9:47:48 AM