
CASA ÁNGEL · PARRILLA · CONDUCTO DE HUMOS: CORTE ESQUEMÁTICO

D-02a · Conducto: corte esquemático 1:50

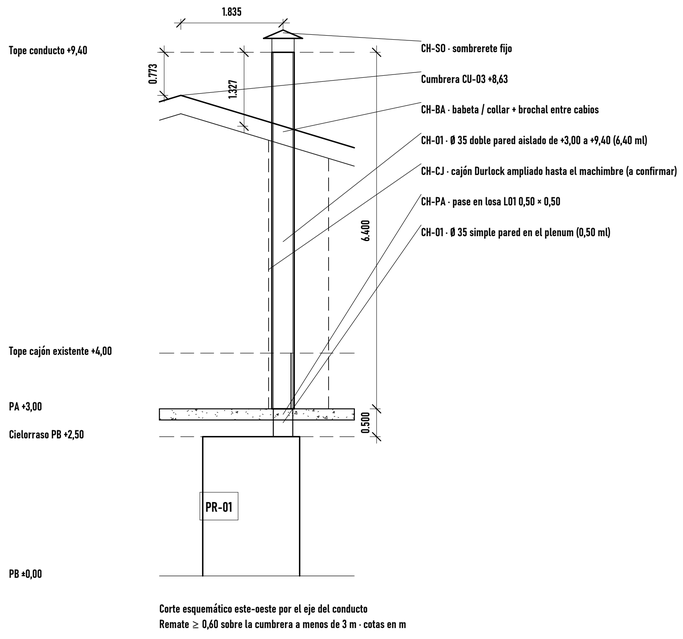

Corte esquemático este-oeste por el eje del conducto
Remate ≥ 0,60 sobre la cumbrera a menos de 3 m · cotas en m

Ø 35: simple pared en el plenum de PB, doble pared aislado desde la PA · remate +9,40 sobre cumbrera +8,63

Parrilla R34 (archivo de documentación con el modelo principal vinculado). Parrilla de obra a medida en el Quincho: boca 1,50 m, hogar a +0,90, campana de ladrillo refractario visto hasta el cielorraso (+2,50), conducto Ø 35 cm por cubierta con sombrerete fijo. Modelada en 3D solo en este archivo: el modelo principal sigue con el equipo K42DB y 2 conductos Ø 25 (no se modificó). Cotas en metros.

https://ezeader.myportfolio.com/ezequiel-ader

Consultant
Address
Address
Phone
Fax
e-mail

Consultant
Address
Address
Phone
Fax
e-mail

Consultant
Address
Address
Phone
Fax
e-mail

Consultant
Address
Address
Phone
Fax
e-mail

No.	Description	Date

Angel Luis Brusca

CASA ANGEL

PAR-D-02

Project number	0001
Date	18 de Agosto, 2025
Drawn by	Author
Checked by	Checker

Parrilla · D-02

Scale 1 : 50

10/26/2026 11:42:39 AM