
CASA ÁNGEL · ABERTURAS · 00. PLANTA BAJA · PLANTA GENERAL

33 aberturas: P-1, V-15, V-35, P-31, V-57, V-69, V-92, V-108, P-59, P-60, V-117, P-63, V-123, V-127, V-131, V-132, MC-1020050, MC-1020586, P-90, MC-1045585, MC-1046251, MC-1046631, MC-1046997, P-93, V-147, V-150, P-94, V-154, P-95, P-96, V-155, MC-2275029, MC-2295997

Planta general · 00. Planta Baja 1:75

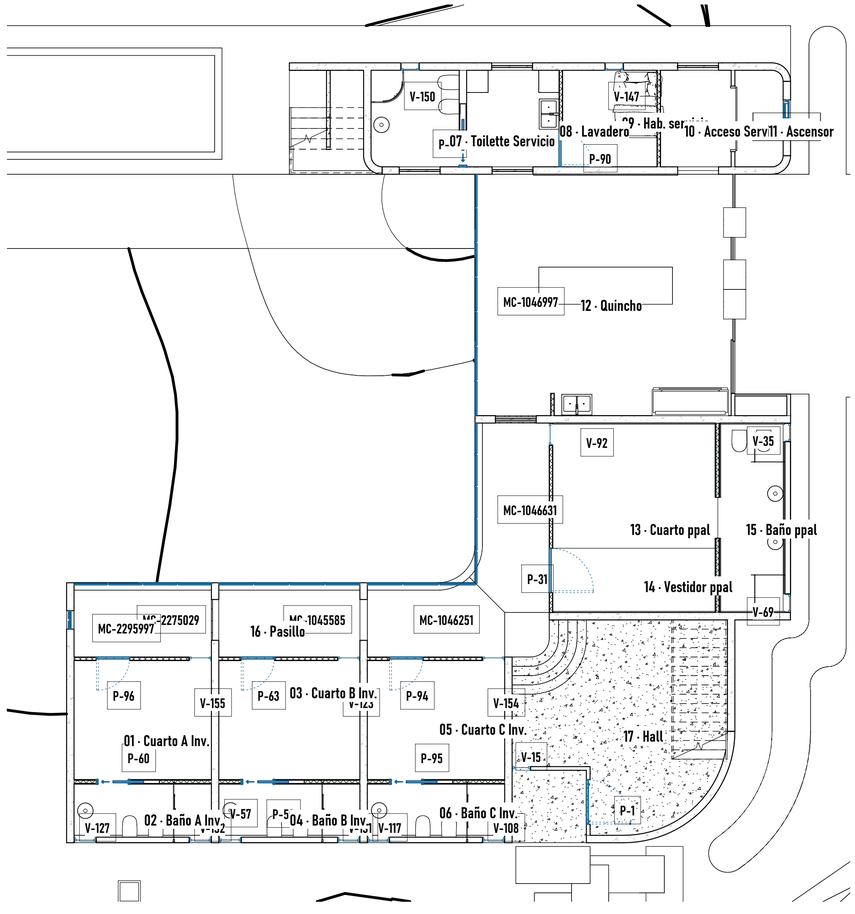

https://ezeader.myportfolio.com/ezequiel-ader

Consultant
Address
Address
Phone
Fax
e-mail

Consultant
Address
Address
Phone
Fax
e-mail

Consultant
Address
Address
Phone
Fax
e-mail

Consultant
Address
Address
Phone
Fax
e-mail

No.	Description	Date

Angel Luis Brusca

CASA ANGEL

ABR-R4-PB-00

Project number	0001
Date	18 de Agosto, 2025
Drawn by	Author
Checked by	Checker

Planta general · ABR

Scale 1 : 75

10/23/2026 5:24:06 PM