CASA ÁNGEL · CUBIERTA · PLANTA DE TECHOS POR FALDÓN

Planta de techos por faldón 1:75

Referencias


Verde: alero con canaleta
Círculo azul: bajada Ø100 (1 c/ ≤10 ml)
Roja: cumbrera ventilada
Naranja: limatesa · azul: limahoya
Violeta: encuentro con muro (babeta)
Gris: borde libre (fascia)
Flecha: sentido de la pendiente
(nn): local con machimbre visto

Faldones (aguas)

CU-01 · alero +6,00 · cumbrera +7,50 · 128,62 m²
CU-01a 47,46 m² 26,7°
CU-01b 35,36 m² 26,7°
CU-01c 20,06 m² 26,7°
CU-01d 16,69 m² 26,7°
CU-01e 9,01 m² 30,0°
CU-02 · alero +6,00 · cumbrera +7,51 · 21,09 m²
CU-02a 7,86 m² 30,0°
CU-02b 6,62 m² 30,0°
CU-02c 6,61 m² 30,0°
CU-03 · alero +7,50 · cumbrera +8,48 · 98,73 m²
CU-03a 34,01 m² 16,8°
CU-03b 34,01 m² 16,8°
CU-03c 14,91 m² 26,1°
CU-03d 3,85 m² 30,0°
CU-03e 3,85 m² 30,0°
CU-03f 3,85 m² 26,1°
CU-03g 3,84 m² 26,1°

Machimbre visto

17 Hall
01 Sala de TV
08 Comedor
03 Playroom
03 Atelier
01 SM
02 Hall PE
09 Living
10 Puente

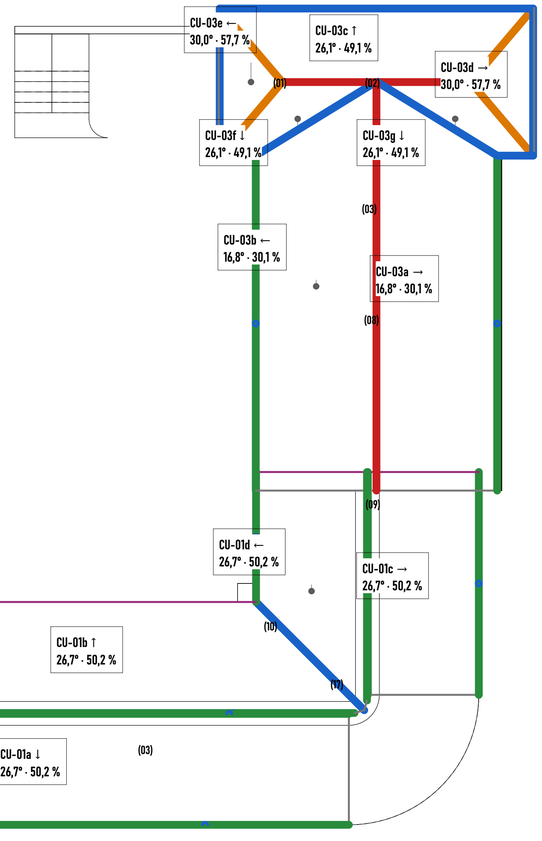

Aguas, pendientes, cumbreras, limatesas, limahoyas, canaletas y bajadas · locales con machimbre visto

Cubierta R30 (archivo de documentación con el modelo principal vinculado). Paquete modelado: teja 20 · cámara ventilada 25 (contraclavaderas) · membrana respirable · EPS 75 entre clavaderas · barrera de vapor · machimbre 3/4" visto. Cabios LVL 5×15 c/0,96; vigas VC LVL 6×20 a verificar por el calculista. Cotas en metros.

https://ezeader.myportfolio.com/ezequiel-ader

Consultant
Address
Address
Phone
Fax
e-mail

Consultant
Address
Address
Phone
Fax
e-mail

Consultant
Address
Address
Phone
Fax
e-mail

Consultant
Address
Address
Phone
Fax
e-mail

No.	Description	Date

Angel Luis Brusca

CASA ANGEL

CUB-P-01

Project number	0001
Date	18 de Agosto, 2025
Drawn by	Author
Checked by	Checker

Cubierta · P-01

Scale 1 : 75

10/25/2026 12:03:06 AM