
CASA ÁNGEL · ESTRUCTURA · ALZADOS · 00. PLANTA BAJA · 1/5


Alzados de muros y encadenados · MH-PB-01, MH-PB-02, MH-PB-03, MH-PB-04, MH-PB-05

MH-PB-01 · alzado 1:40

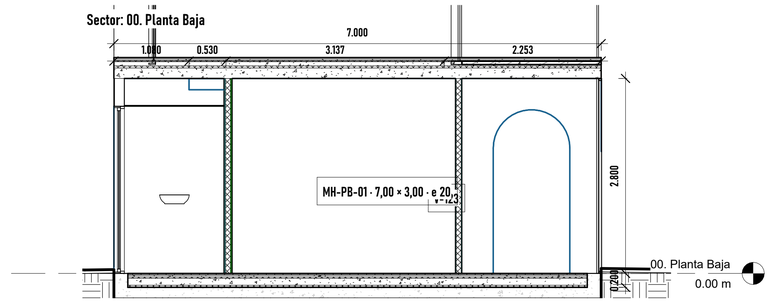


MH-PB-01 · 7,00 × 3,00 · e 20
Hormigón armado (tipo Muro Hormigón 20cm)

MH-PB-02 · alzado 1:40

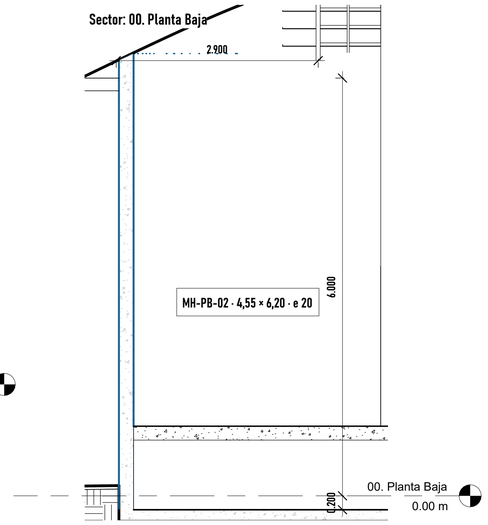


MH-PB-02 · 4,55 × 6,20 · e 20
Hormigón armado (tipo Muro Hormigón 20cm)

MH-PB-03 · alzado 1:40

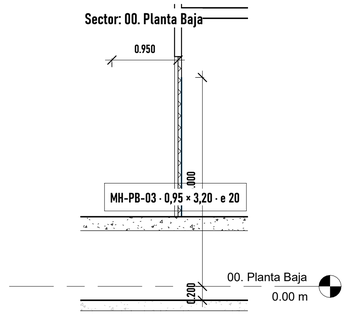


MH-PB-03 · 0,95 × 3,20 · e 20
Hormigón armado (tipo Muro Hormigón 20cm)

MH-PB-04 · alzado 1:40

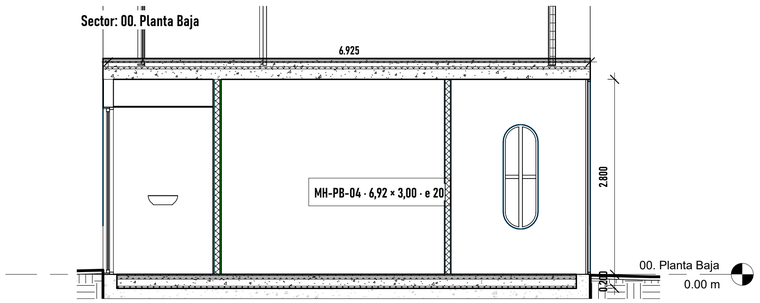

MH-PB-04 · 6,92 × 3,00 · e 20
Hormigón armado (tipo Muro Hormigón 20cm)

MH-PB-05 · alzado 1:40

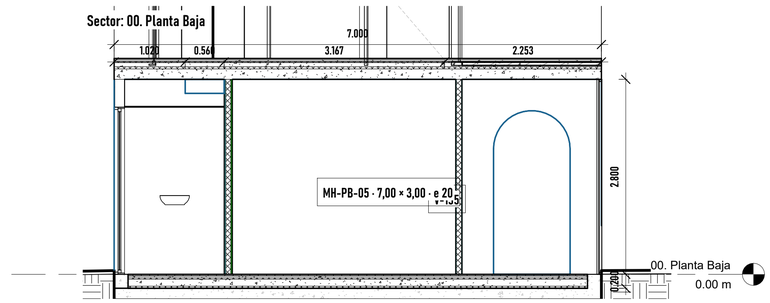

MH-PB-05 · 7,00 × 3,00 · e 20
Hormigón armado (tipo Muro Hormigón 20cm)

Estructura: documentación sobre geometría nativa. Códigos MH/VE/LO/PL solo como anotación (no se escribieron en el modelo). Cotas en metros; largos y vanos anclados a extremos (no asociativos). Losas LO1.00 de PA/PE: a confirmar.

https://ezeader.myportfolio.com/ezequiel-ader

Consultant
Address
Address
Phone
Fax
e-mail

Consultant
Address
Address
Phone
Fax
e-mail

Consultant
Address
Address
Phone
Fax
e-mail

Consultant
Address
Address
Phone
Fax
e-mail

No.	Description	Date

Angel Luis Brusca

CASA ANGEL

EST-SEC-PB-01

Project number	0001
Date	18 de Agosto, 2025
Drawn by	Author
Checked by	Checker

Estructura · SEC-PB-01

Scale 1 : 40

10/23/2026 10:10:58 PM