
CASA ÁNGEL · ESTRUCTURA · PLANTA DE ESTRUCTURA · 00. PLANTA BAJA

Planta de estructura · 00. Planta Baja 1:60

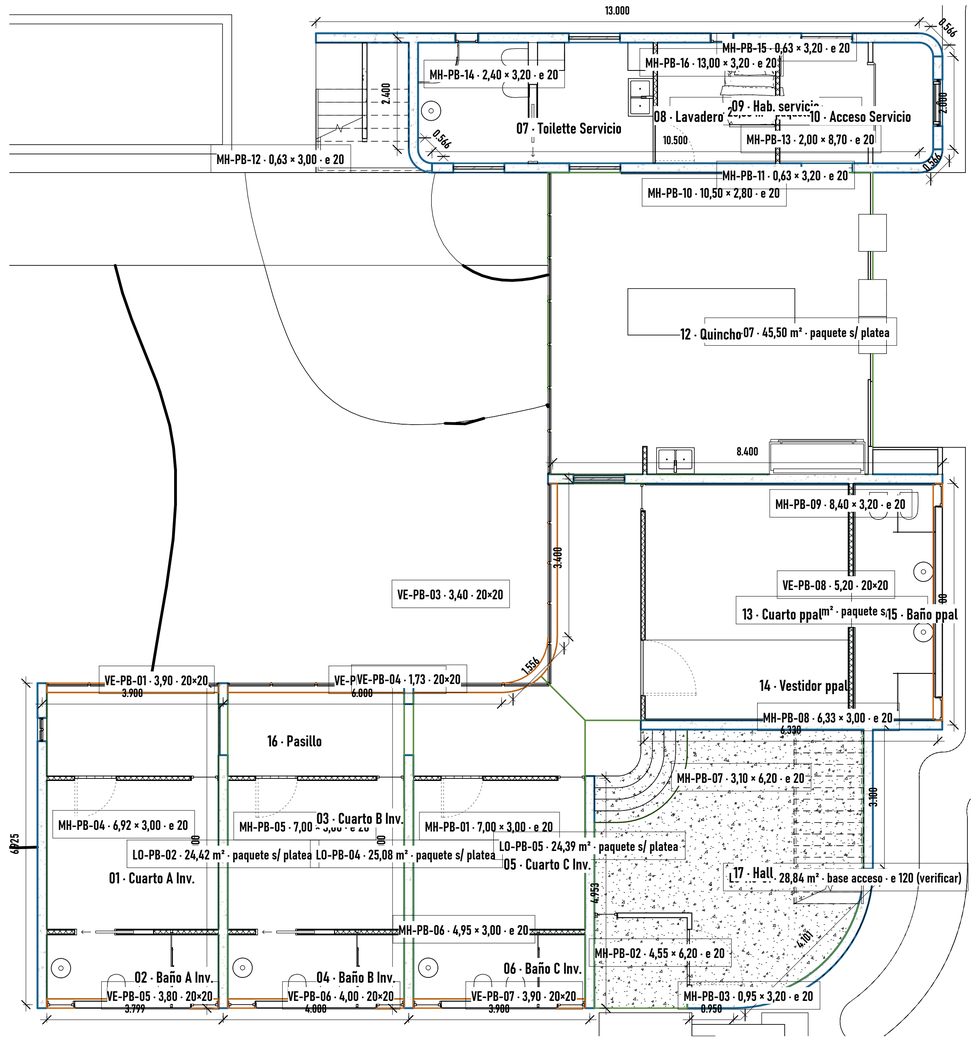

16 muros MH · 49,11 m³ · 7 losas/paquetes · 8 encadenados · fuera del recorte (exterior): LO-PB-01

Estructura: documentación sobre geometría nativa. Códigos MH/VE/LO/PL escritos también en el parámetro Mark del modelo. Cotas en metros; largos y vanos anclados a extremos (no asociativos). Losas L01.00 de PA/PE: a confirmar.

https://ezeader.myportfolio.com/ezequiel-ader

Consultant
Address
Address
Phone
Fax
e-mail

Consultant
Address
Address
Phone
Fax
e-mail

Consultant
Address
Address
Phone
Fax
e-mail

Consultant
Address
Address
Phone
Fax
e-mail

No.	Description	Date

Angel Luis Brusca

CASA ANGEL

EST-PB-01

Project number	0001
Date	18 de Agosto, 2025
Drawn by	Author
Checked by	Checker

Estructura · PB-01

Scale 1 : 60

10/23/2026 7:07:24 PM