
CASA ÁNGEL · ESTRUCTURA · ALZADOS · 00. PLANTA BAJA · 5/5


Alzados de muros y encadenados · VE-PB-05, VE-PB-06, VE-PB-07, VE-PB-08

VE-PB-05 · alzado 1:25

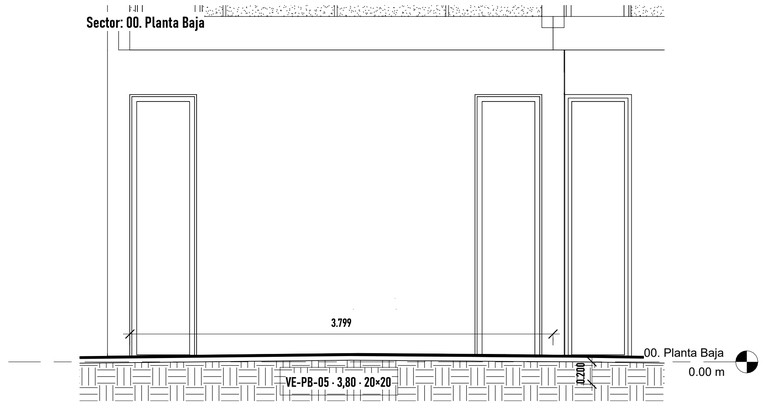


VE-PB-05 · 3,80 · 20×20
Viga de encadenado invertida (modelado como muro)

VE-PB-06 · alzado 1:25

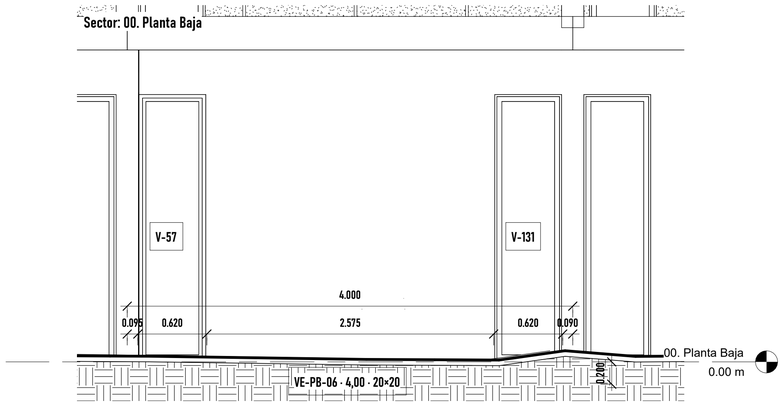


VE-PB-06 · 4,00 · 20×20
Viga de encadenado invertida (modelado como muro)

VE-PB-07 · alzado 1:25

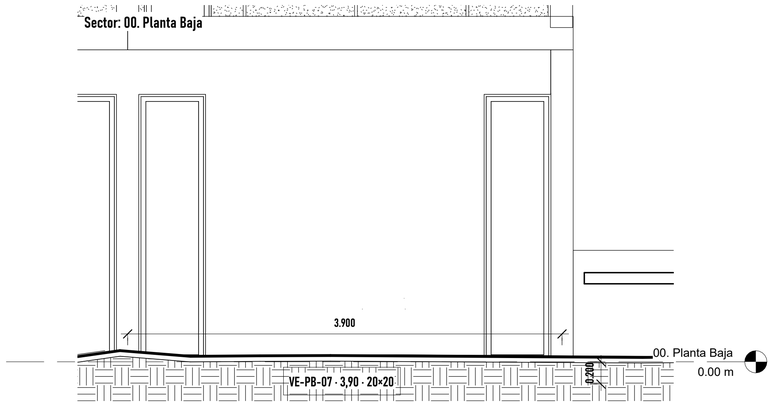

VE-PB-07 · 3,90 · 20×20
Viga de encadenado invertida (modelado como muro)

VE-PB-08 · alzado 1:25

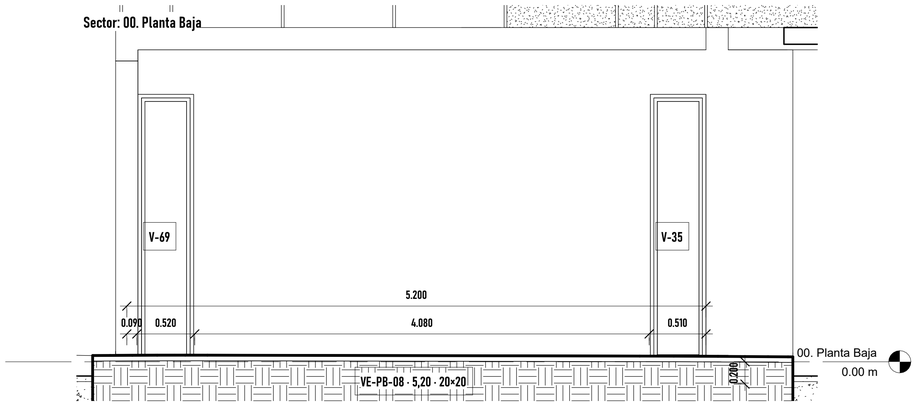

VE-PB-08 · 5,20 · 20×20
Viga de encadenado invertida (modelado como muro)

Estructura: documentación sobre geometría nativa. Códigos MH/VE/LO/PL escritos también en el parámetro Mark del modelo. Cotas en metros; largos y vanos anclados a extremos (no asociativos). Losas L01.00 de PA/PE: a confirmar.

https://ezeader.myportfolio.com/ezequiel-ader

Consultant
Address
Address
Phone
Fax
e-mail

Consultant
Address
Address
Phone
Fax
e-mail

Consultant
Address
Address
Phone
Fax
e-mail

Consultant
Address
Address
Phone
Fax
e-mail

No.	Description	Date

Angel Luis Brusca

CASA ANGEL

EST-SEC-PB-05

Project number	0001
Date	18 de Agosto, 2025
Drawn by	Author
Checked by	Checker

Estructura · SEC-PB-05

Scale 1 : 25

10/23/2025 7:57 PM