
CASA ÁNGEL · PISOS Y ZÓCALOS · FICHA TP-02 · L01.01


TP-02 · L01.01 · alfombra · 127,56 m²

TP-02 · planta (01. Planta Alta) 1:75

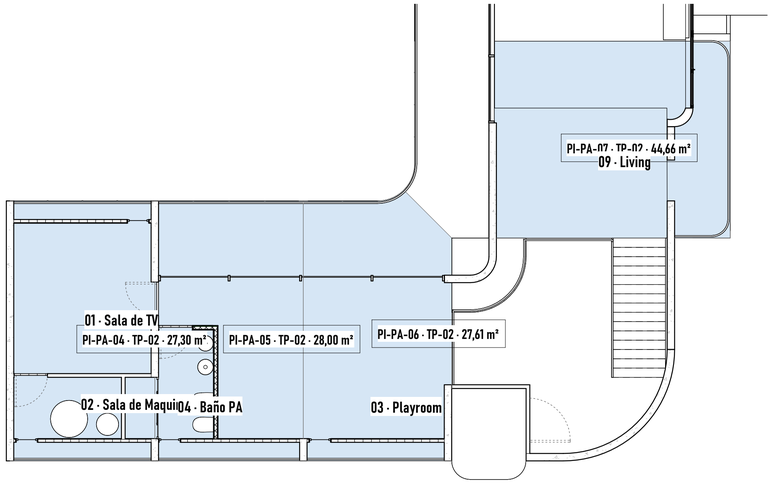


TP-02 · alfombra · 127,56 m²
Paquete: alfombra 2 / Carpeta 2 / EPS 2 / Contrapiso 6 / PLACA EPS . PR 3 / hormigón 15 cm · total 30,00 cm
Locales: 01 Sala de TV (14,99 m²), 02 Sala de Maquinas (4,79 m²), 03 Playroom (28,94 m²), 04 Baño PA (5,81 m²), 09 Living (16,14 m²)
Piezas: PI-PA-04, PI-PA-05, PI-PA-06, PI-PA-07

TP-02 · corte de paquete 1:5

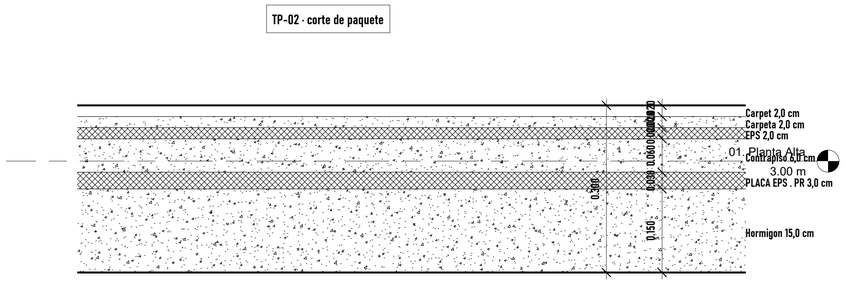

TP-02 · axonométrica 1:40

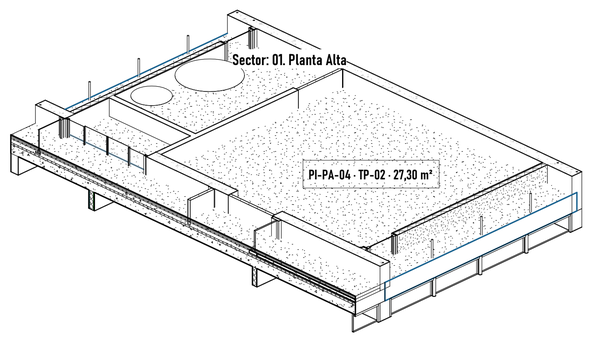

Pisos: paquetes según tipo de piso del modelo; terminación = capa superior. Cotas en metros (no asociativas). Códigos TP/PI/ZO como anotación. Zócalos: solo 5 tramos modelados; el resto se computa por perímetro de local.

https://ezeader.myportfolio.com/ezequiel-ader

Consultant
Address
Address
Phone
Fax
e-mail

Consultant
Address
Address
Phone
Fax
e-mail

Consultant
Address
Address
Phone
Fax
e-mail

Consultant
Address
Address
Phone
Fax
e-mail

No.	Description	Date

Angel Luis Brusca

CASA ANGEL

PIS-F-TP-02

Project number	0001
Date	18 de Agosto, 2025
Drawn by	Author
Checked by	Checker

Pisos · TP-02

Scale As indicated

10/23/2026 7:35:13 PM