
CASA ÁNGEL · PISOS Y ZÓCALOS · FICHA TP-03 · L01.02


TP-03 · L01.02 · madera · 20,37 m²

TP-03 · planta (02. Planta Entrepiso) 1:25

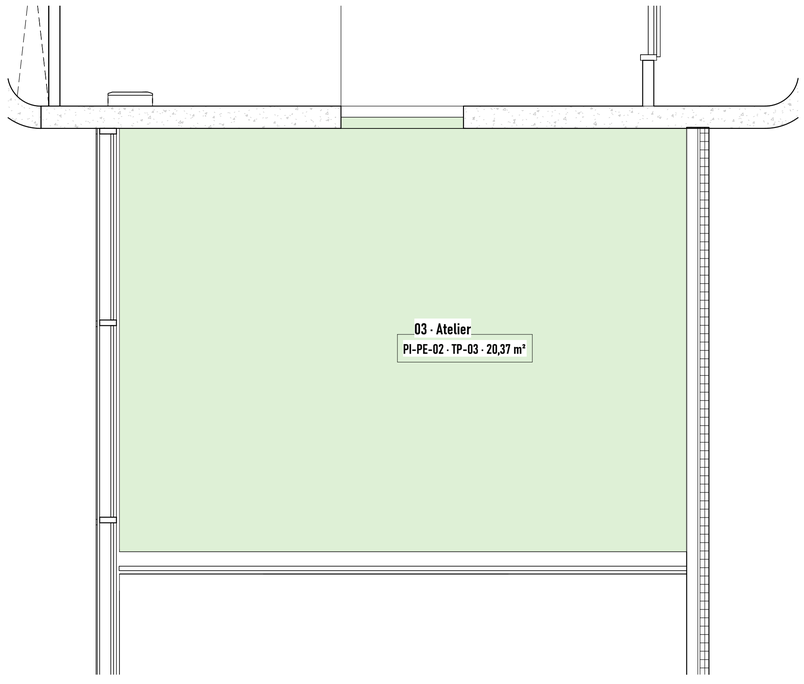


TP-03 · L01.02 · madera · 20,37 m²
Paquete: madera 2,5 / Concrete, Cast-in-Place, Gray 17,5 cm · total 20,00 cm
Locales: 03 Atelier (19,36 m²)
Piezas: PI-PE-02

TP-03 · corte de paquete 1:5

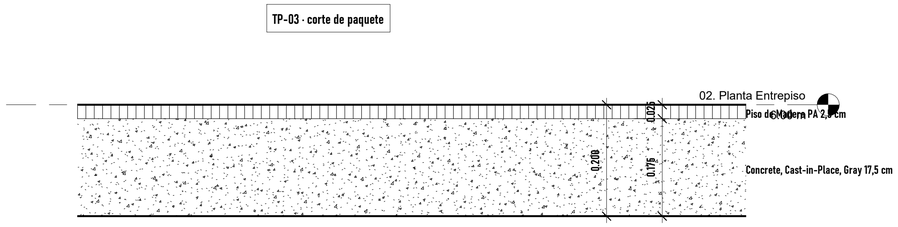

TP-03 · axonométrica 1:30

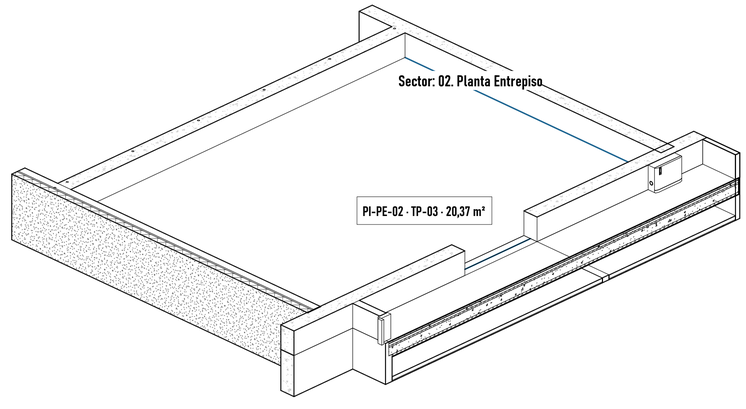

Pisos: paquetes según tipo de piso del modelo; terminación = capa superior. Cotas en metros (no asociativas). Códigos TP/PI/ZO como anotación. Zócalos: solo 5 tramos modelados; el resto se computa por perímetro de local.

https://ezeader.myportfolio.com/ezequiel-ader

Consultant
Address
Address
Phone
Fax
e-mail

Consultant
Address
Address
Phone
Fax
e-mail

Consultant
Address
Address
Phone
Fax
e-mail

Consultant
Address
Address
Phone
Fax
e-mail

No.	Description	Date

Angel Luis Brusca

CASA ANGEL

PIS-F-TP-03

Project number	0001
Date	18 de Agosto, 2025
Drawn by	Author
Checked by	Checker

Pisos · TP-03

Scale As indicated

10/23/2026 7:35:15 PM