
# CASA ÁNGEL · PISOS Y ZÓCALOS · FICHA TP-07 · L05.00


**TP-07 · L05.00 · vinílico · 42,30 m²**

## TP-07 · planta (00. Planta Baja)  1:40

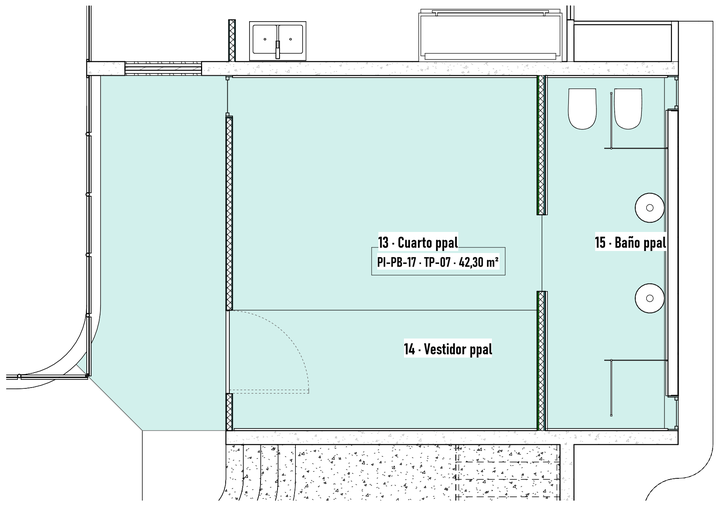



**TP-07 · vinílico · 42,30 m²**
**Paquete: vinílico 2 / Adhesivo 0,5 / Carpeta 2,5 / PLACA EPS . PR 2 / Contrapiso 10 / EPS 3 cm · total 20,00 cm**
**Locales: 13 Cuarto ppal (14,82 m²), 14 Vestidor ppal (7,57 m²), 15 Baño ppal (9,03 m²)**
**Piezas: PI-PB-17**

## TP-07 · corte de paquete  1:5

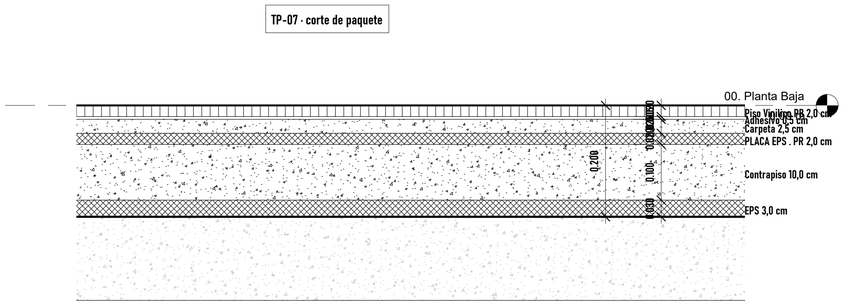


## TP-07 · axonométrica  1:40

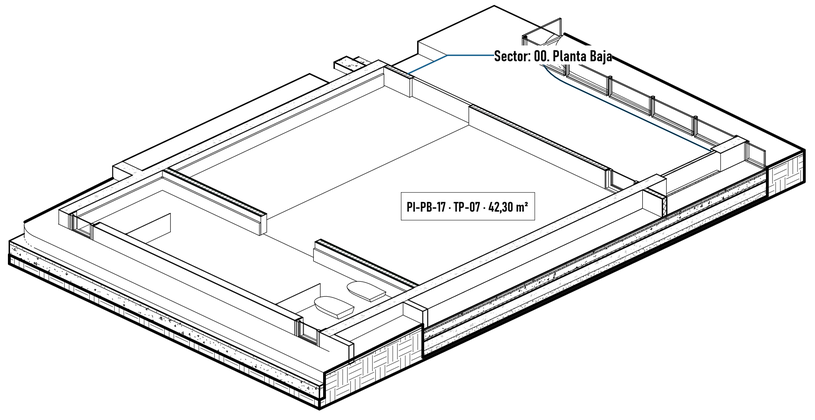


**Pisos: paquetes según tipo de piso del modelo; terminación = capa superior. Cotas en metros (no asociativas). Códigos TP/PI/ZO como anotación. Zócalos: solo 5 tramos modelados; el resto se computa por perímetro de local.**


https://ezeader.myportfolio.com/ezequiel-ader

Consultant
Address
Address
Phone
Fax
e-mail

Consultant
Address
Address
Phone
Fax
e-mail

Consultant
Address
Address
Phone
Fax
e-mail

Consultant
Address
Address
Phone
Fax
e-mail


| No. | Description | Date |
|---|---|---|
| | | |

Angel Luis Brusca

CASA ANGEL

PIS-F-TP-07

| | |
|---|---|
| Project number | 0001 |
| Date | 18 de Agosto, 2025 |
| Drawn by | Author |
| Checked by | Checker |

Pisos · TP-07

Scale  As indicated

10/23/2026 7:35:22 PM